
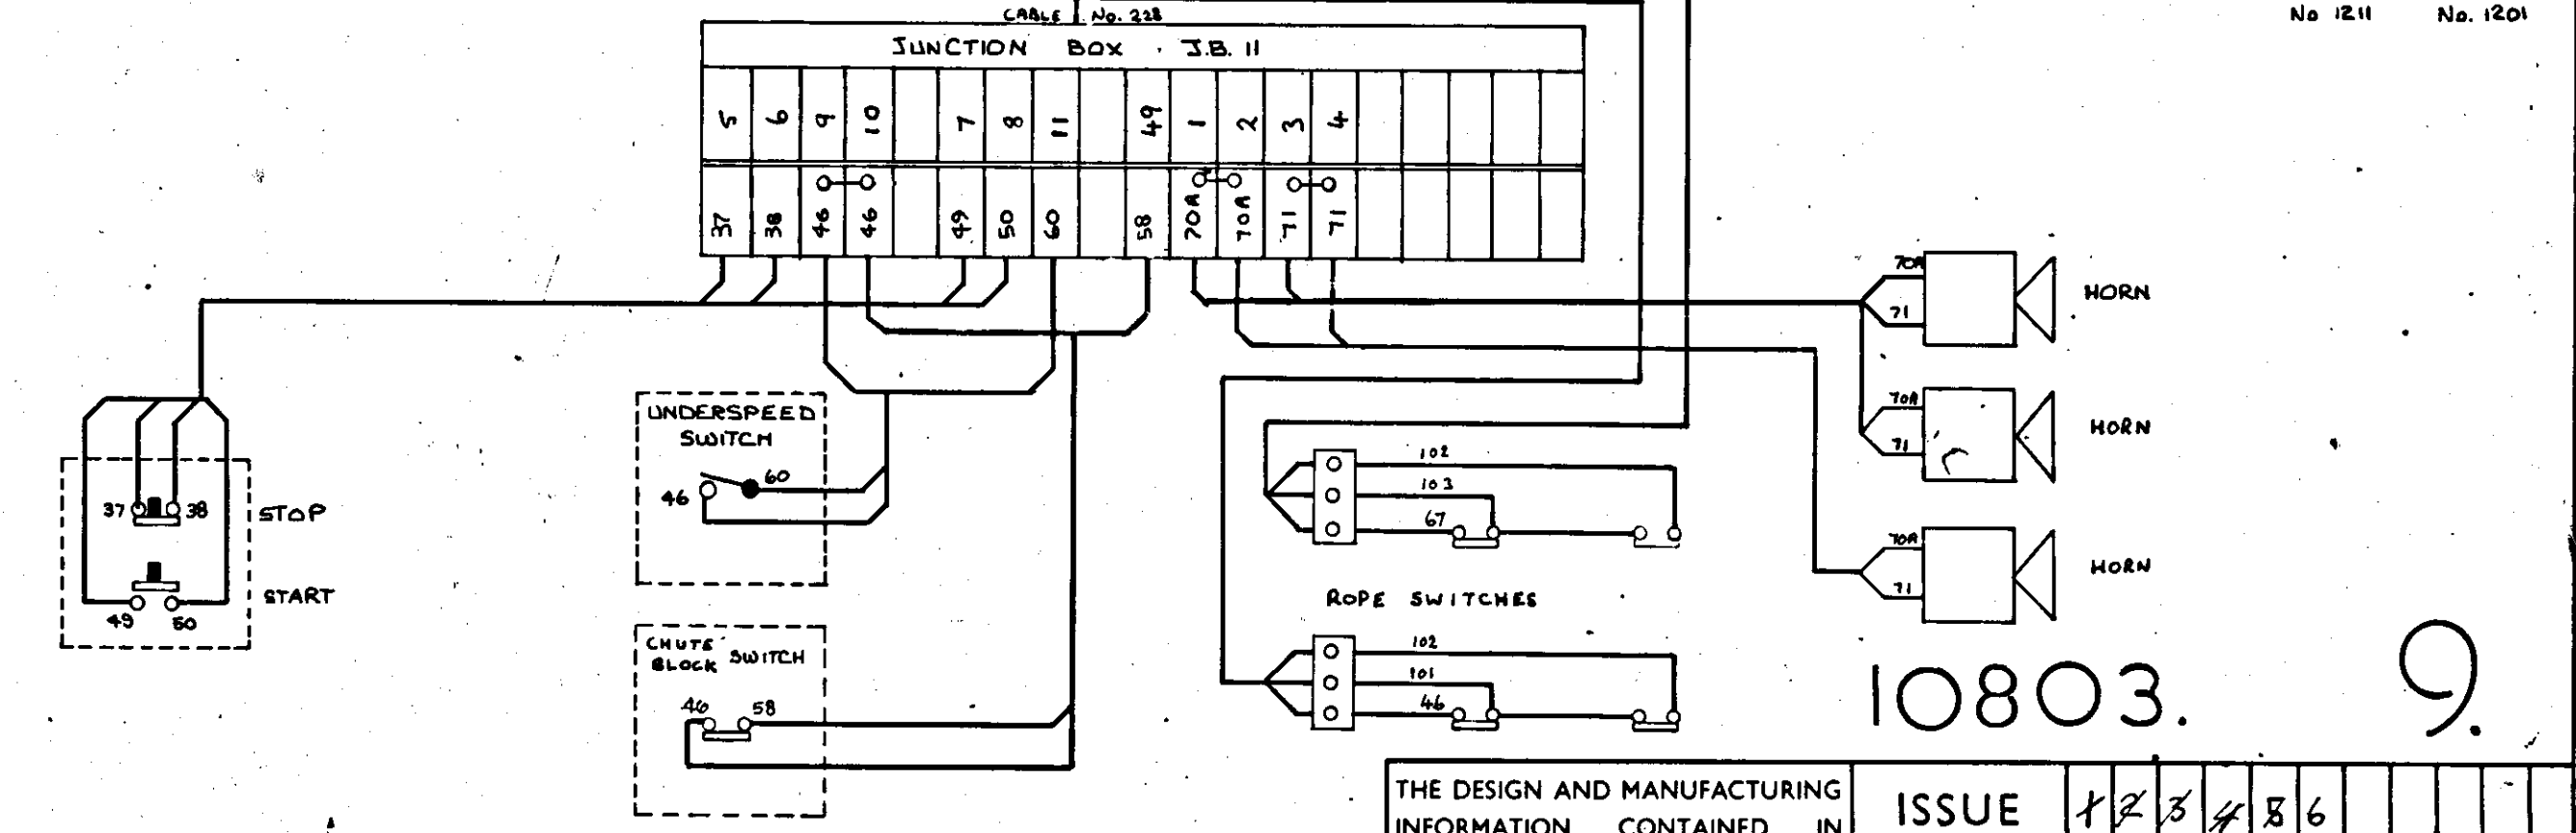
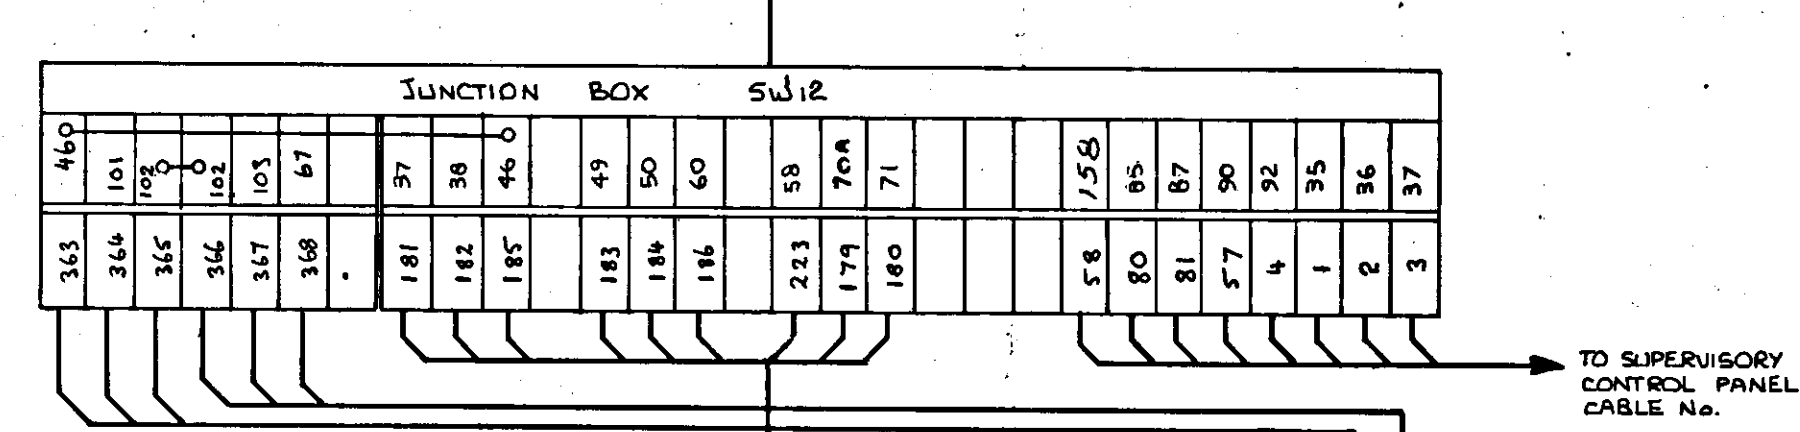
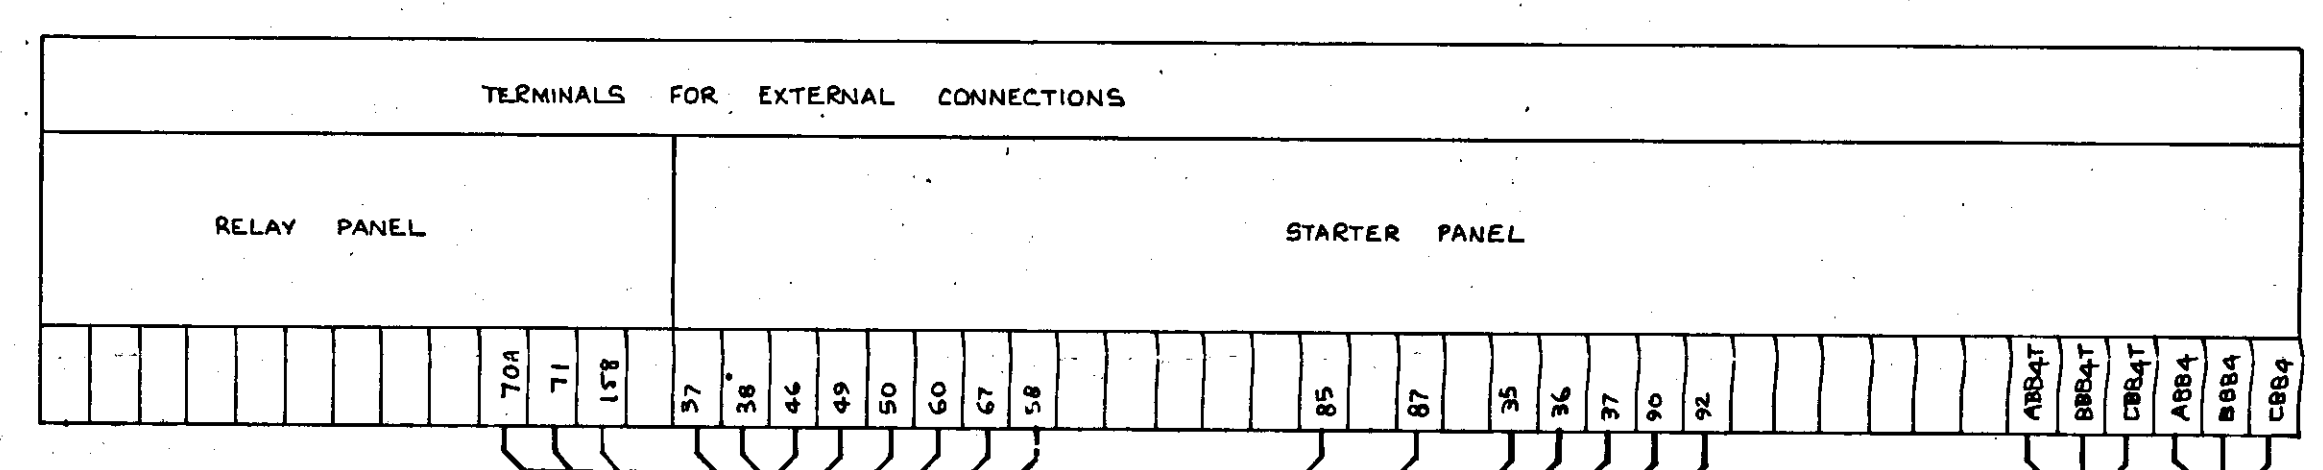
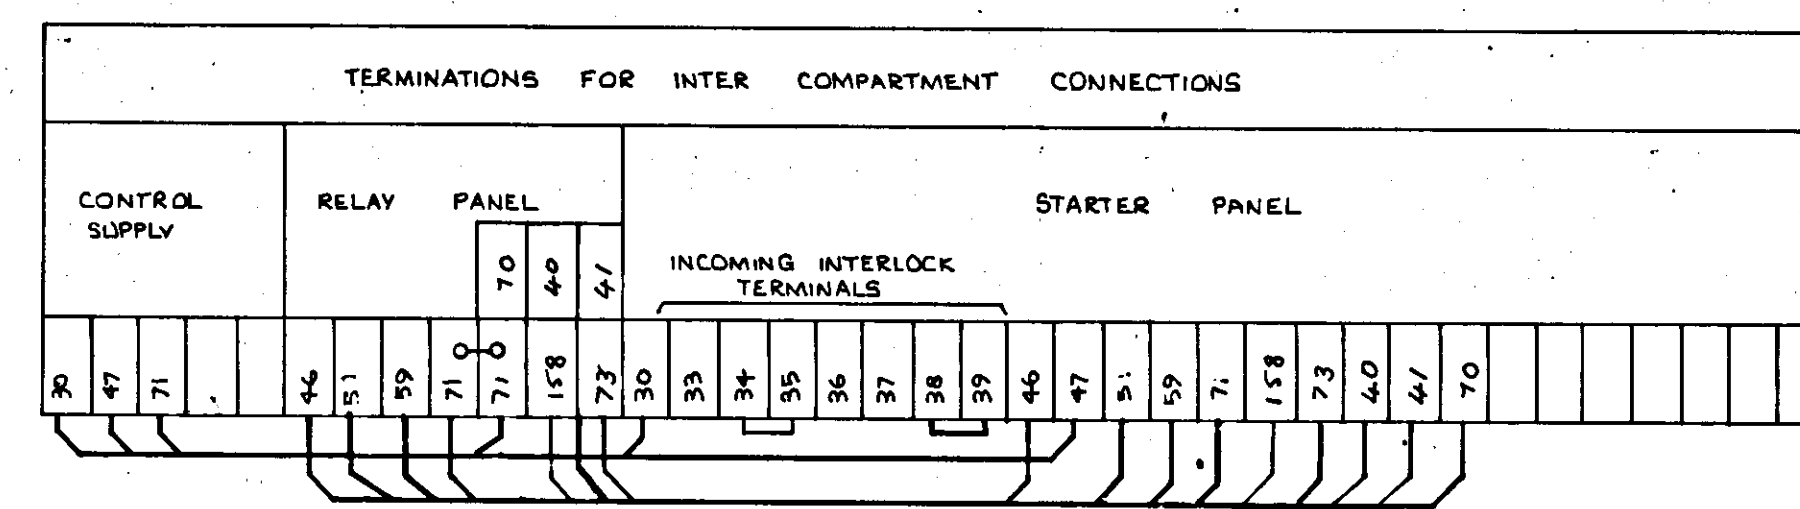
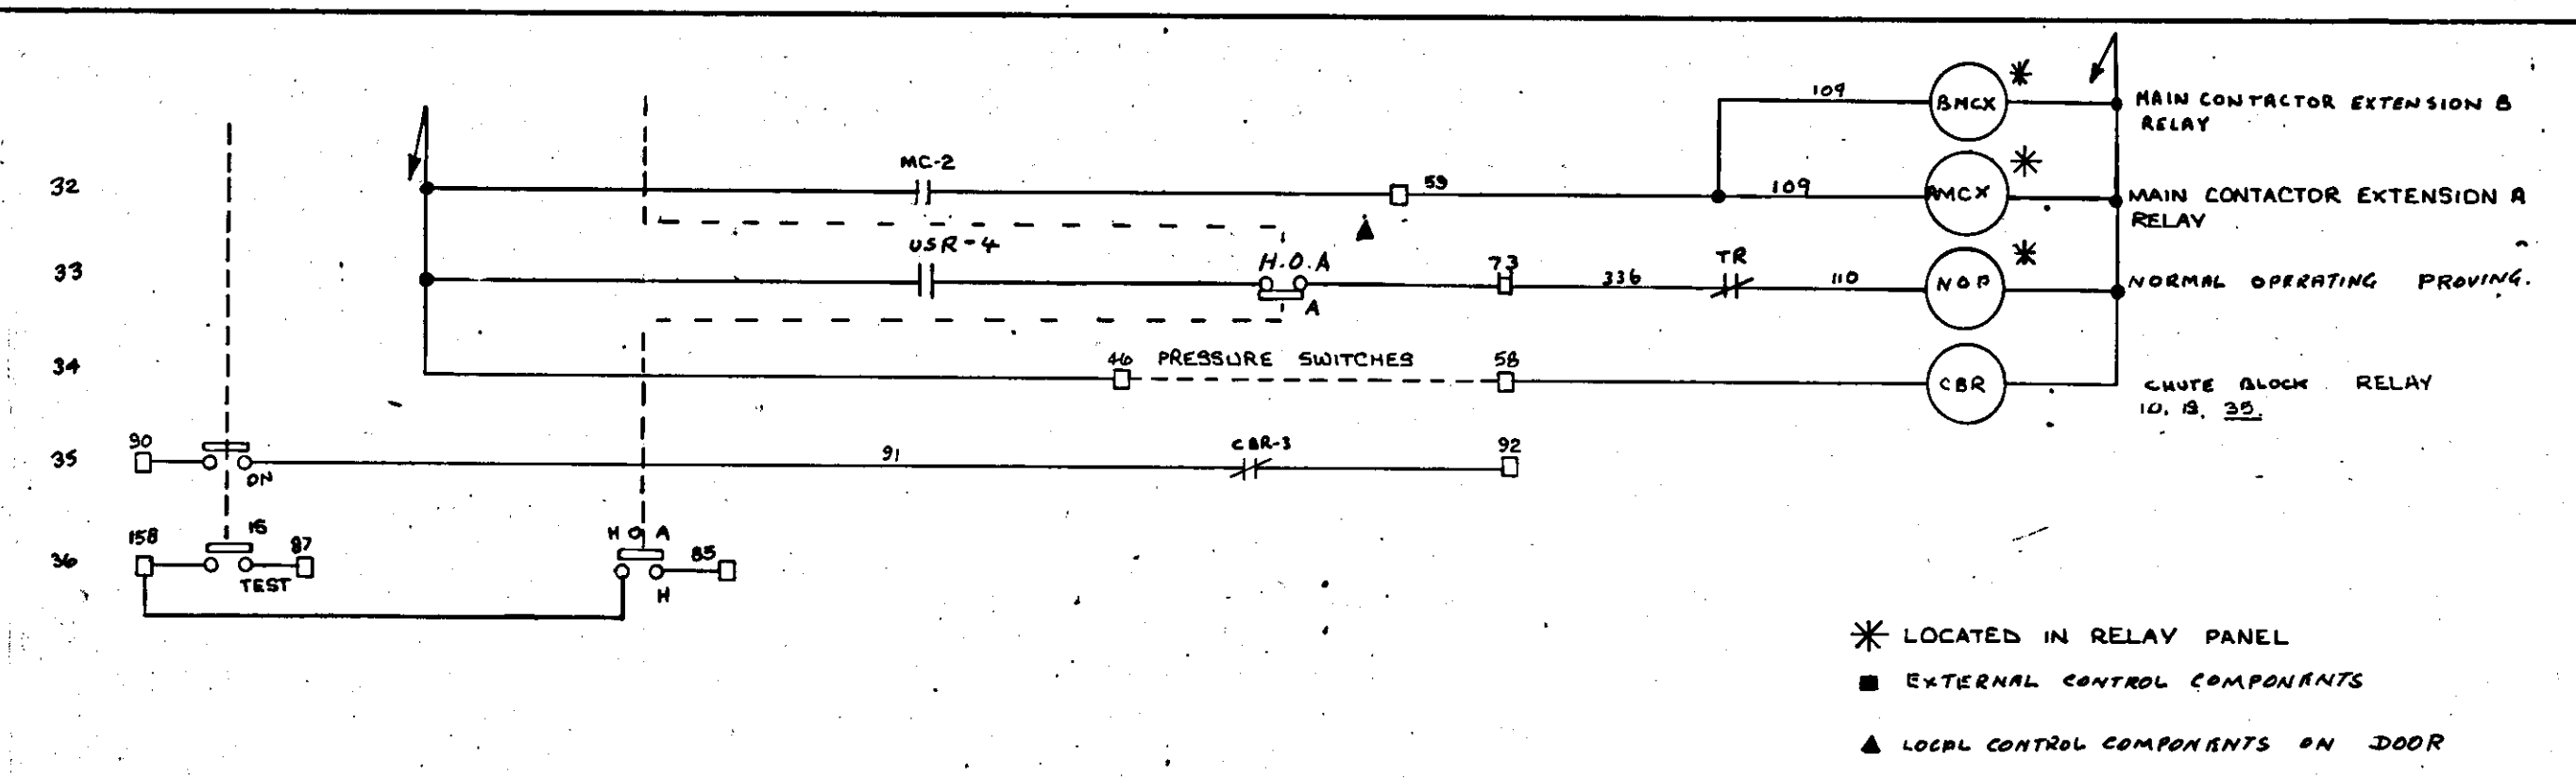
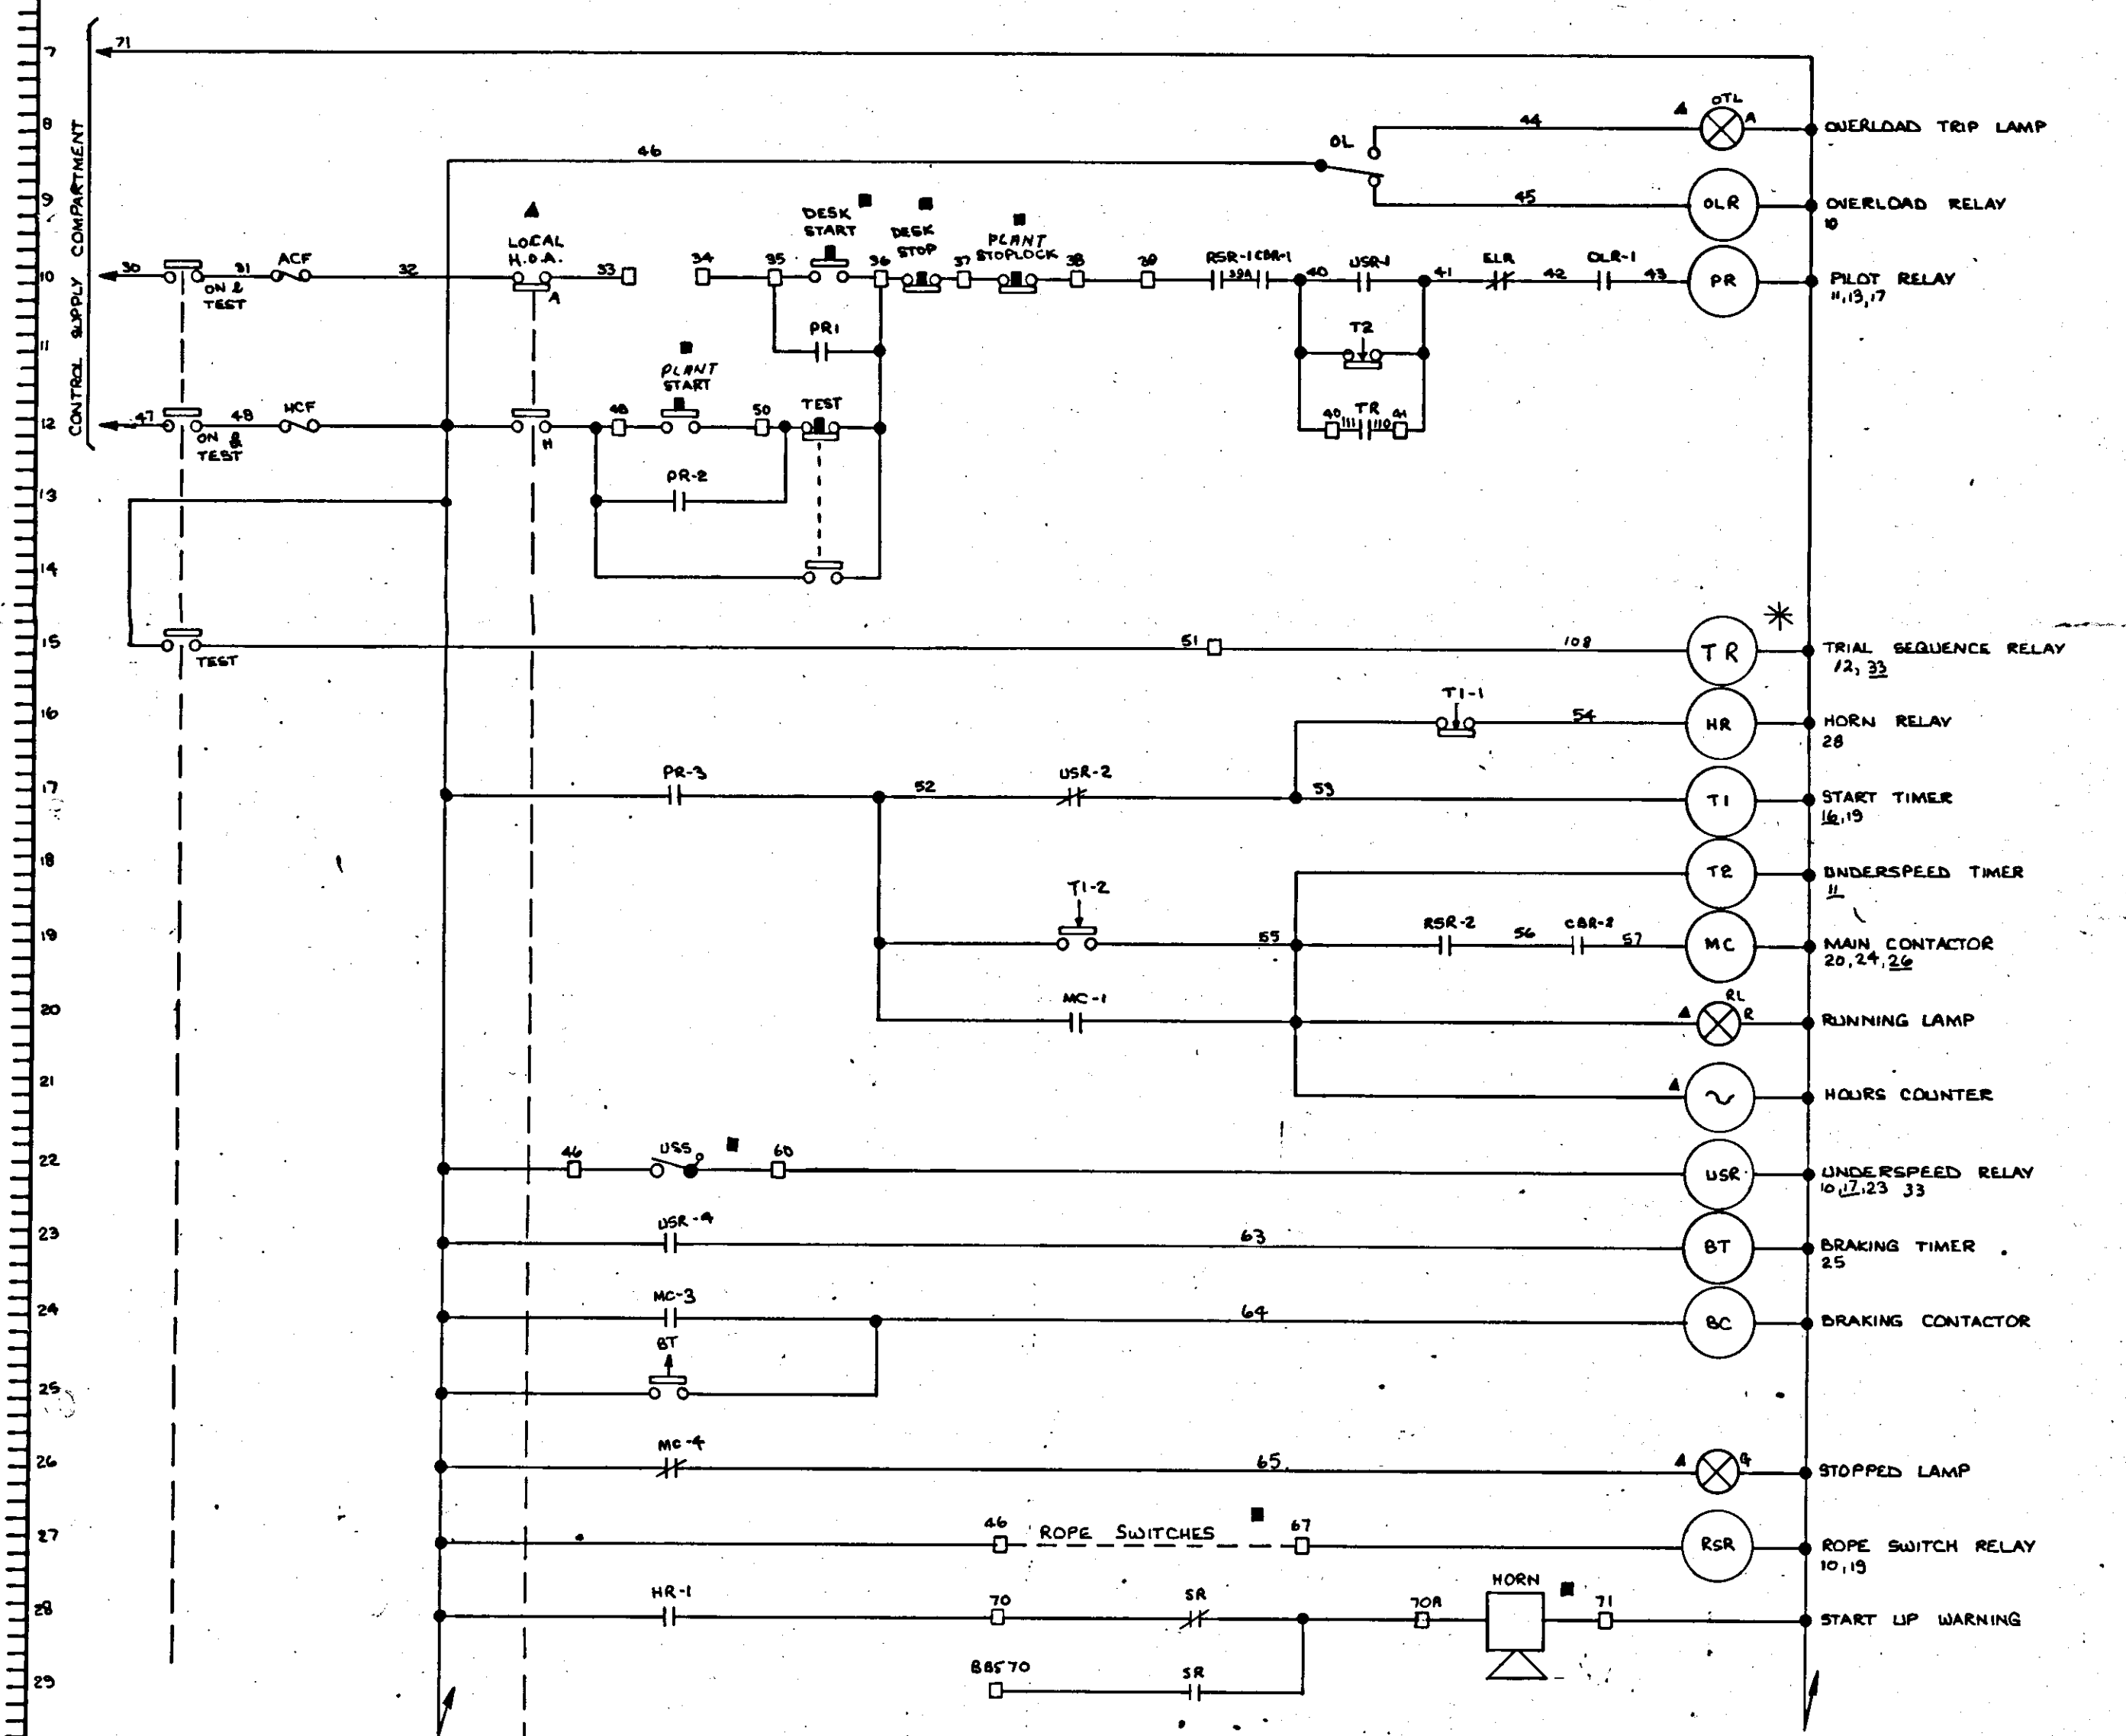


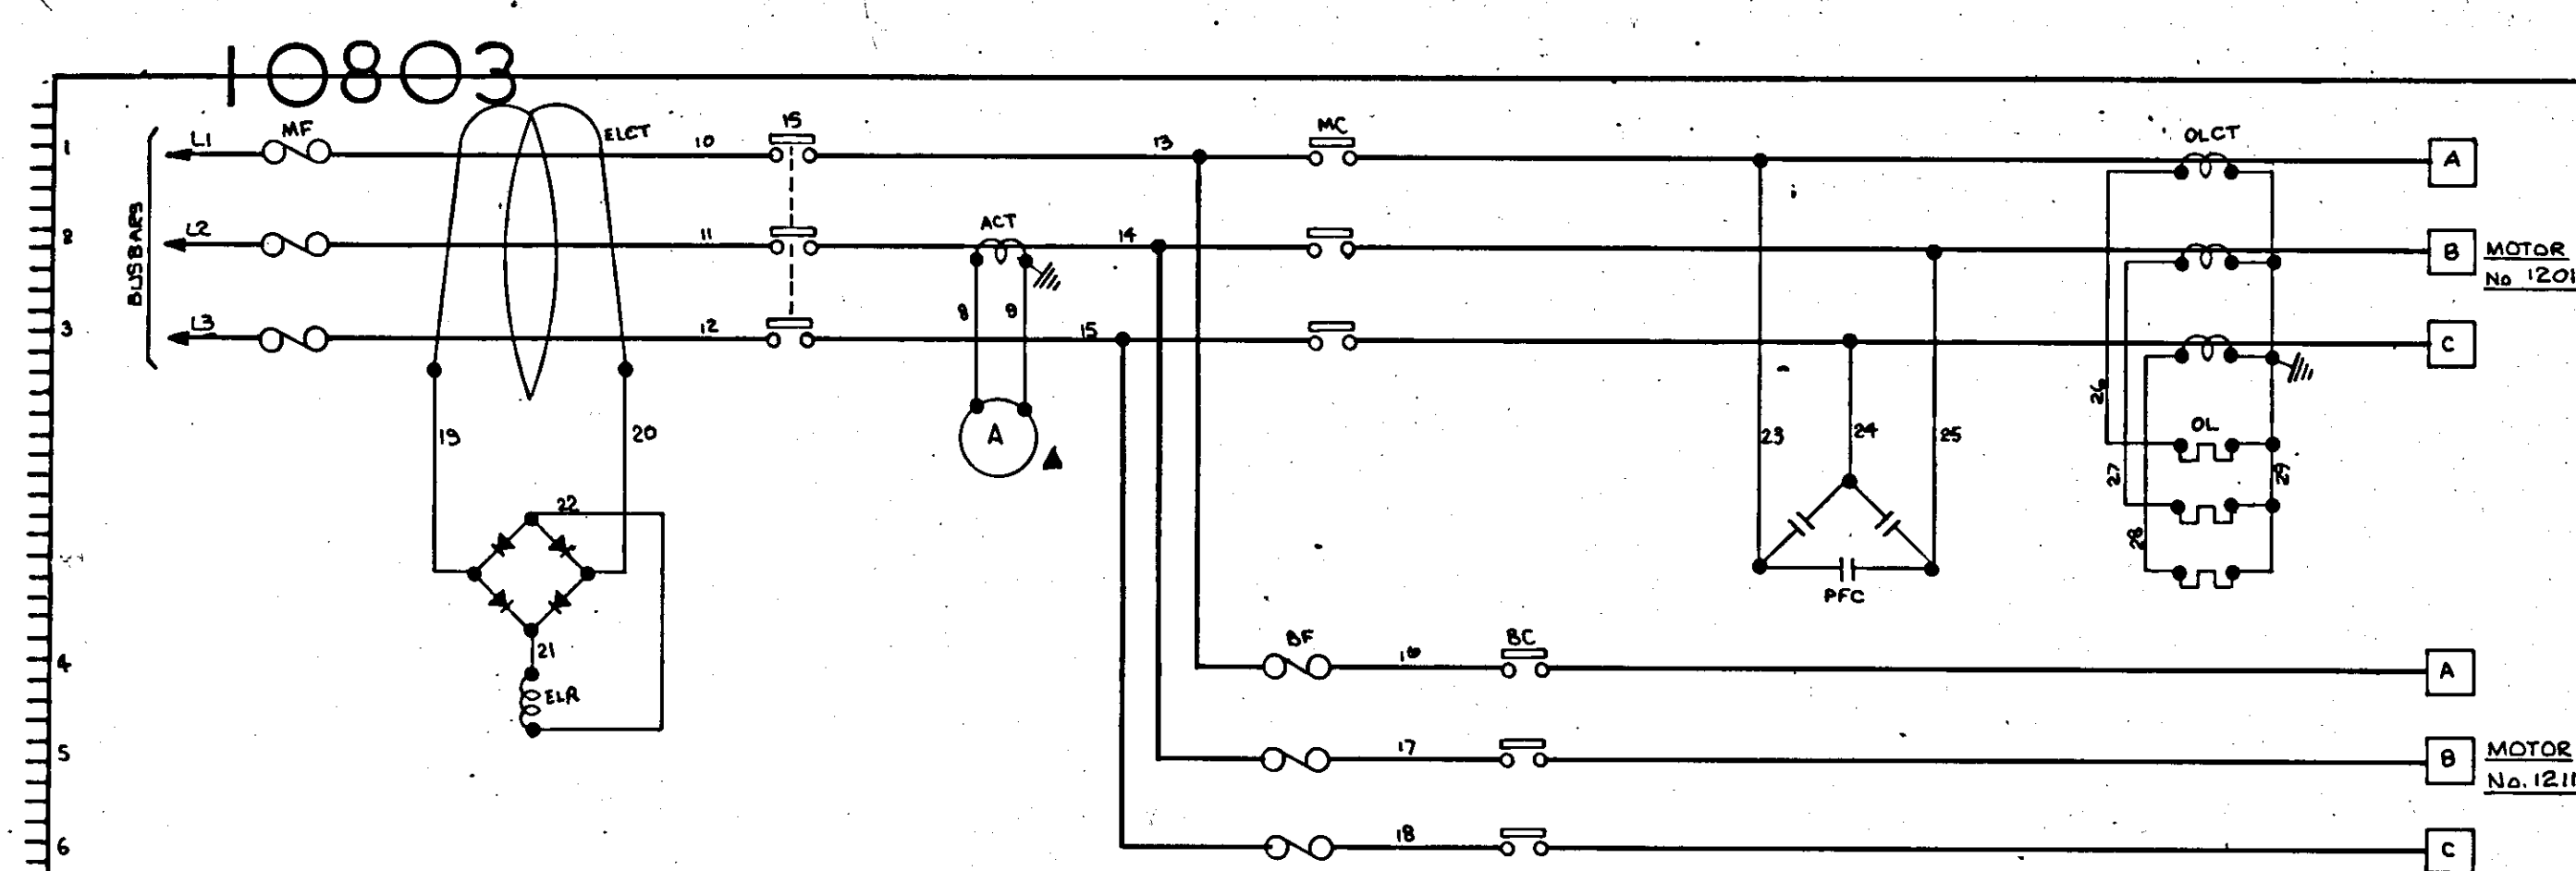

DEWHURST & PARTNER LTD. MELBOURNE WORKS HOUNSLOW		TITLE: BASEMENT BELT CONVEYOR No. 4 MCC12A		REVISION: 3 CSR MODIFICATIONS ORIGIN: 21/77 SGD.	REVISION: 2 GENERAL MODS. ORIGIN: 1/77 SGD. A.M.	REVISION: 1 TSR ADDED. REDRAWN. ORIGIN: 11/76 SGD. A.M.	REVISION: 6 SCP TERM MODIFICATION NO. 5 TURNS IN 54 NO. 5 TURNS IN 54 ORIGIN: 10/77 SGD. A.M.	REVISION: 5 TERNING TO SCP ADDER, ANCE NAME IN MOD. MODS. ORIGIN: 28/4/77	REVISION: 4 GEN. MODS. ORIGIN: 10/77 A.L.J.B.	THE DESIGN AND MANUFACTURING INFORMATION CONTAINED IN THIS DRAWING IS THE EXCLUSIVE RIGHT OF DEWHURST & PARTNER LTD. AND MUST NOT BE COPIED OR USED FOR MANUFACTURING PURPOSES.	ISSUE 123456 CTX36IBN CTX36IBN
				DRAWN BY: A.M. DATE: 24.11.76 CHECKED BY: [Signature] APPROVED BY: [Signature] DATE: 29.11.76	KEY DIAG. No. EXT. DIAG. No. REL. DIAG. No. PANEL LAYOUT No.						