
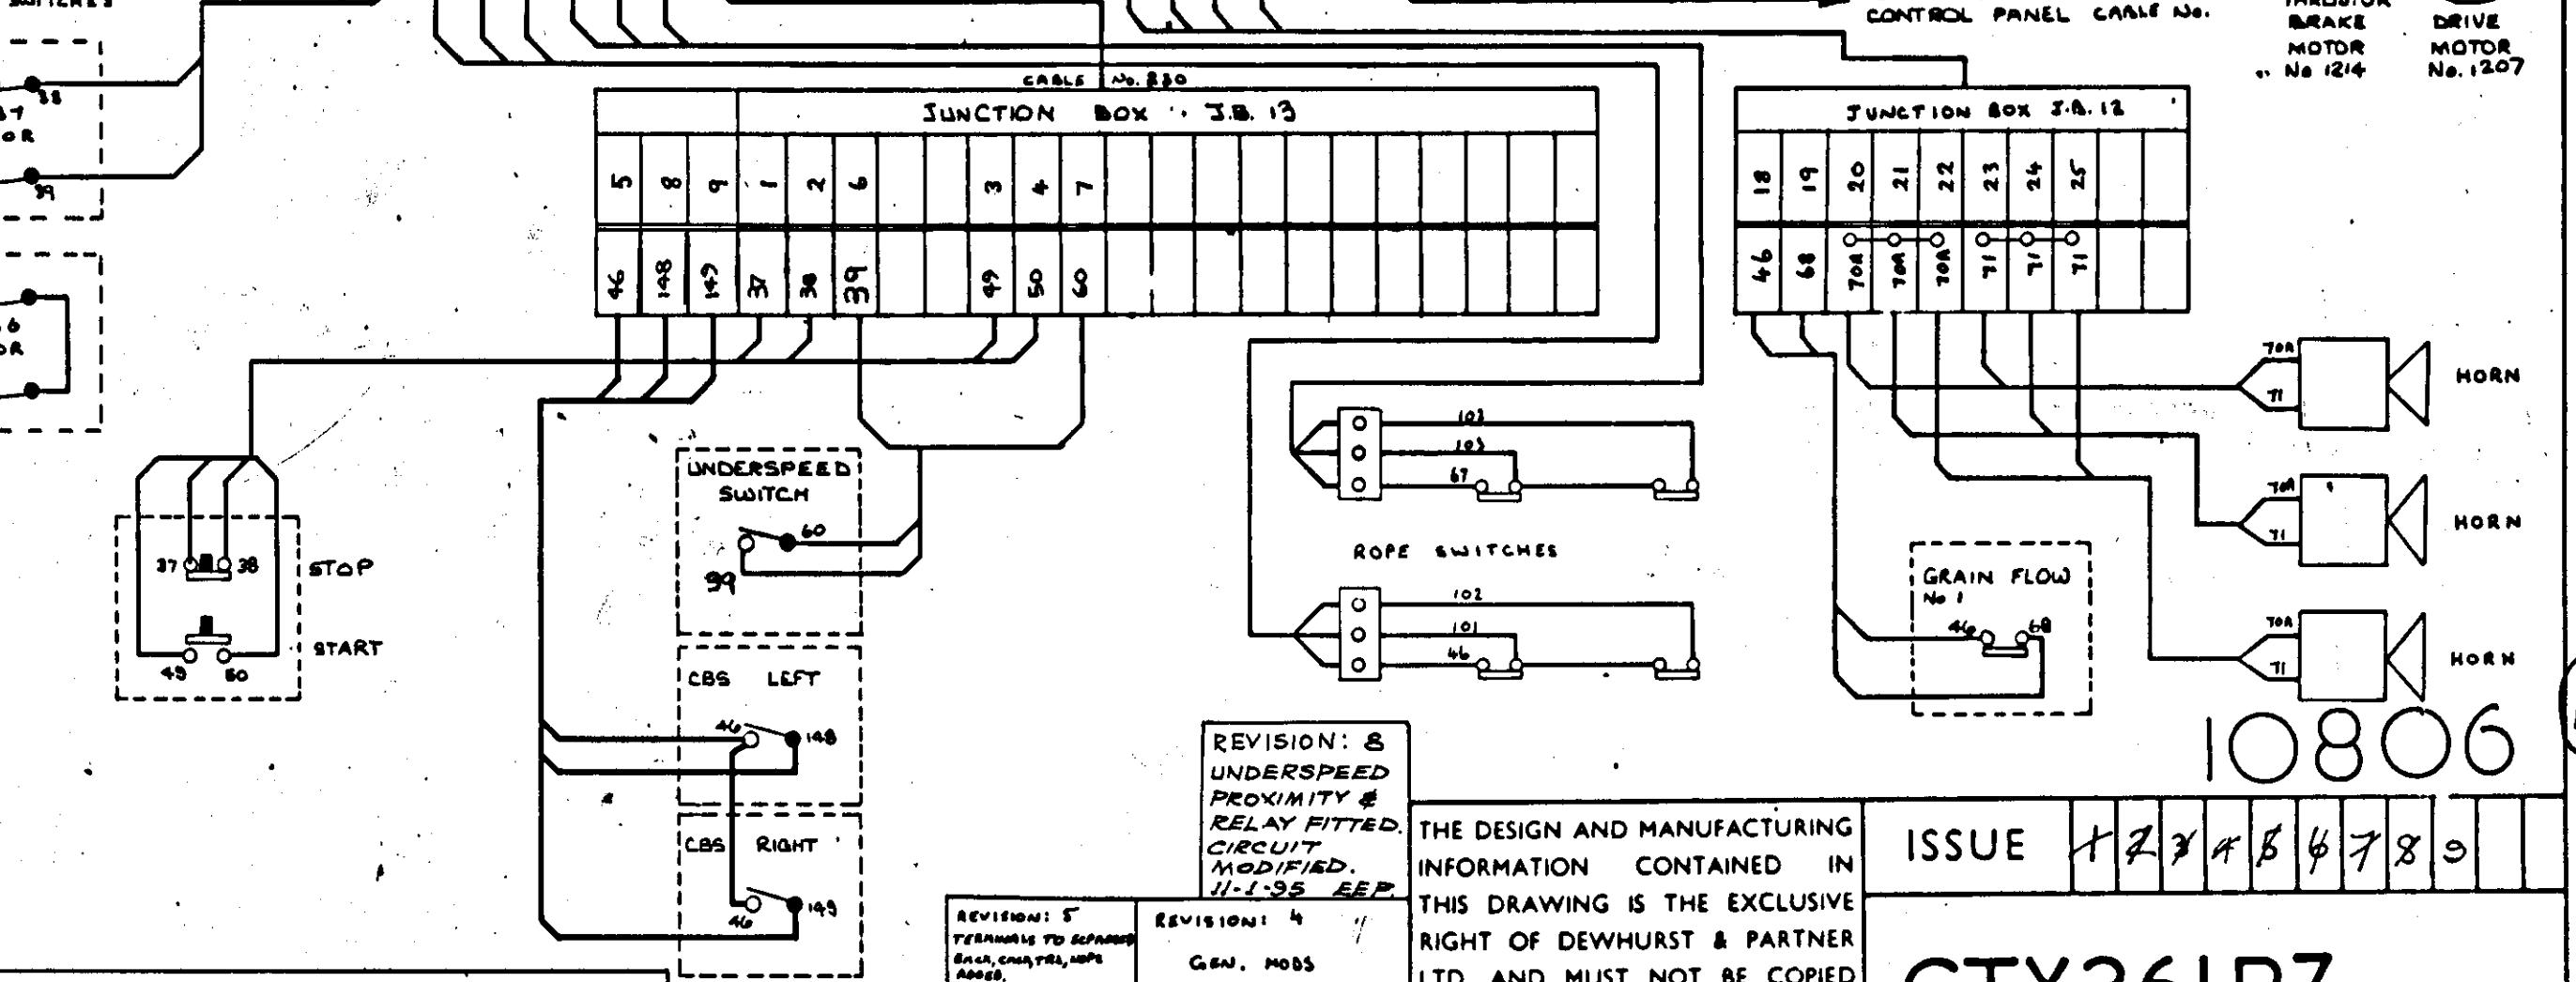
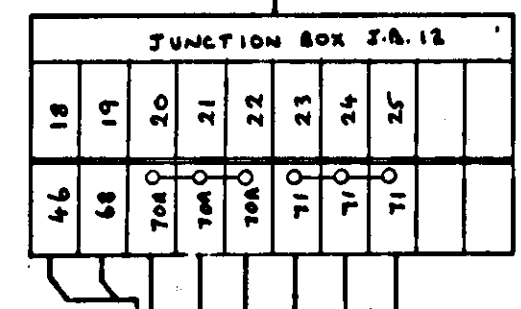
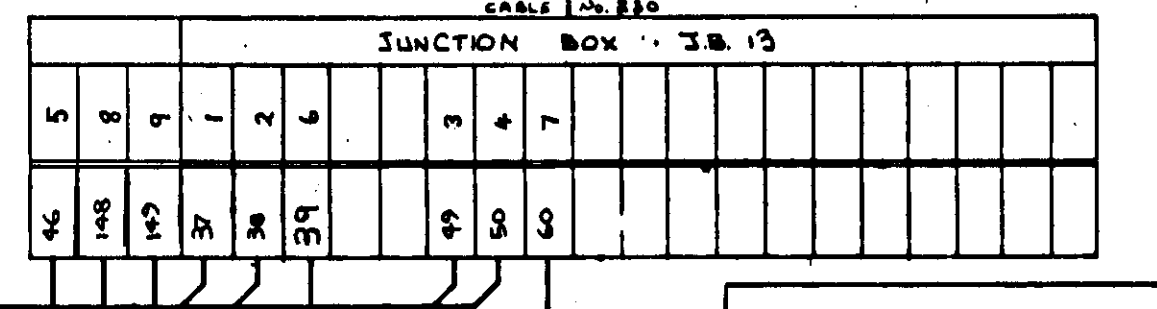
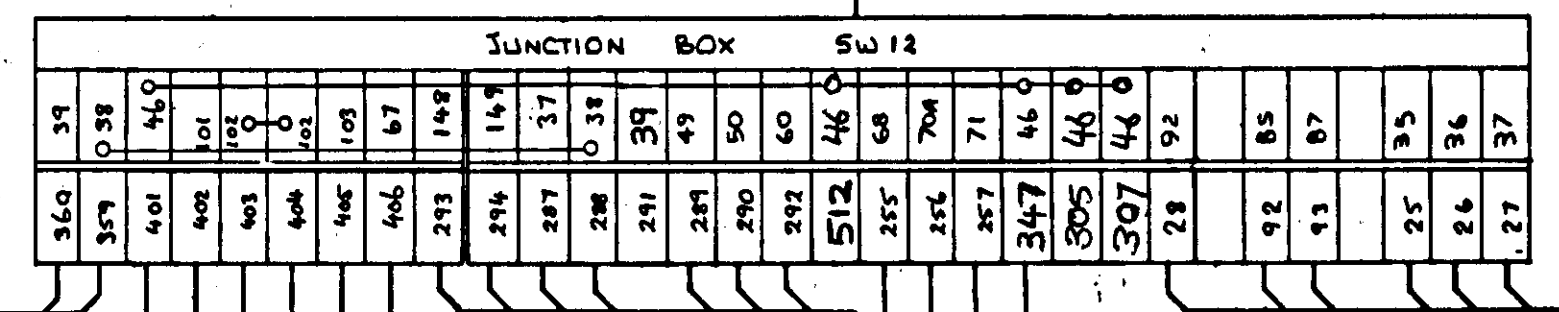
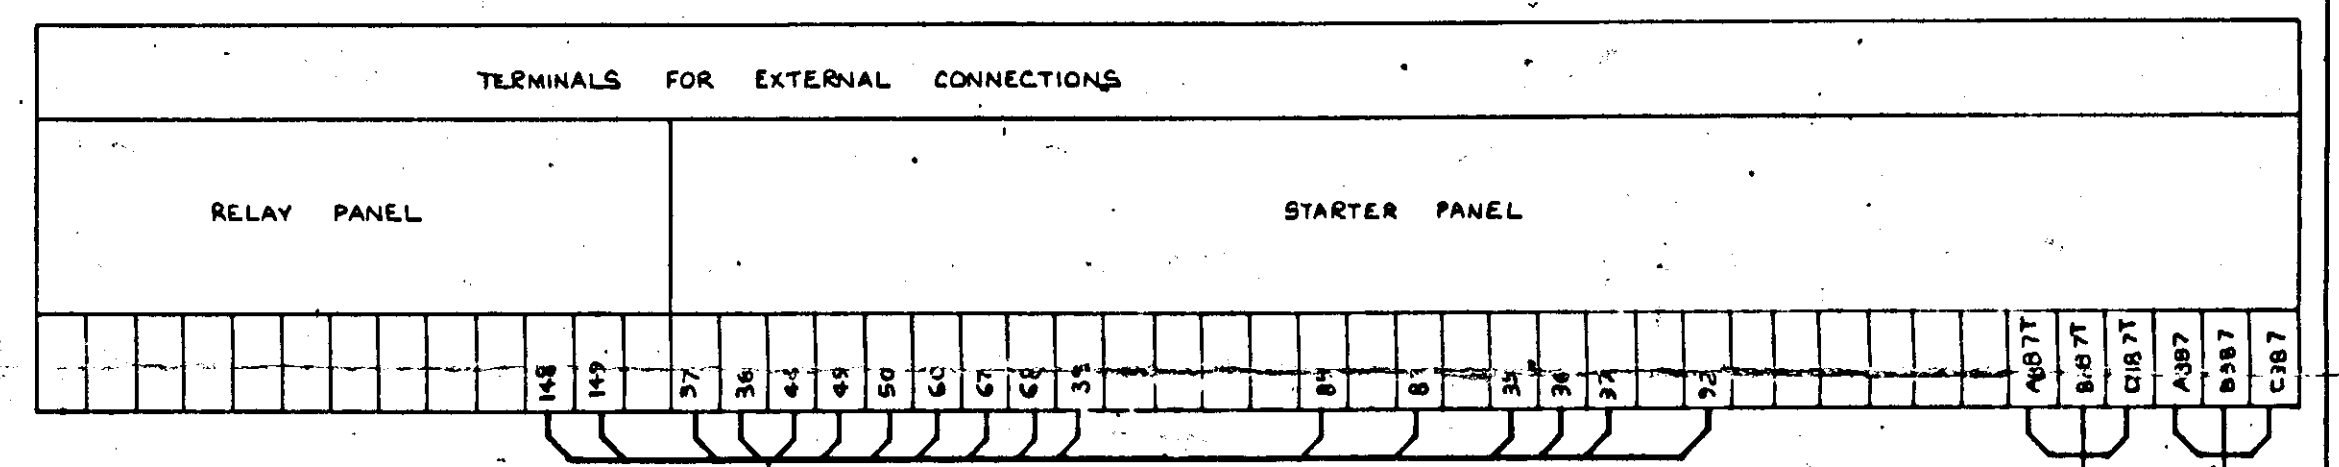
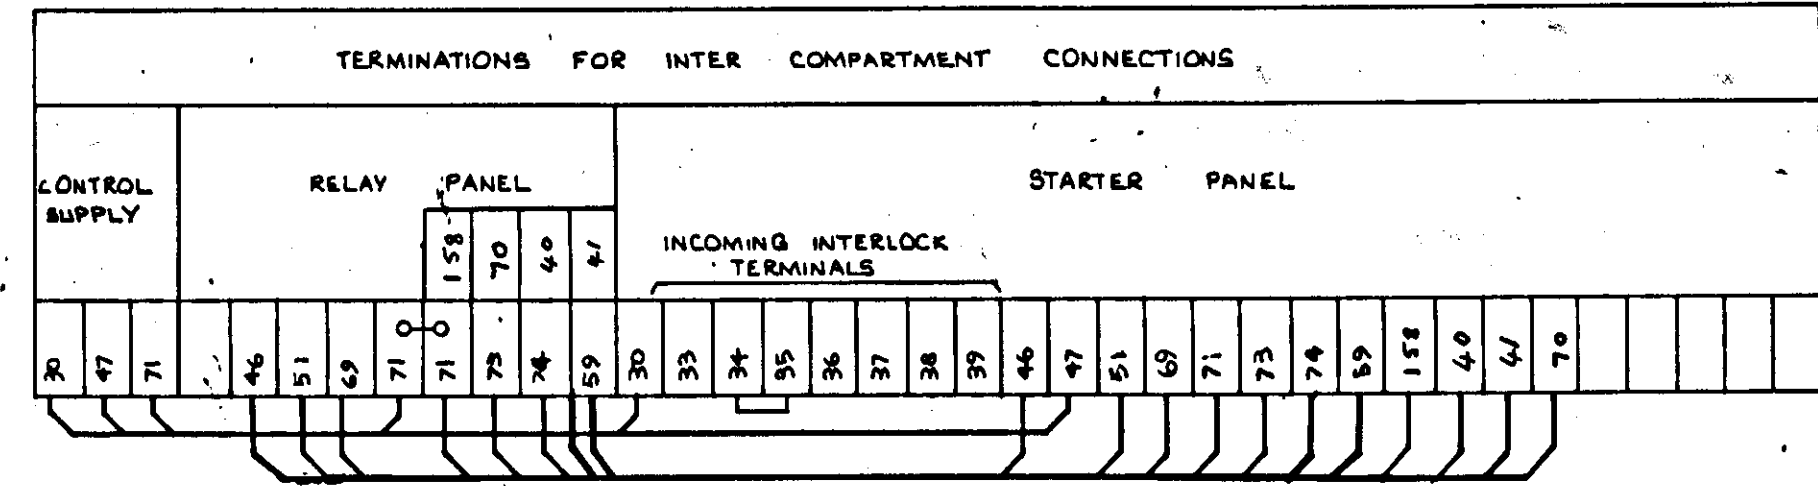
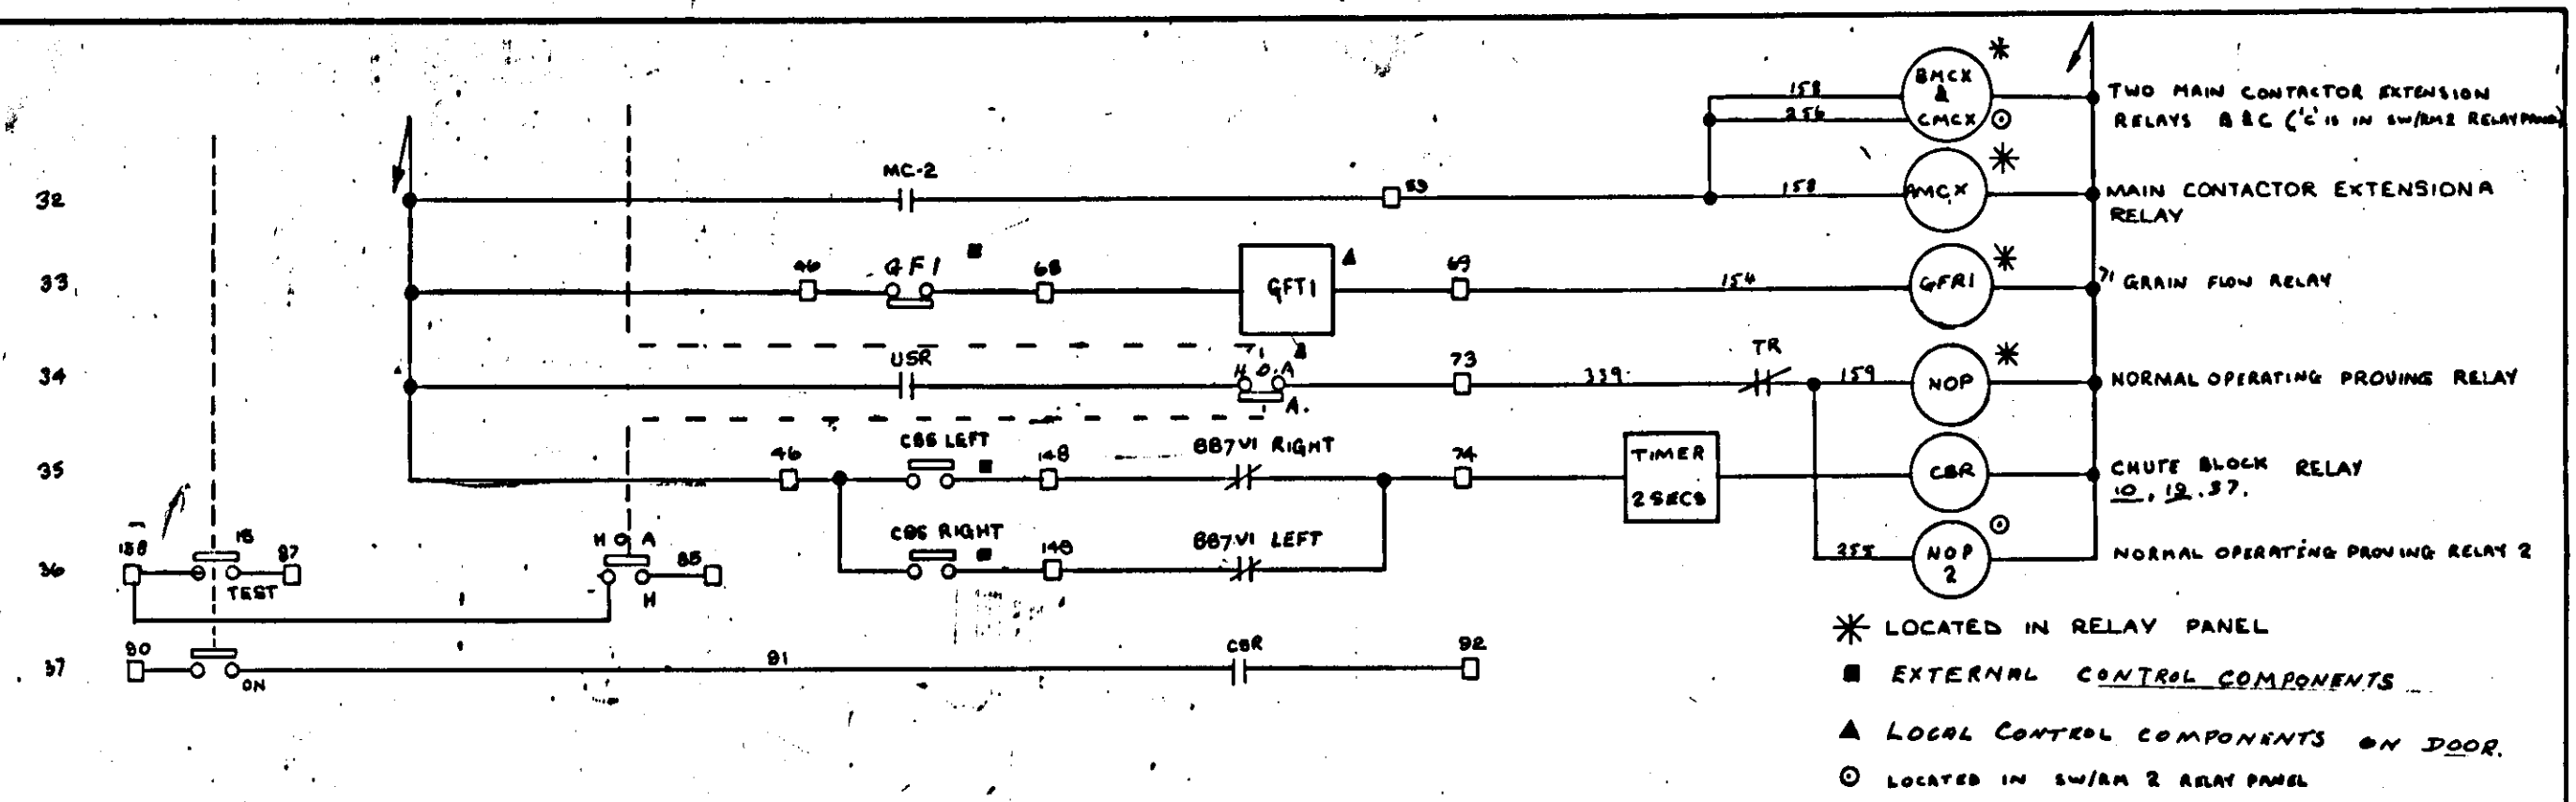
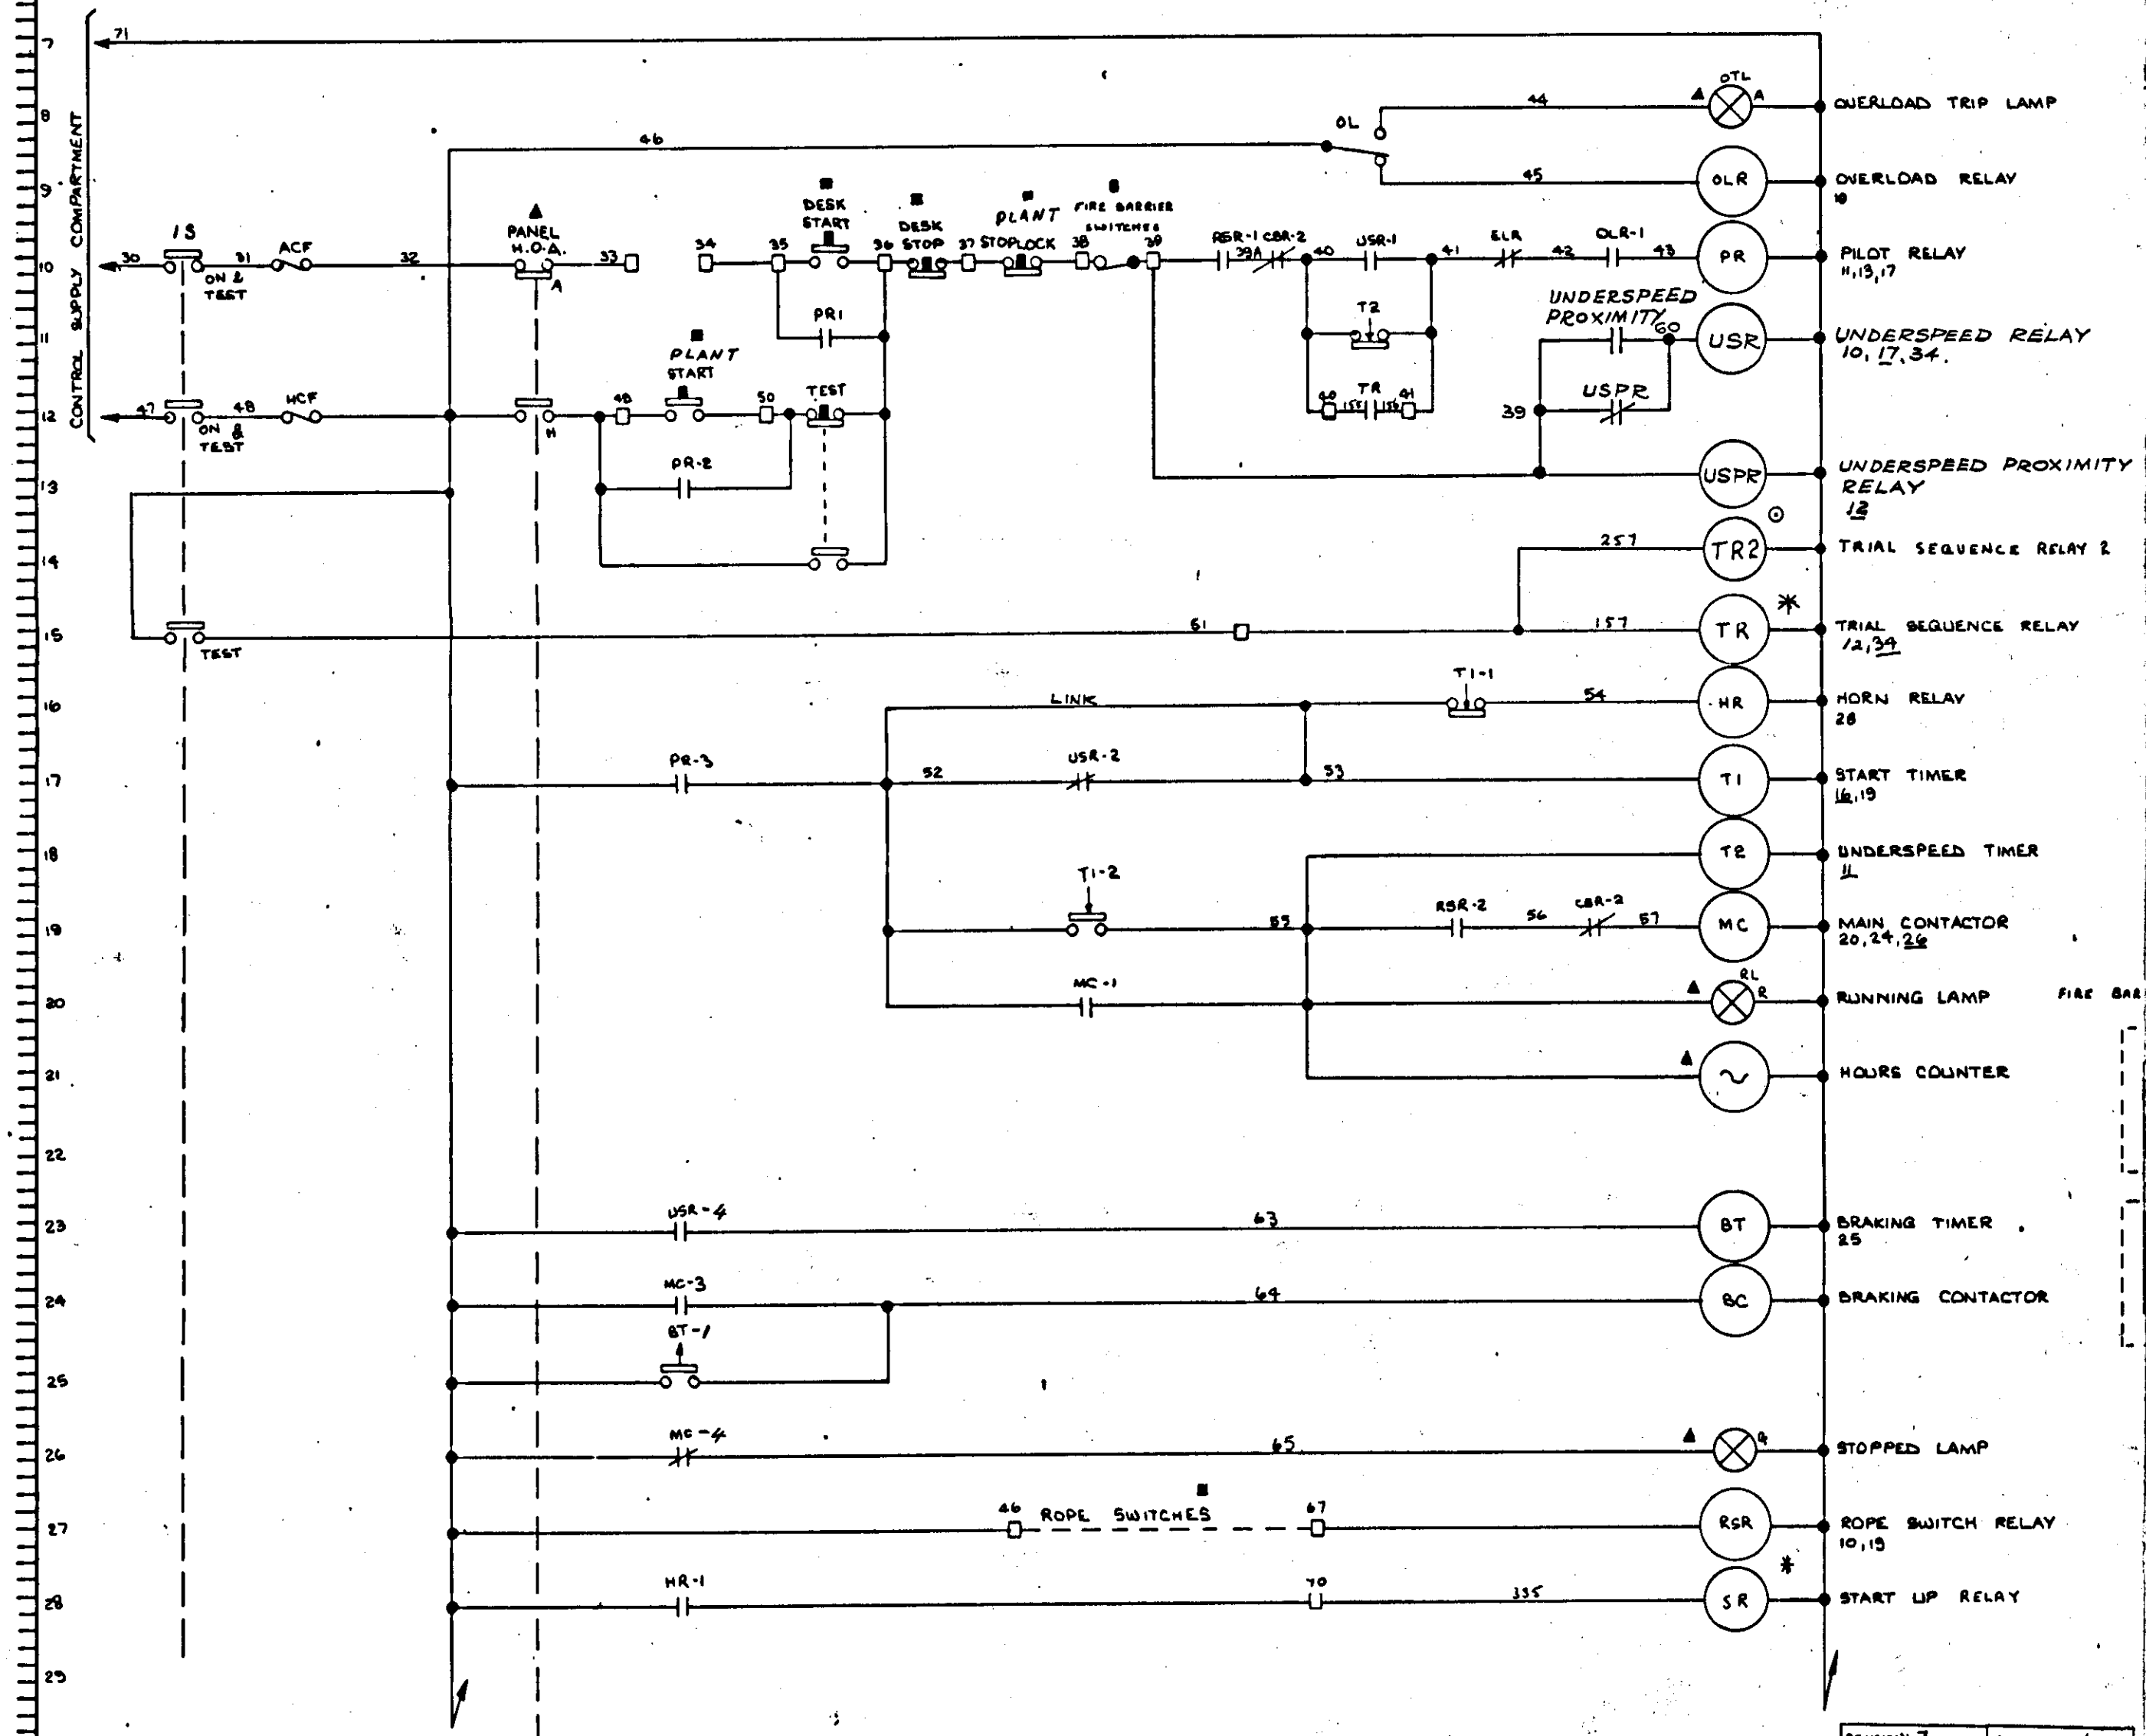


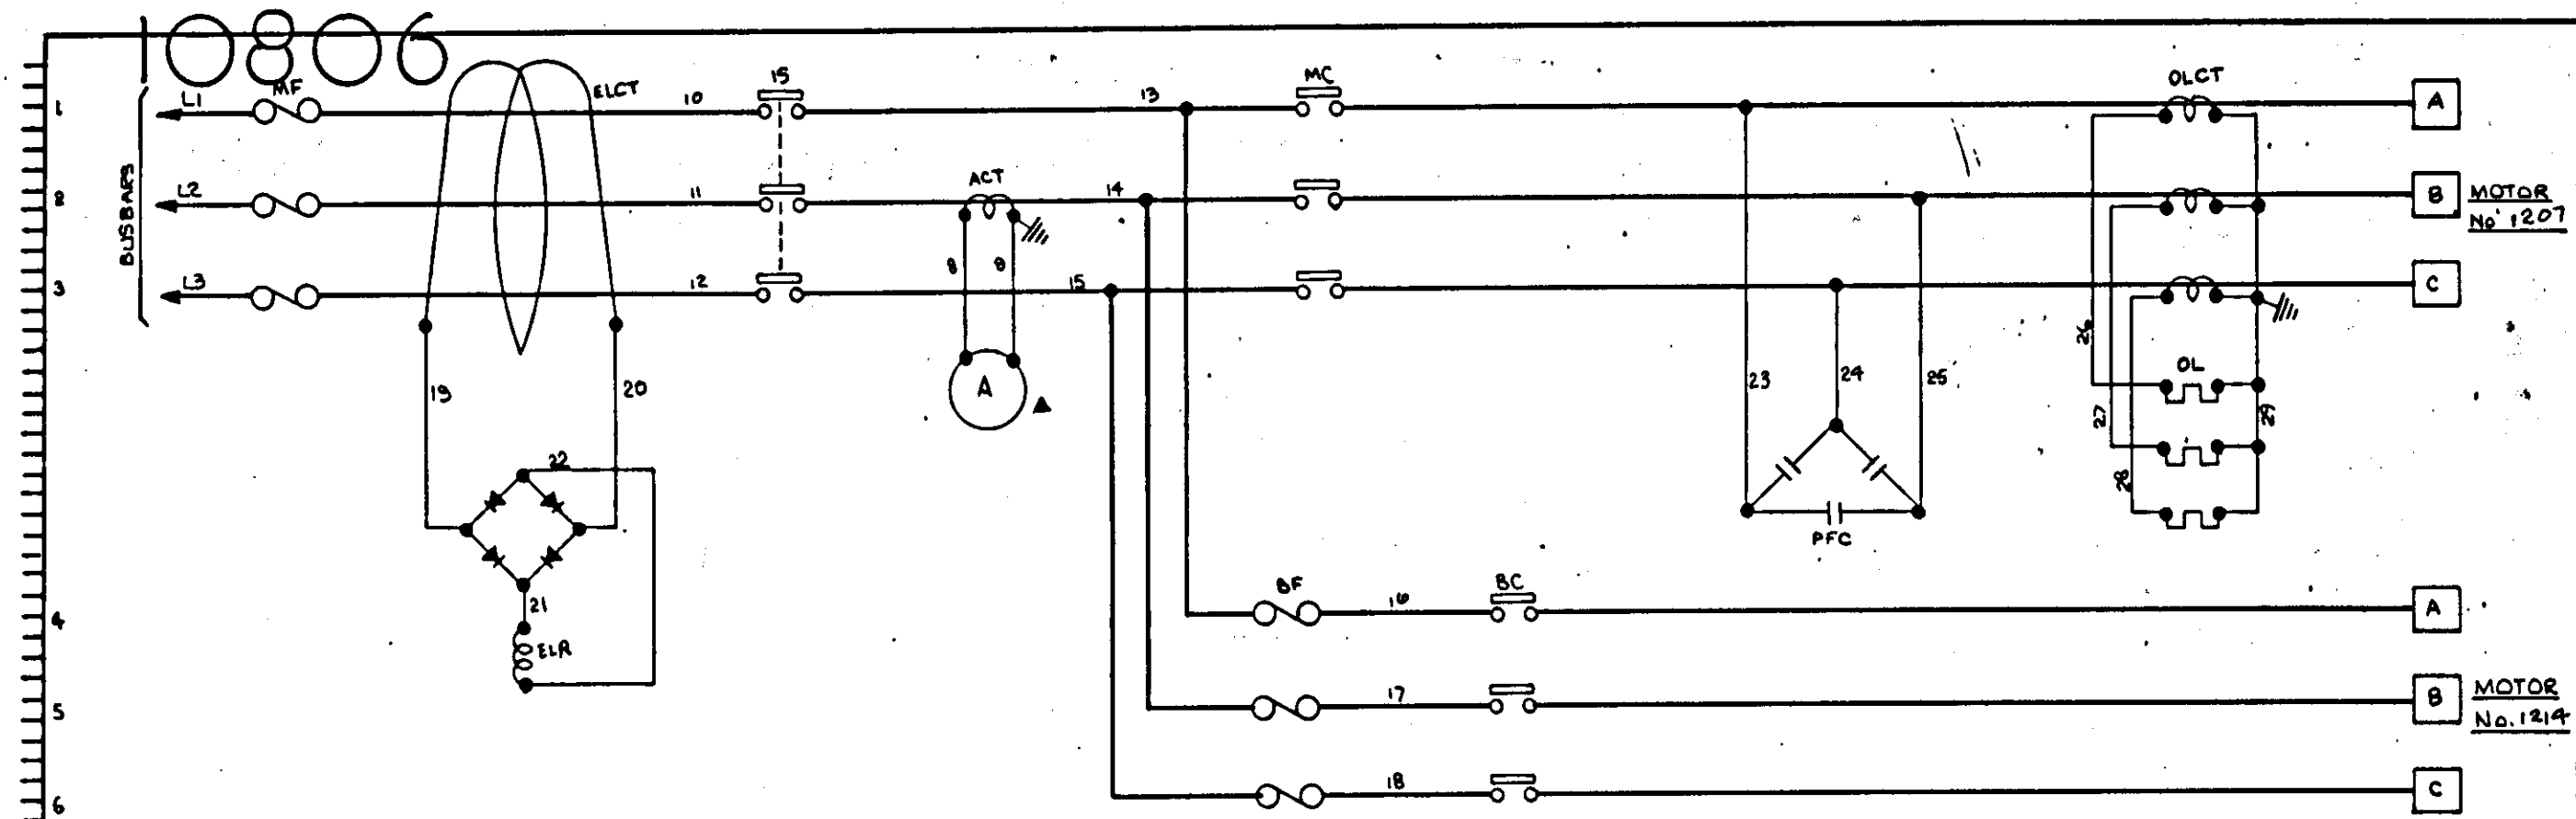

DEWHURST & PARTNER LTD.
MELBOURNE WORKS HOUNSLOW

TITLE: BASEMENT BELT CONVEYOR No. 7
MCC:12A

REVISION: 3. CSR MODIFICATIONS. DATE: 2/2/77 SGD. A.M.
REVISION: 2. GENERAL MODS. DATE: 1/1/77 SGD. A.M.
REVISION: 1. TSR ADDED REDRAWN. DATE: 11/1/76 SGD. A.M.

DRAWN BY: A.M. DATE: 24.11.76
CHECKED BY: [Signature] DATE: 29.11.76
APPROVED BY: [Signature]

KEY DIAG. No. EXT. DIAG. No. REL. DIAG. No. PANEL LAYOUT No.

ISSUE 1 2 3 4 5 6 7 8 9
CTX361BZ
CTX361BZ