


10802

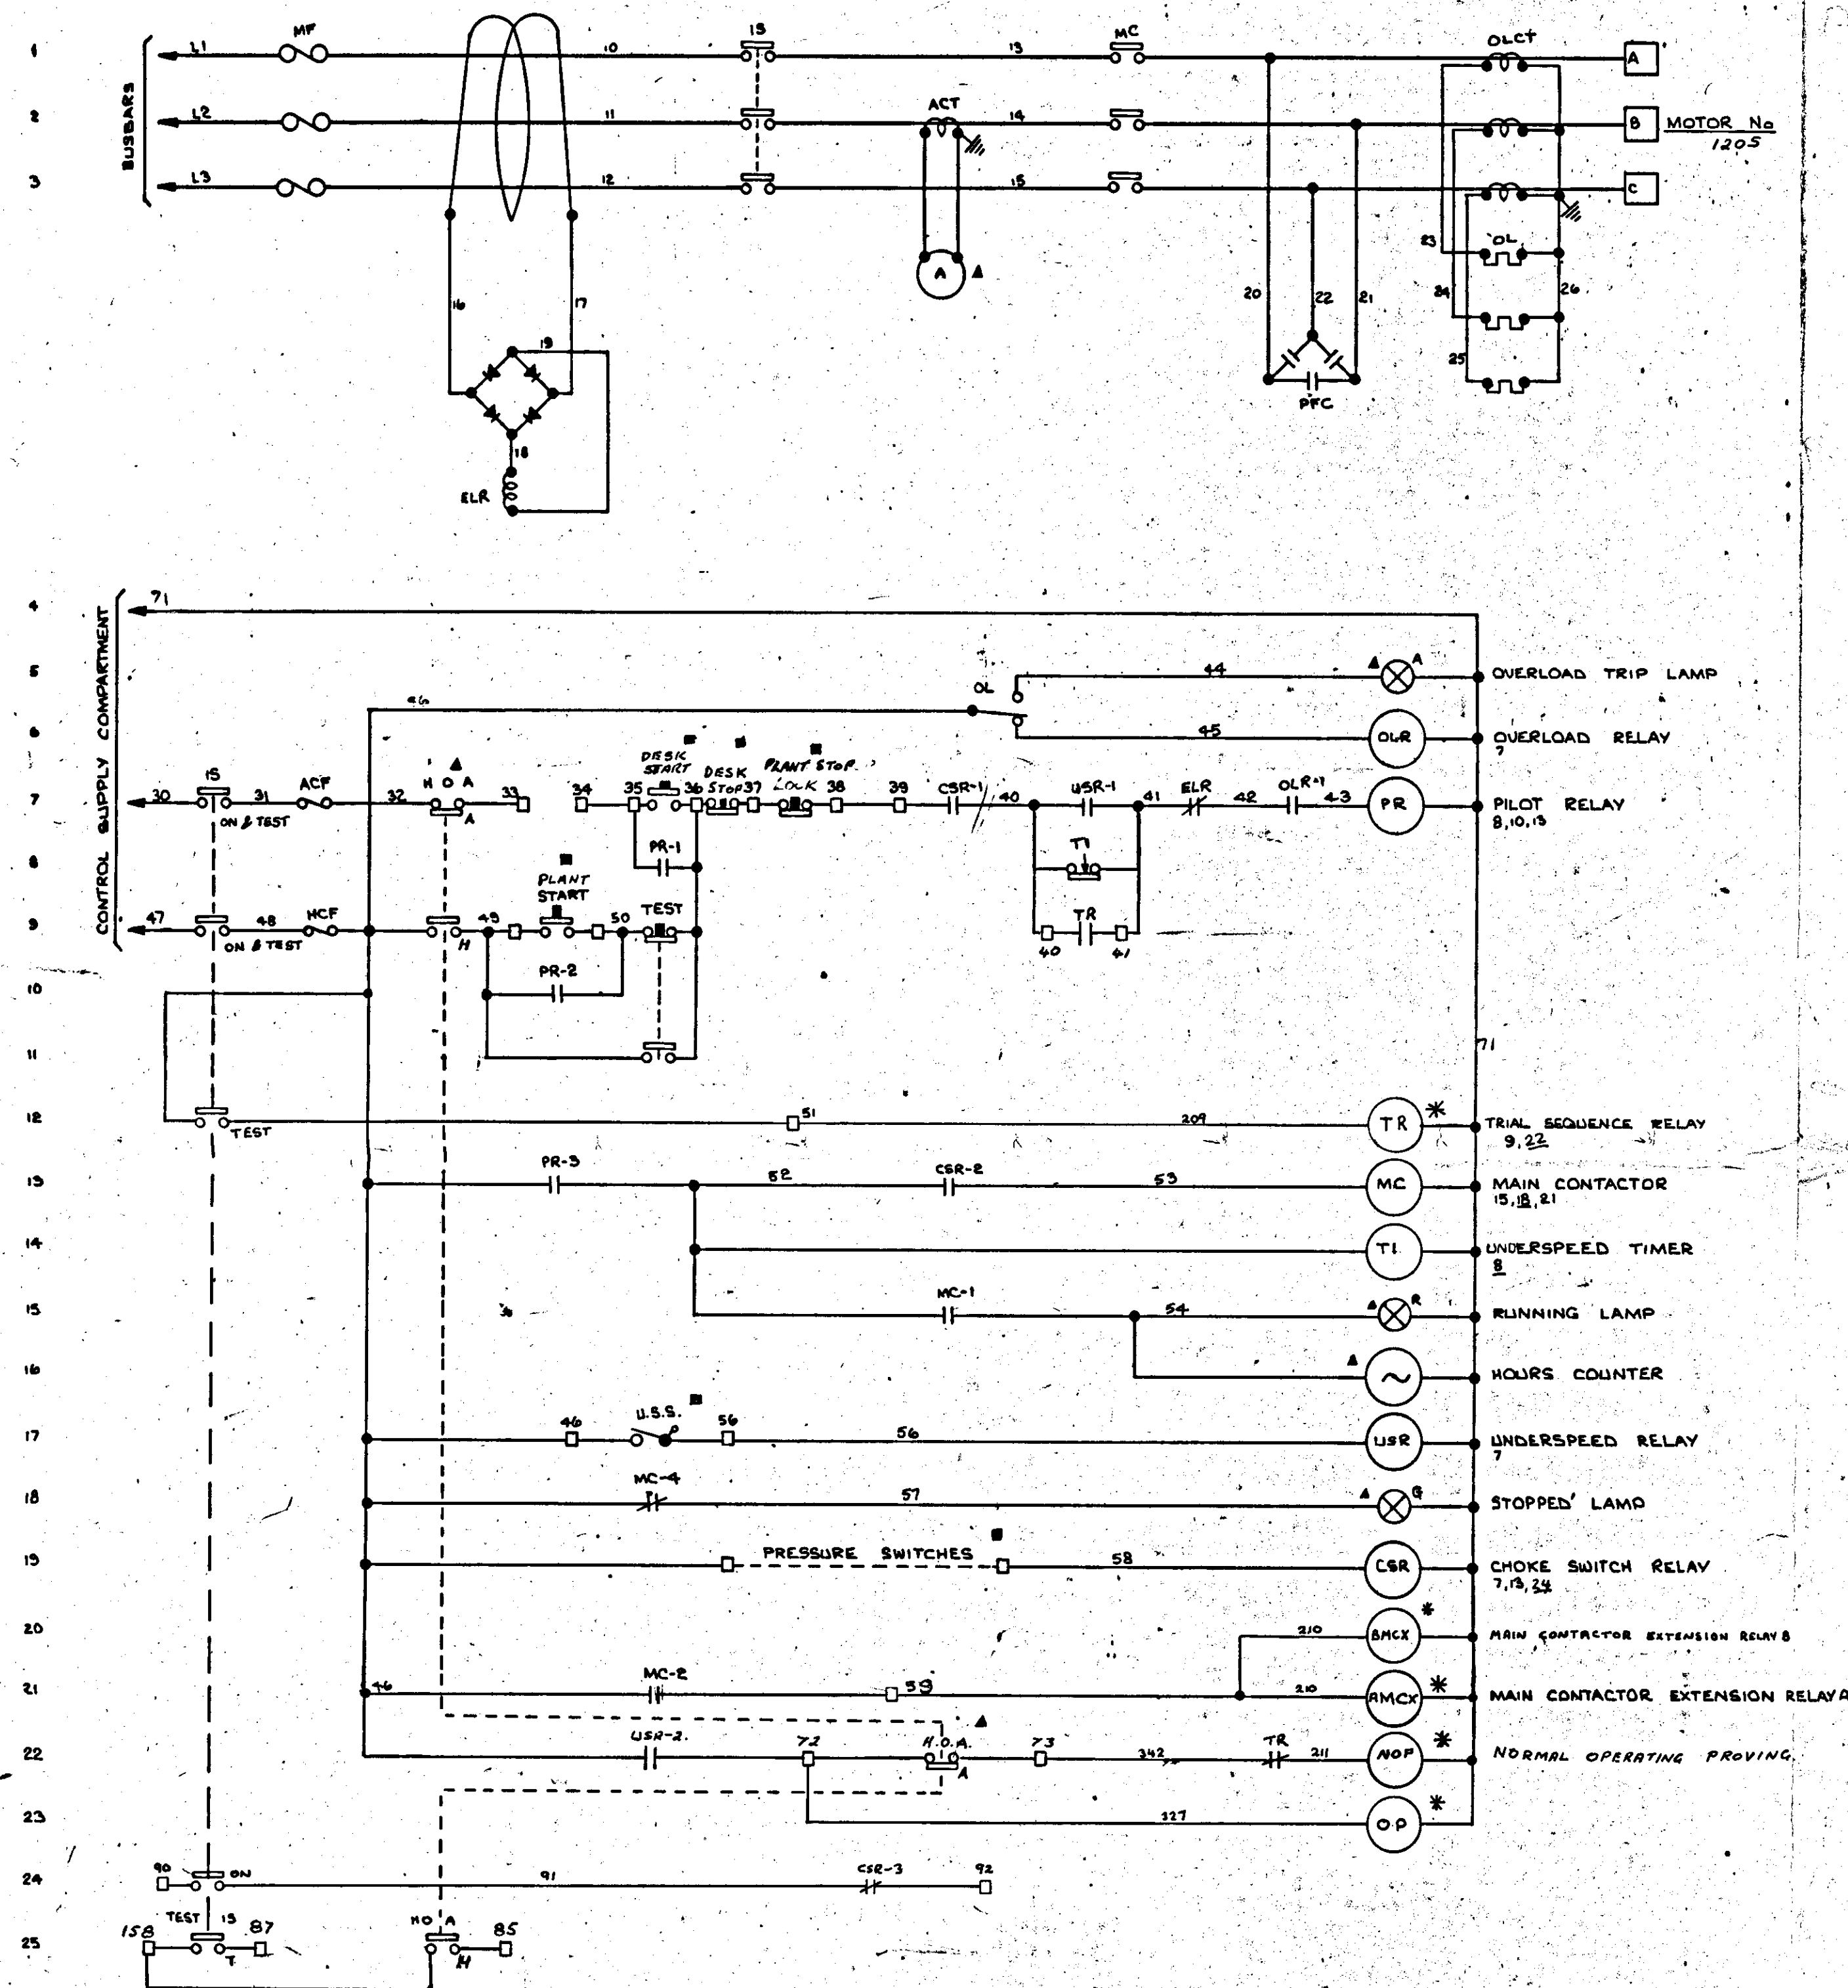

- * LOCATED IN RELAY PANEL
 ■ EXTERNAL CONTROL COMPONENTS
 ▲ LOCAL CONTROL COMPONENTS ON DOOR

DEWHURST & PARTNER LTD.

MELBOURNE WORKS

HOUNSLOW

TITLE:

BASEMENT CHAIN CONVEYOR No. 2

MCC12A

ALL CONTROL TERMINALS PREFIXED 12F

REVISION: 3

CSR MODIFICATIONS

ORIGIN: 2/2/77 SGD. A.M.

REVISION: 2

GENERAL MODS

ORIGIN: 2/2/77 SGD. A.M.

REVISION: 1

TSR ADDED, REDRAWN

ORIGIN: 2/2/77 SGD. A.M.

REVISION: 5
 TAIL, 100% PASSED
 29/4/77 A.L.J.B.

REVISION: 4
 GEN. MODS
 31/3/77 A.L.J.B.

DRAWN BY: A.M.
 DATE: 22.11.76
 CHECKED BY: [Signature]
 APPROVED BY: [Signature]
 DATE: 29.11.76






THE DESIGN AND MANUFACTURING INFORMATION CONTAINED IN THIS DRAWING IS THE EXCLUSIVE RIGHT OF DEWHURST & PARTNER LTD. AND MUST NOT BE COPIED OR USED FOR MANUFACTURING PURPOSES.

ISSUE 128486

CTX36ICF

CTX36ICF

KEY DIAG. No.
 EXT. DIAG. No.
 REL. DIAG. No.
 PANEL LAYOUT No.

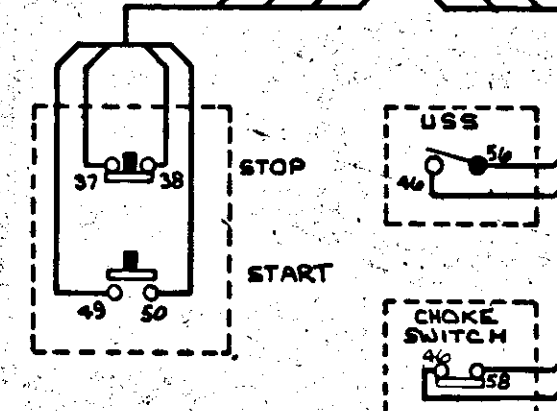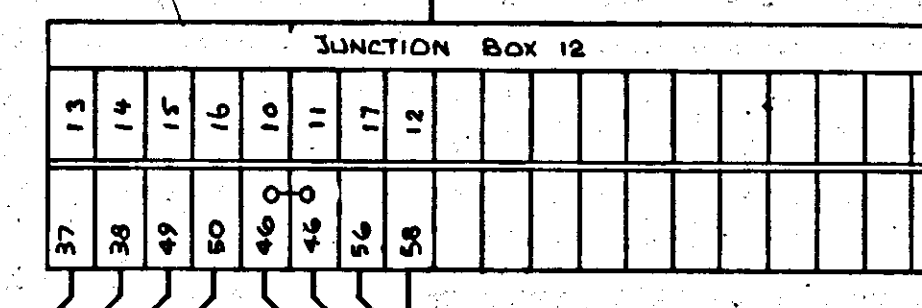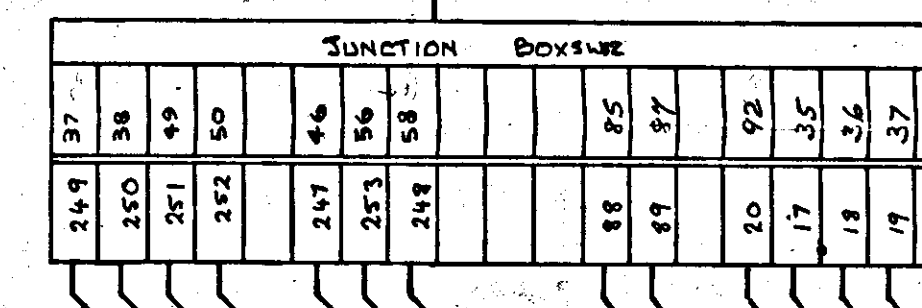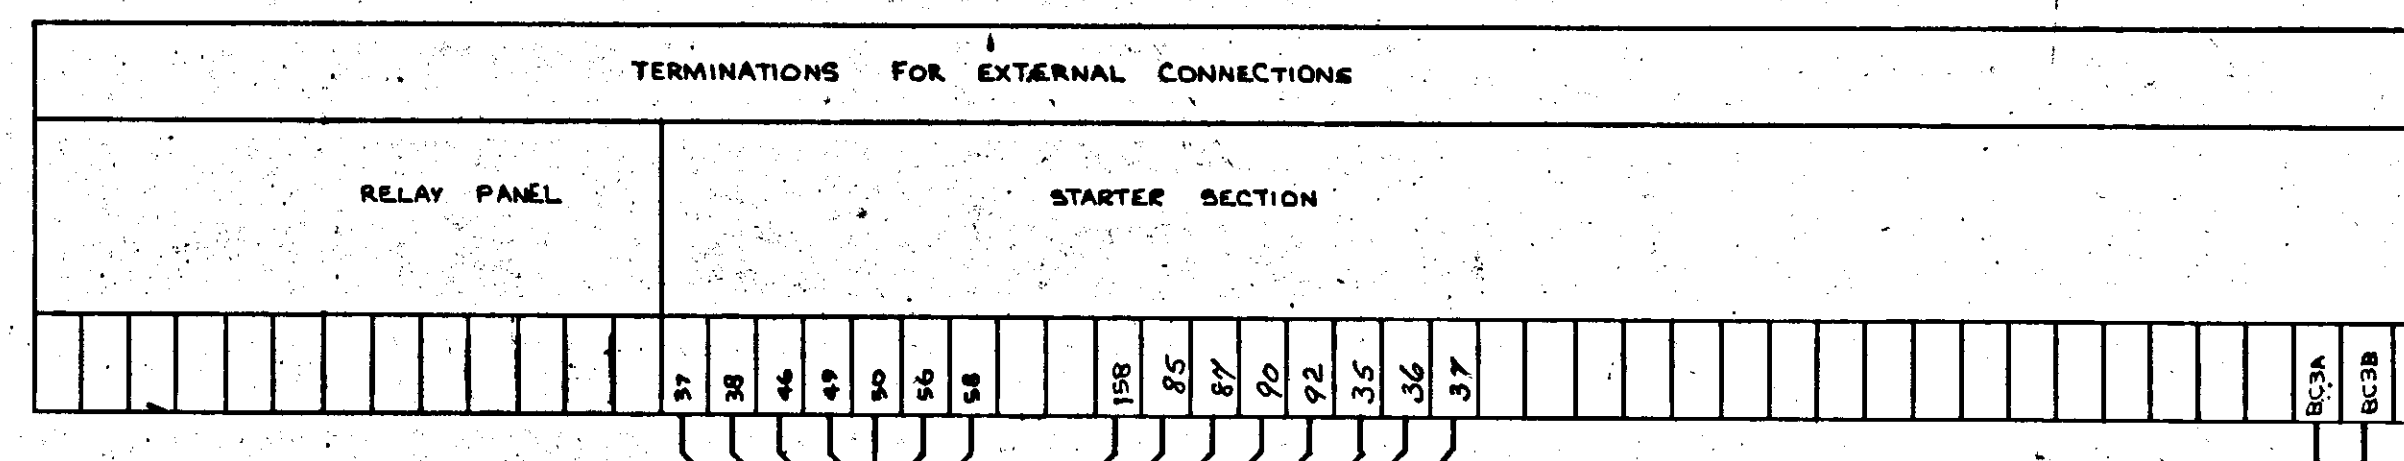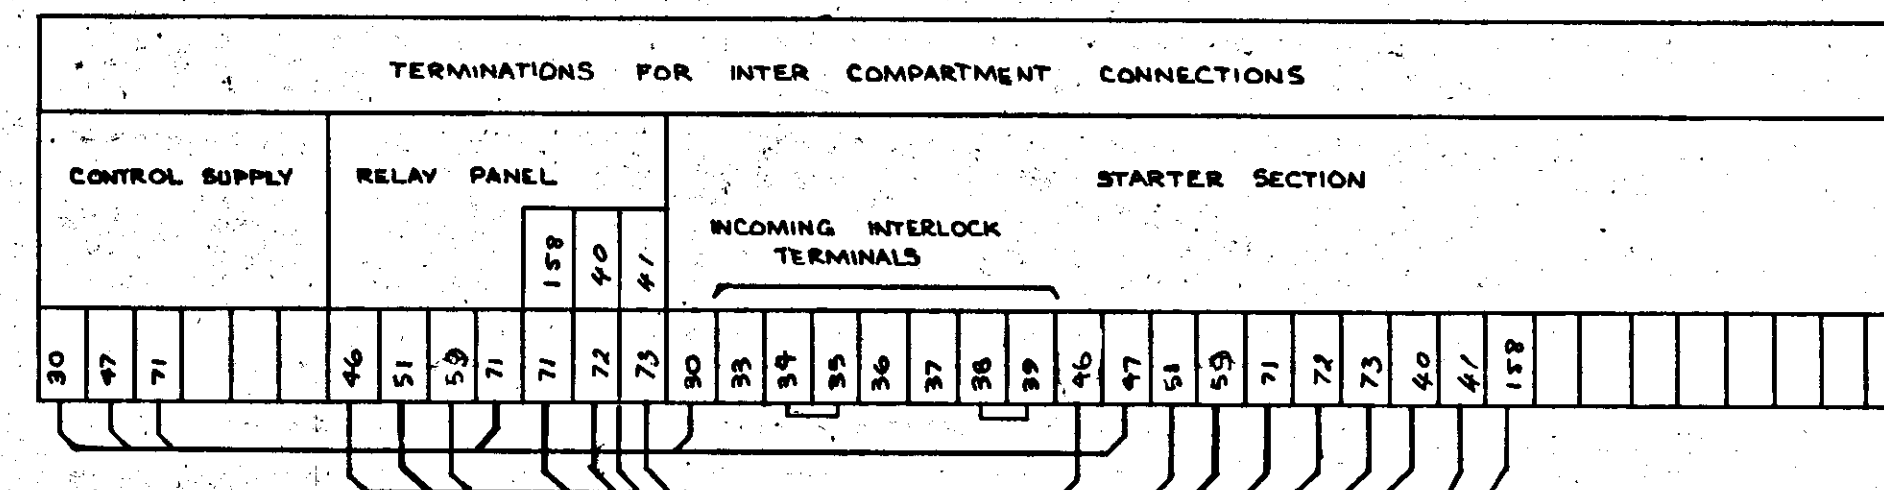

10802

8.