



DEWHURST & PARTNER LTD.
MELBOURNE WORKS HOUNSLOW

1	TITLE
---	-------

SCHEME FOR PANEL MCC12A — SEAFORTH GRAIN TERMINAL SILO II

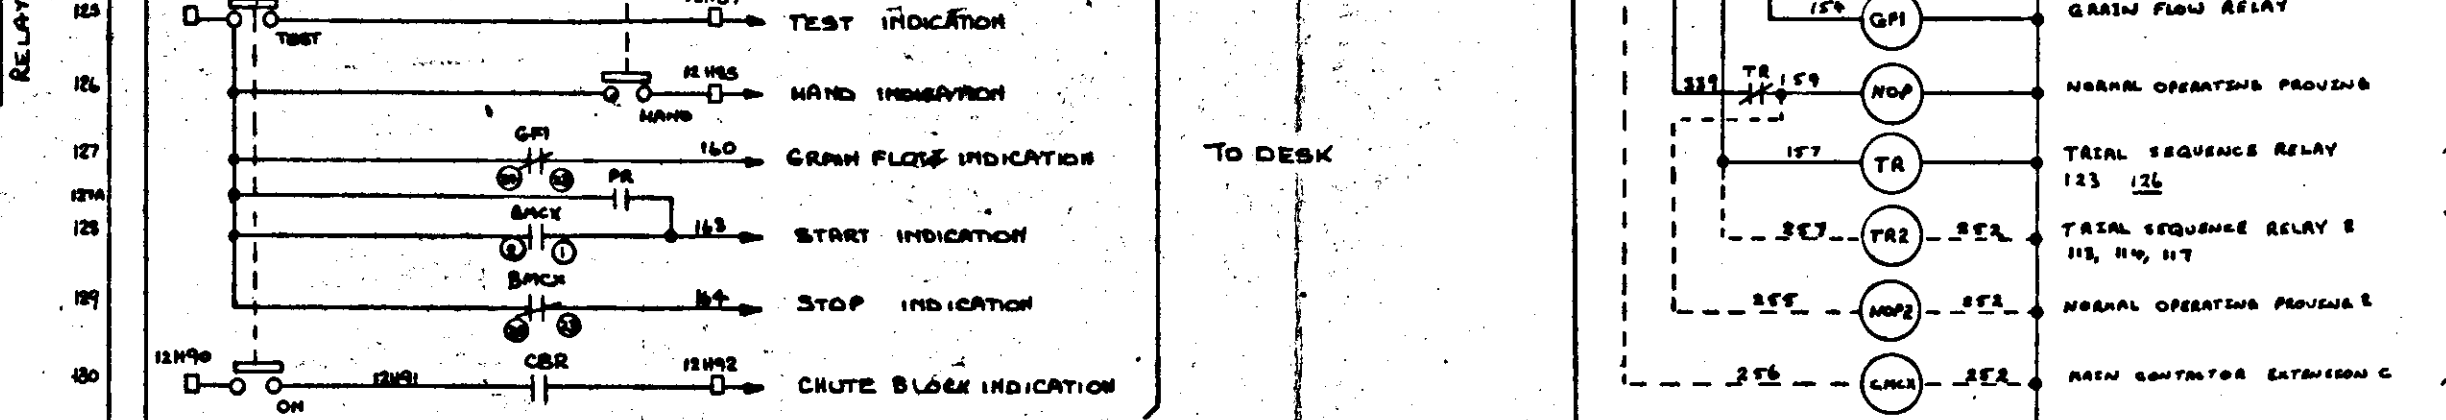

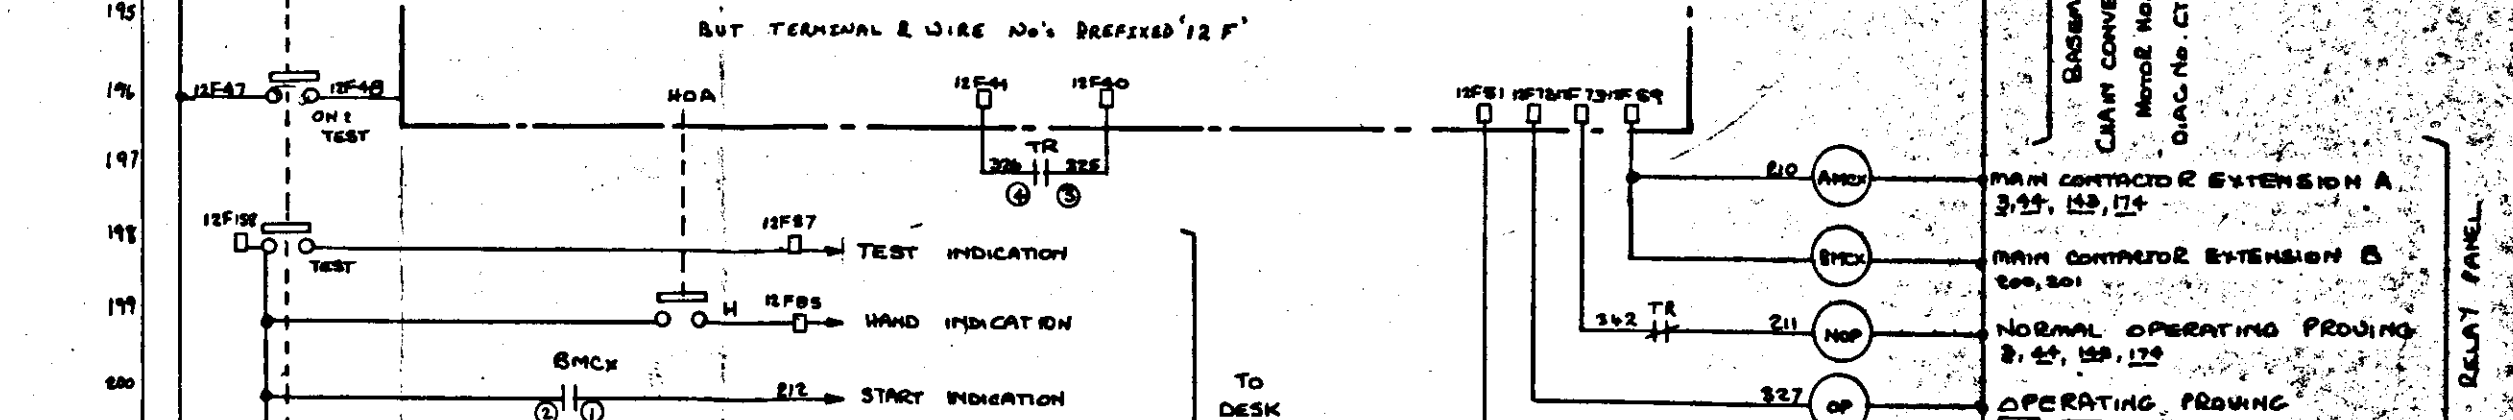

REVISION: 3		REVISION: 2		REVISION: 1		DRAWN BY	
-------------	--	-------------	--	-------------	--	----------	--

TELETYPE UNIT NO. 1	WIRE & CONTACTS	NEW RELAYS	DATE 17/3/77
WIRE NO. 1	NUMBERS ADDED	GR RELAYS	CHECKED BY
		ADDED	APPROVED BY

ORIGIN: 1cD 30/6/77 SGD. A-LTB	ORIGIN: 1cD 30/6/77 SGD. A-LTB	ORIGIN: 1cD 6/7/77 SGD. A-LTB	APPROVED BY
			DATE

1-14	THE DESIGN AND MANUFACTURING INFORMATION CONTAINED IN THIS DRAWING IS THE EXCLUSIVE RIGHT OF DEWHURST & PARTNER LTD. AND MUST NOT BE COPIED OR USED FOR MANUFACTURING PURPOSES.	ISSUE	1	2	3	4	5	6	7	8	9	10	
	KEY DIAG. No.	DTX 361DM											
	EXT. DIAG. No.												
	REL. DIAG. No.												
	PANEL LAYOUT No.												
		SHEET 1 OF 2											