



10795

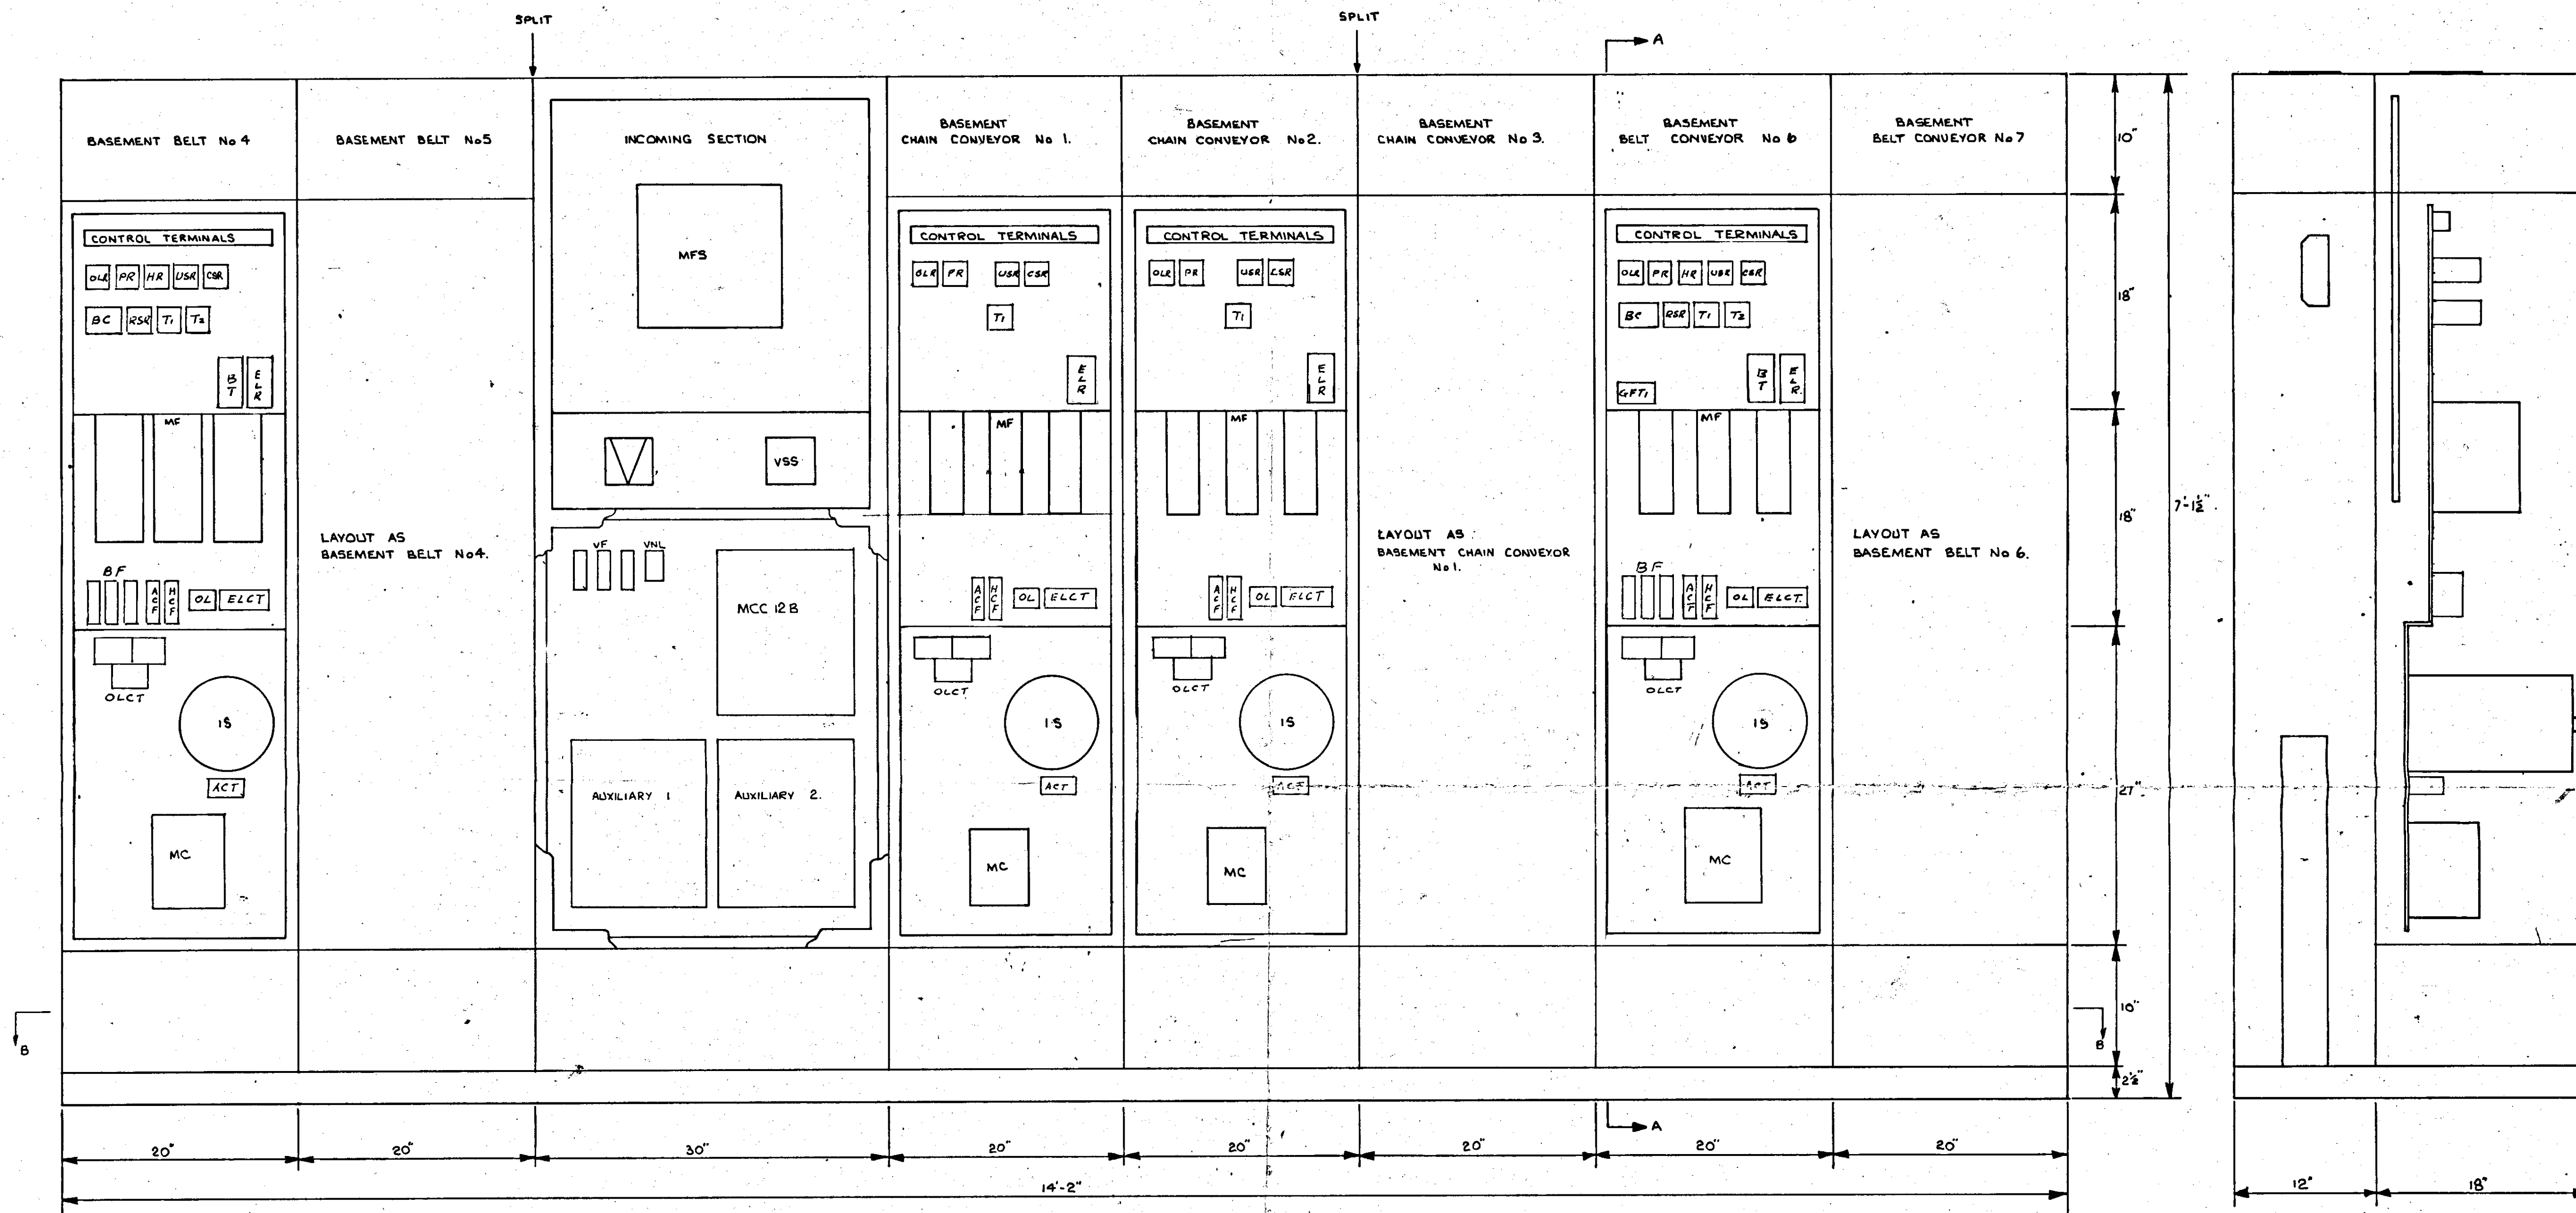

SECTION B-B
SCALE: 1/4" = 1'

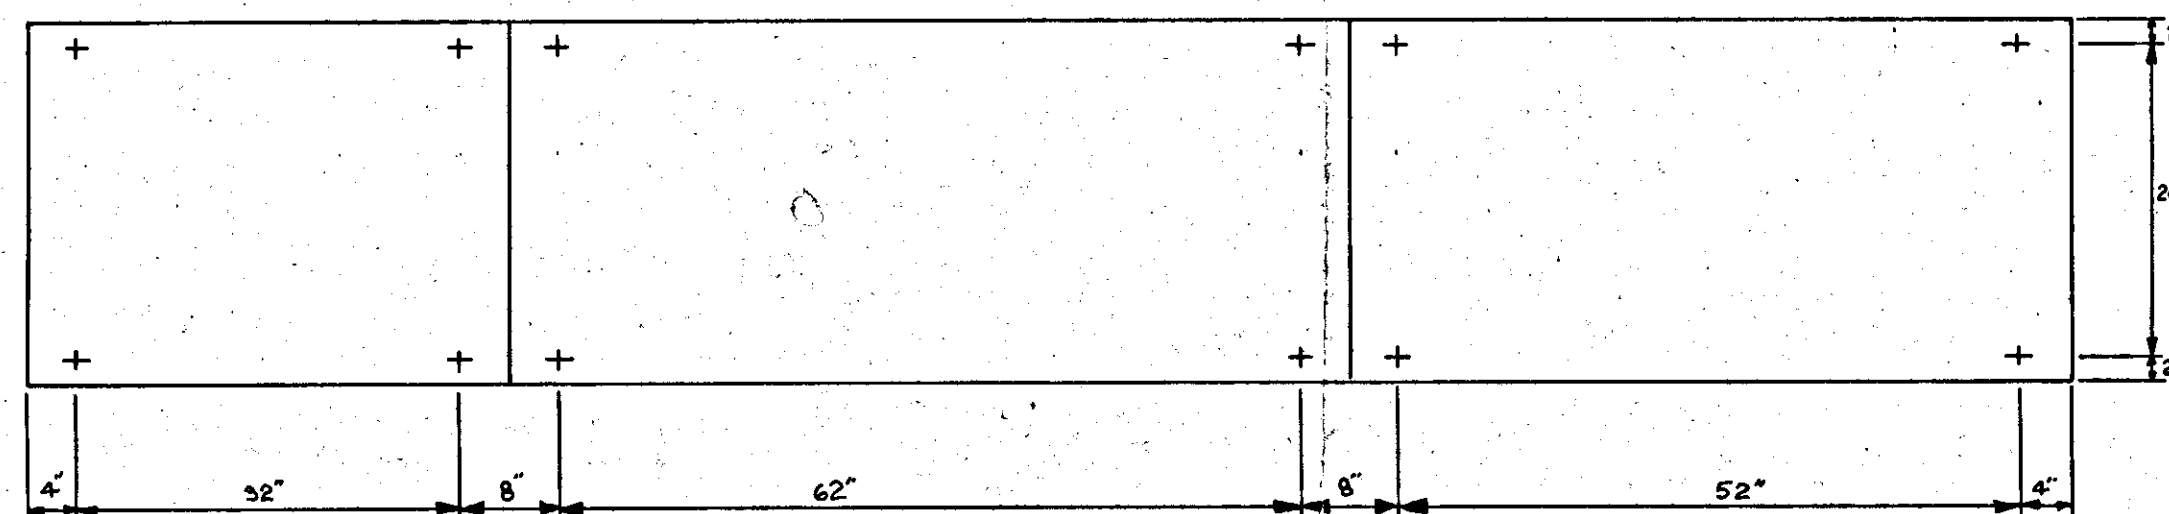

DEWHURST & PARTNER LTD.
MELBOURNE WORKS HOUNSLOW

TITLE:
LAYOUT OF MCC 12A - SEAFORTH GRAIN TERMINAL

REVISION: 4.
MF SIZE ON
BCCI MODIFIED.
5/4/77 A.M.

REVISION: 3.
COMPONENT
LAYOUT CHANGES
ORIGIN:
4/12/77 SGD.

REVISION: 2.
PLUGGING CONTACTS
REMOVED.
ORIGIN:
2/11/76 SGD. A.M.

REVISION: 1.
S/F ON INCOMING
SECTION MODIFIED.
ORIGIN:
2/19/76 SGD. A.M.

DRAWN BY A.M.
DATE 18.8.76
CHECKED BY
APPROVED BY
DATE 23.8.76

KEY DIAG. No.
EXT. DIAG. No.
REL. DIAG. No.
PANEL LAYOUT No.

10795

THE DESIGN AND MANUFACTURING
INFORMATION CONTAINED IN
THIS DRAWING IS THE EXCLUSIVE
RIGHT OF DEWHURST & PARTNER
LTD. AND MUST NOT BE COPIED
OR USED FOR MANUFACTURING
PURPOSES.

ISSUE 12/1/75
GTX36IBJ
GTX36IBJ