
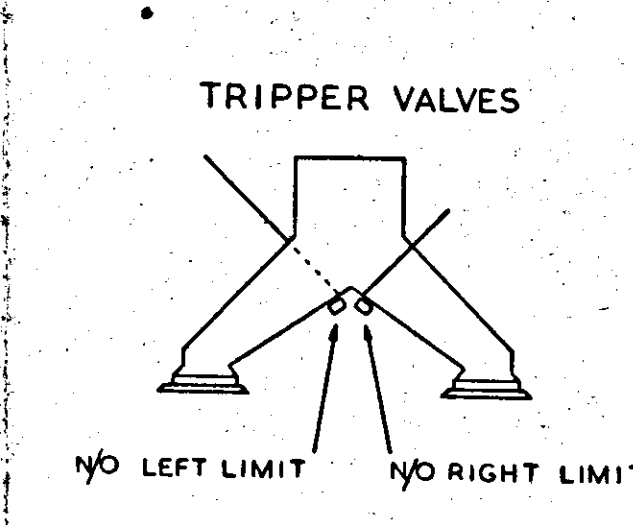


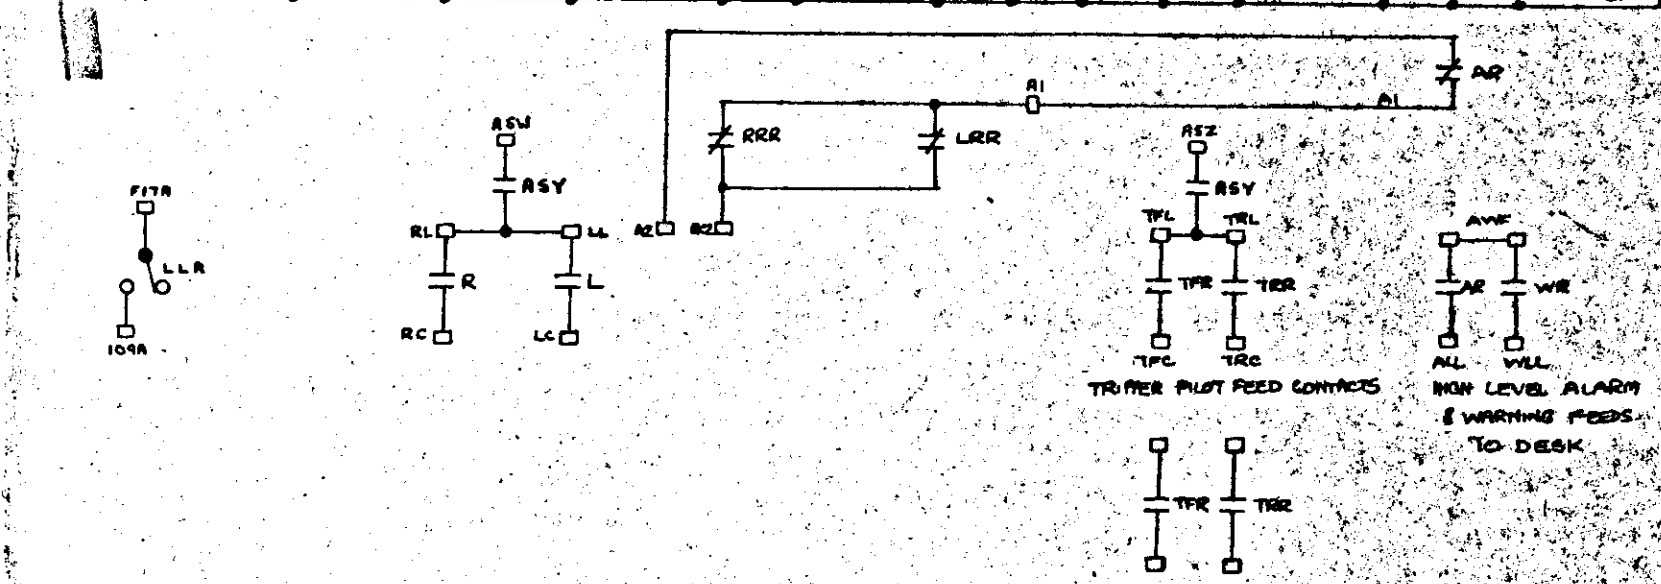

REVISION: 5 L&L + ASSOCIATED CONTRACTORS ADDED:	REVISION: 4 L&L + ASSOCIATED CONTRACTORS ADDED:	REVISION: 3 L&L CONTRACTORS RE ² L&L ADDED, ALSO CONTRACTORS TEL W&L & L TEL W&L L&L	REVISION: 2 DIRECTION OF LIMITS ADDED	REVISION: 1 REFERENCE ASSOCIATED PLUS DETAILS OF NEW WORK - SEE DRAWING + SEE NEW DRAWINGS ORIGIN: 14B
ORIGIN: 14B 1/16/78 SGD. <i>A.L.B.</i>	ORIGIN: 14B 2/13/78 SGD. <i>A.L.B.</i>	ORIGIN: 14B 2/13/78 SGD. <i>A.L.B.</i>	ORIGIN: 14B 2/14/78 SGD. <i>A.L.B.</i>	ORIGIN: 14B 2/15/78 SGD. <i>A.L.B.</i>