


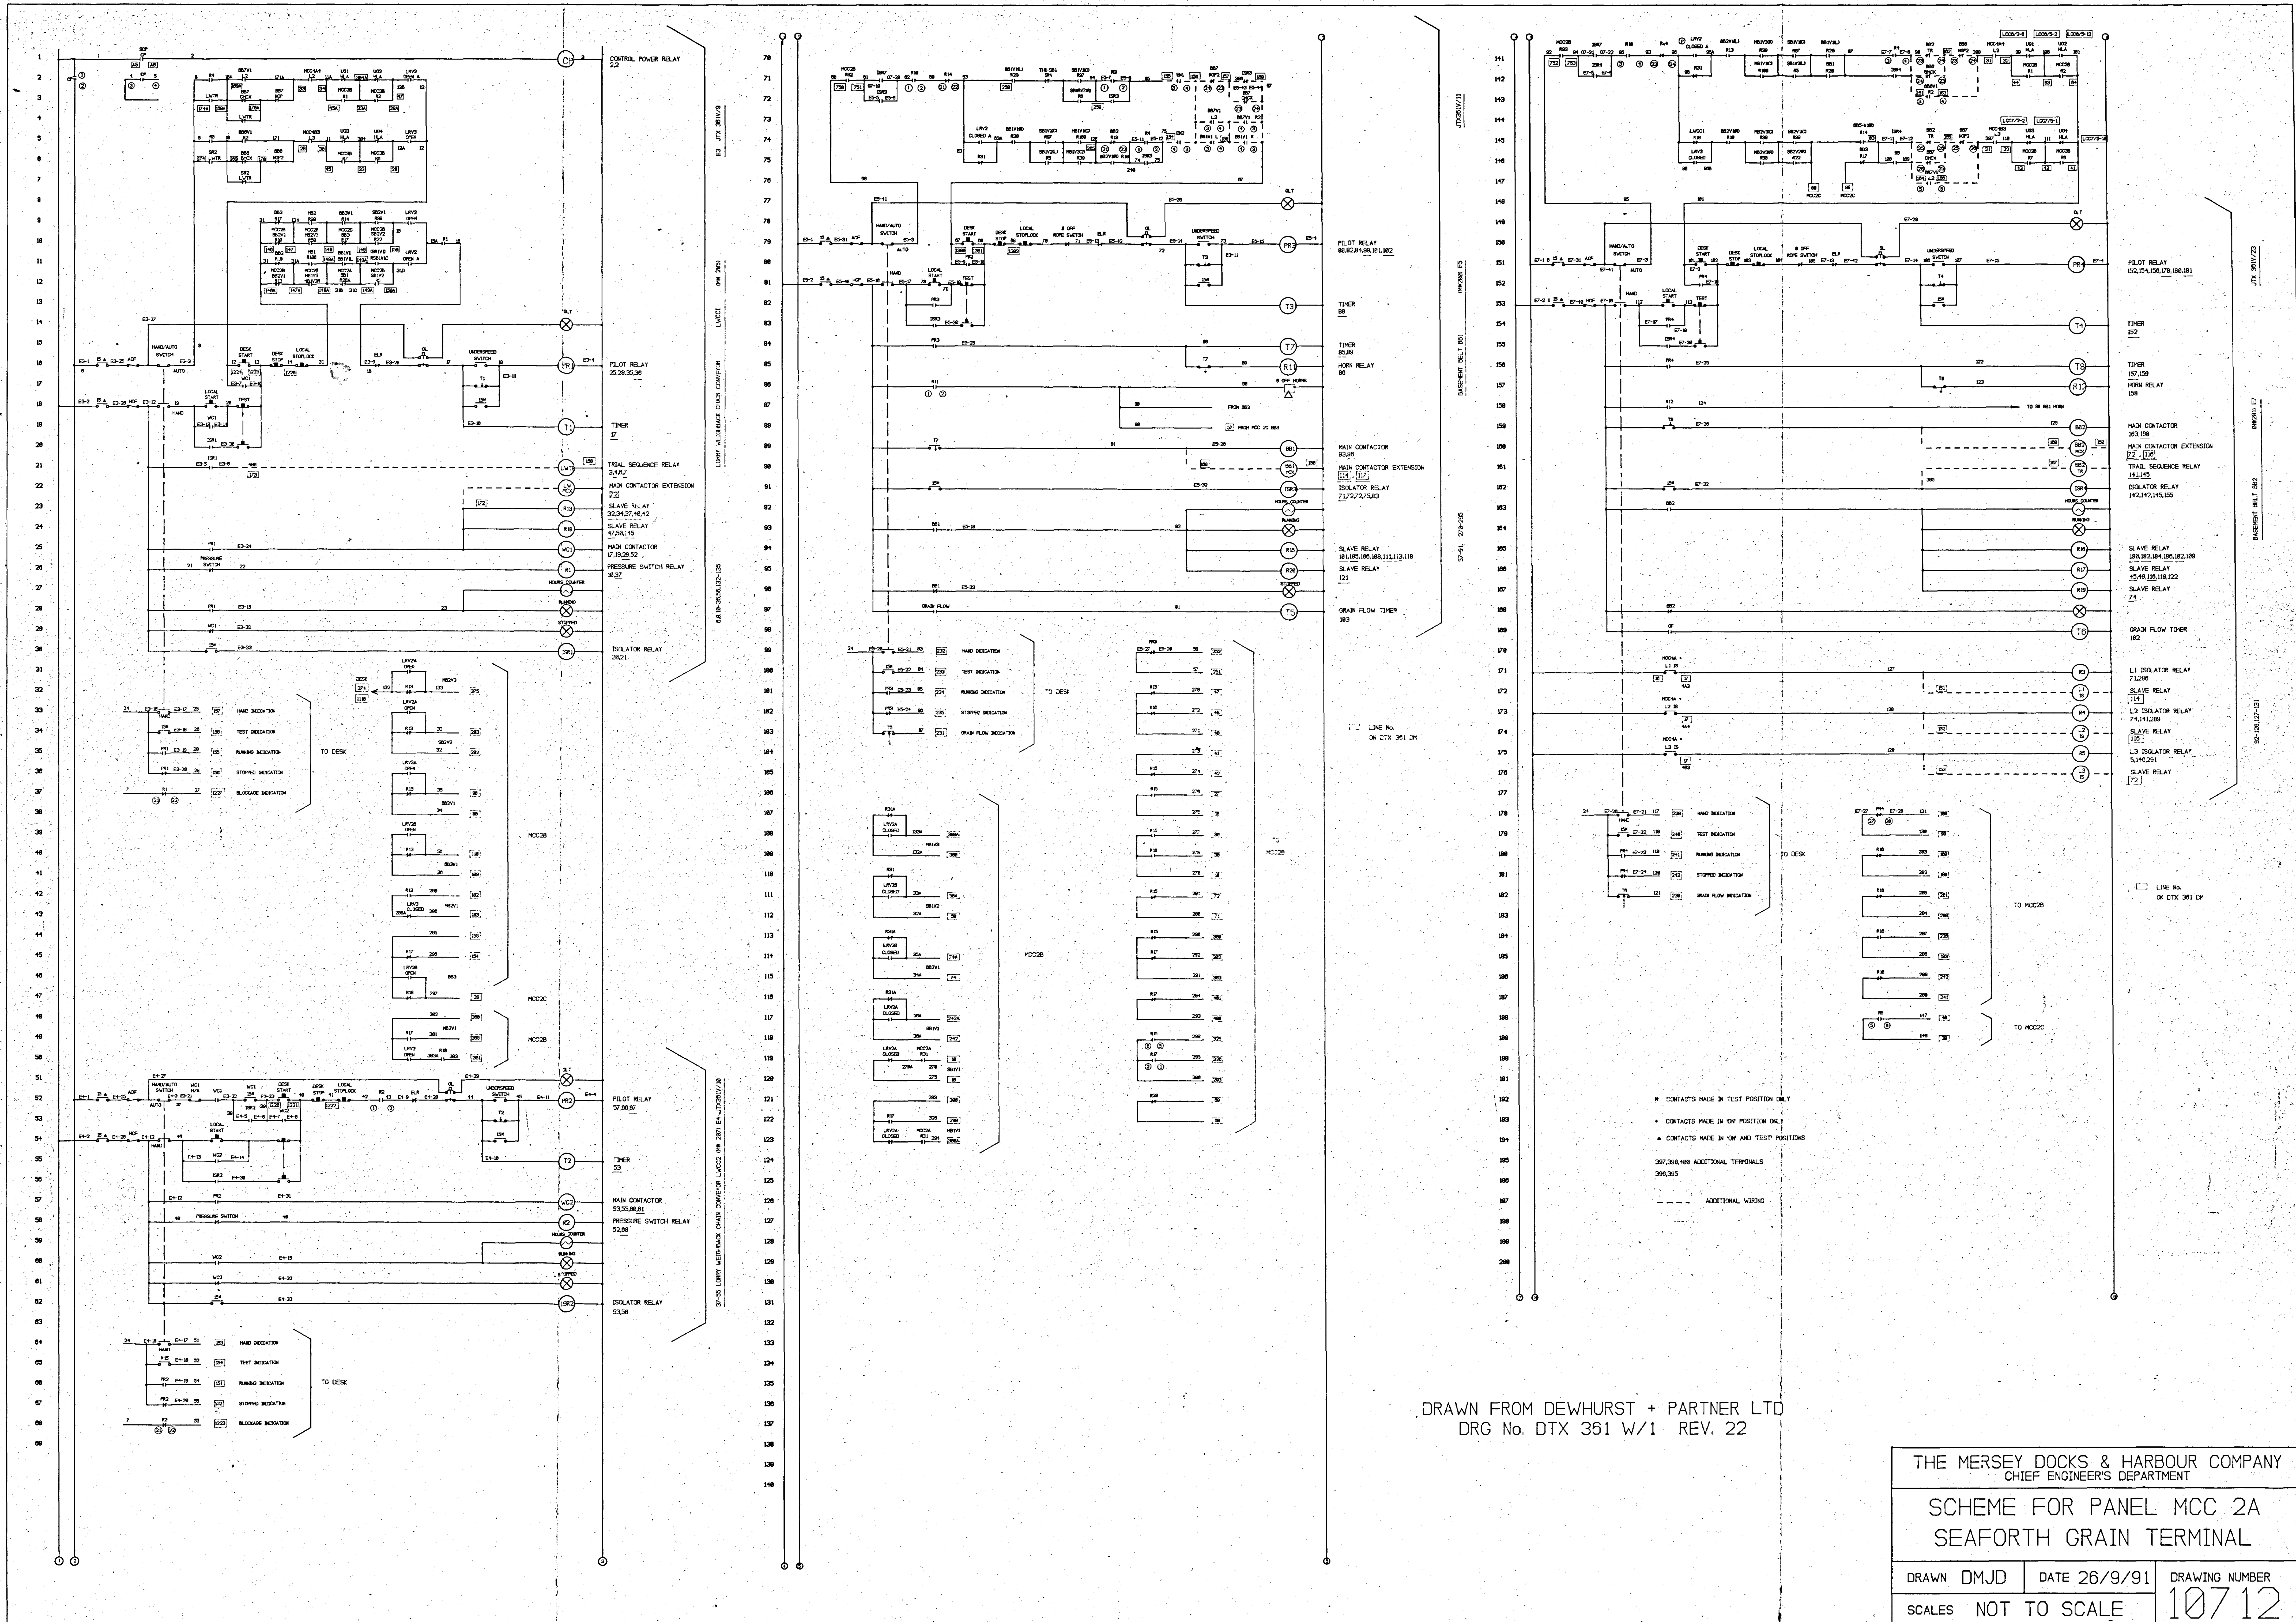

DRAWN FROM DEWHURST + PARTNER LTD
DRG No. DTX 361 W/1 REV. 22

THE MERSEY DOCKS & HARBOUR COMPANY CHIEF ENGINEER'S DEPARTMENT		
SCHEME FOR PANEL MCC 2A SEAFORTH GRAIN TERMINAL		
DRAWN DMJD	DATE 26/9/91	DRAWING NUMBER
SCALES NOT TO SCALE		10712