

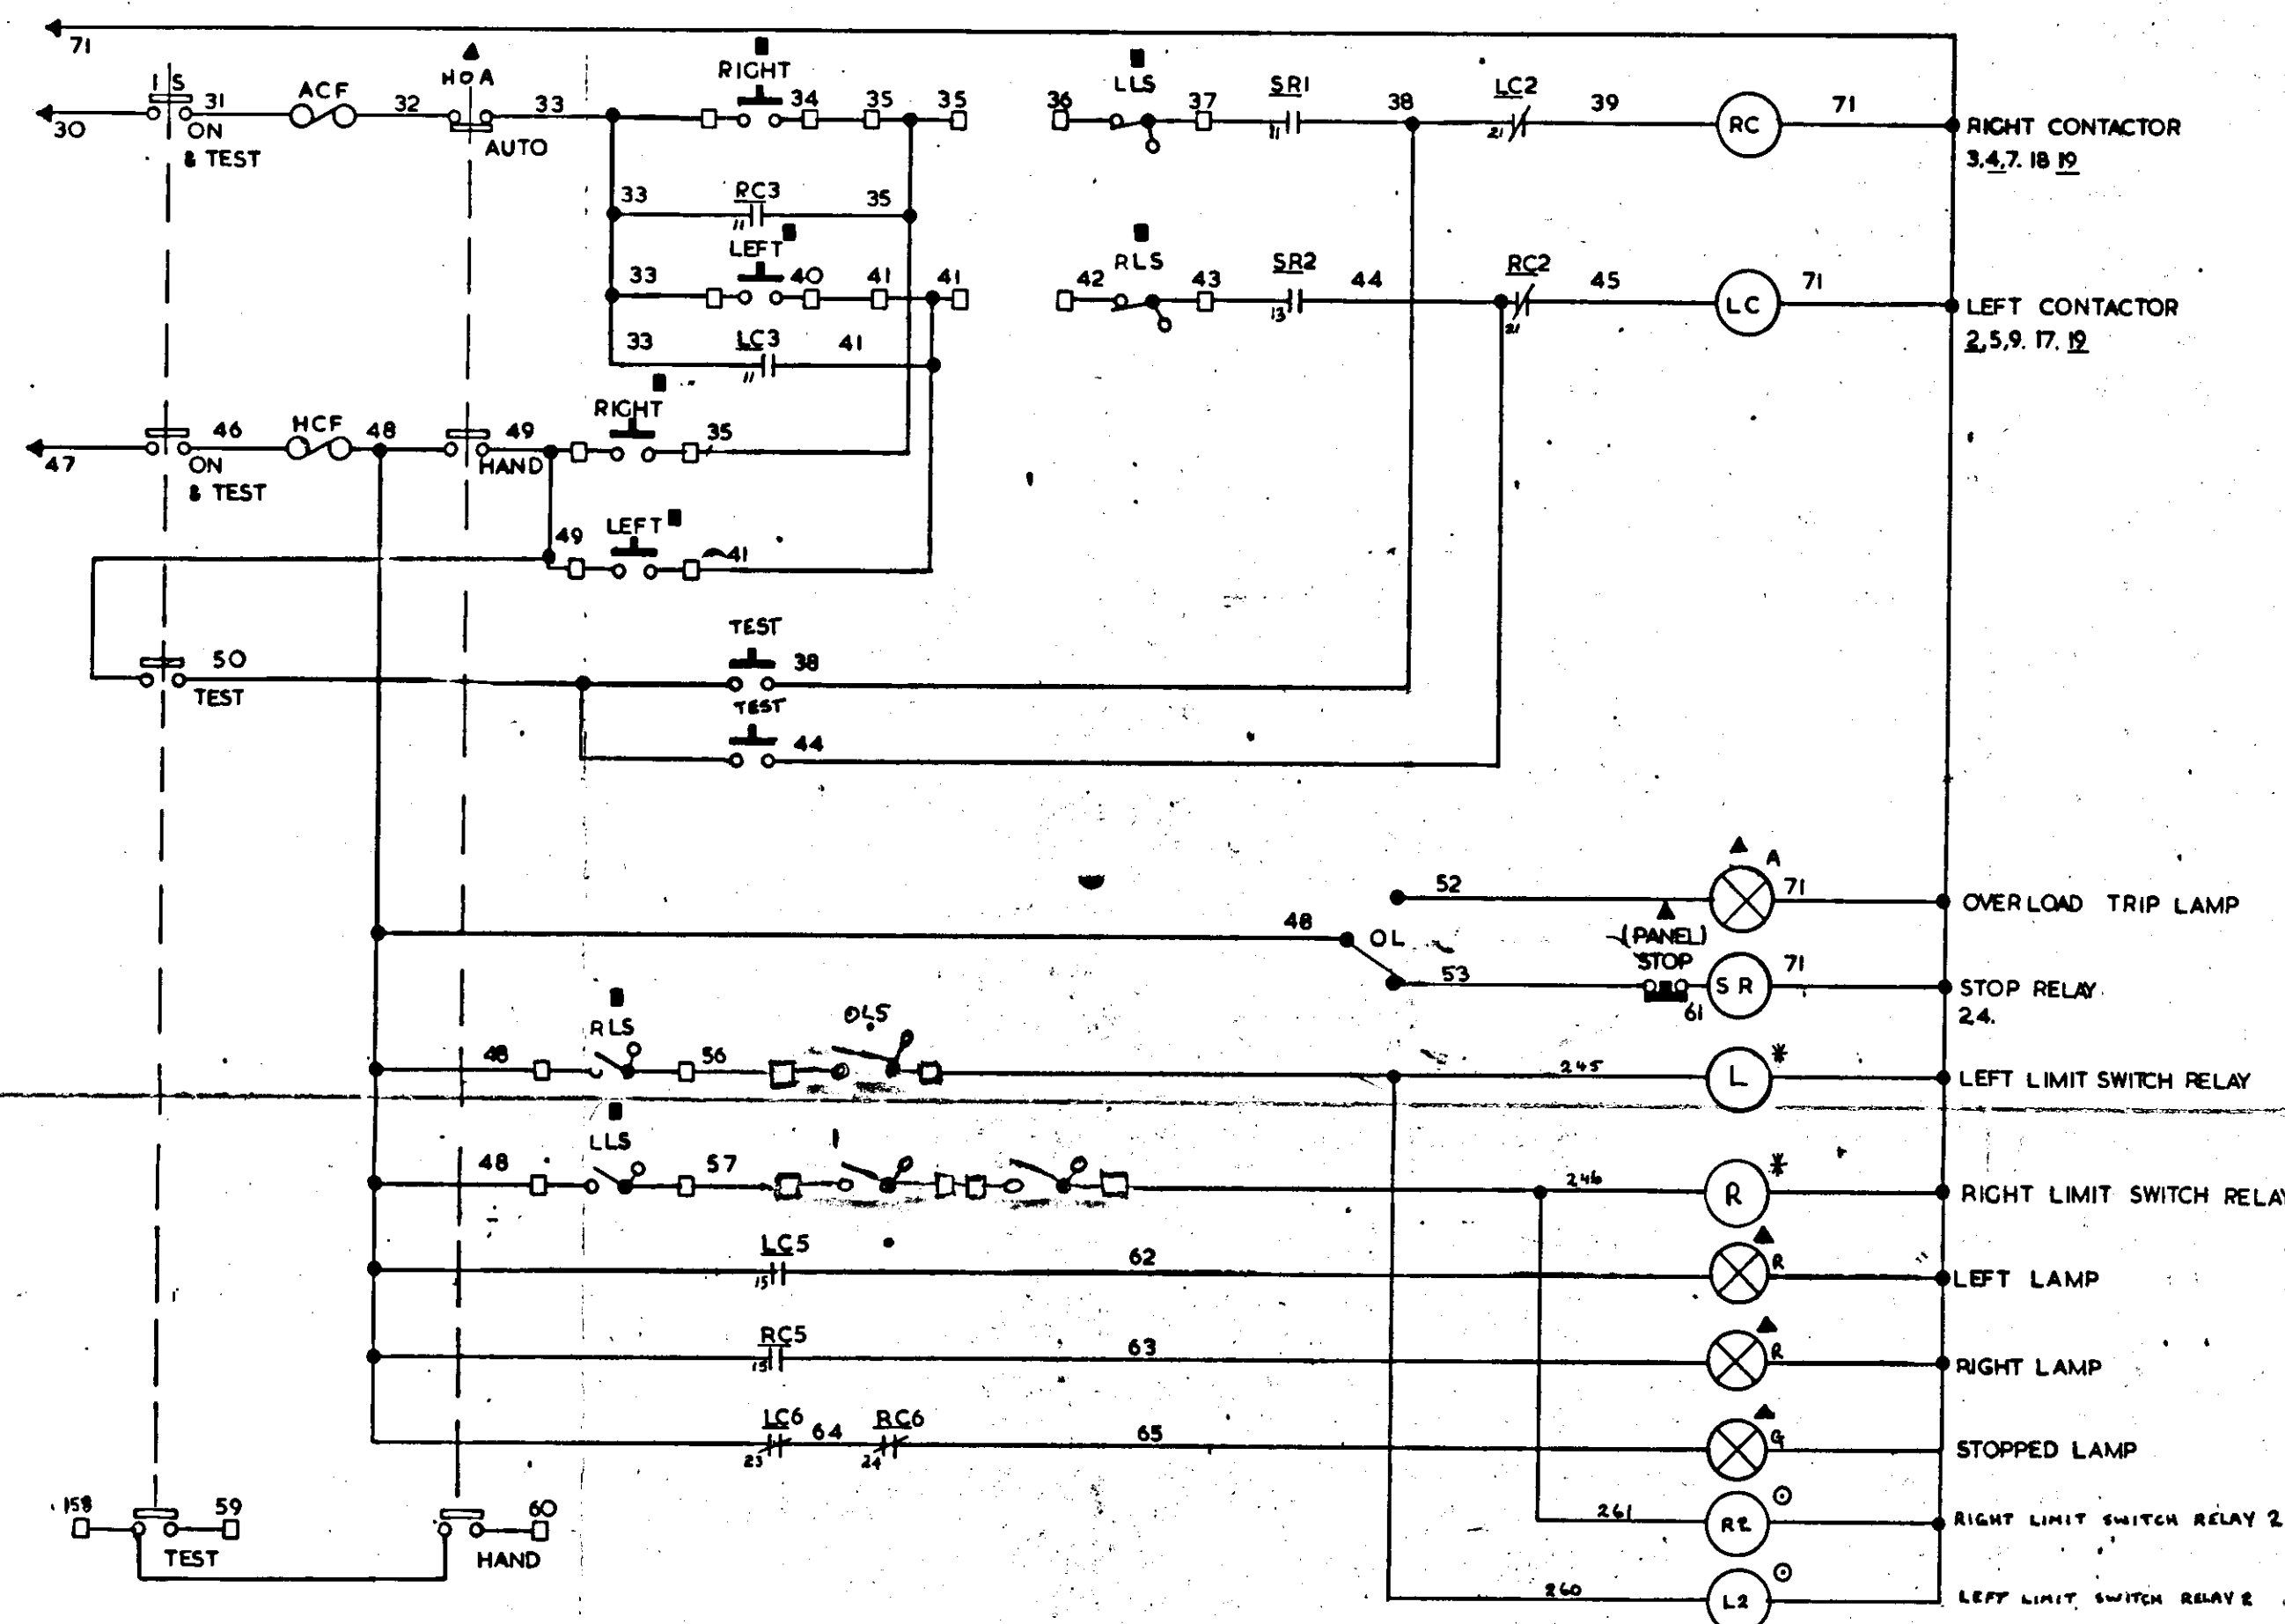
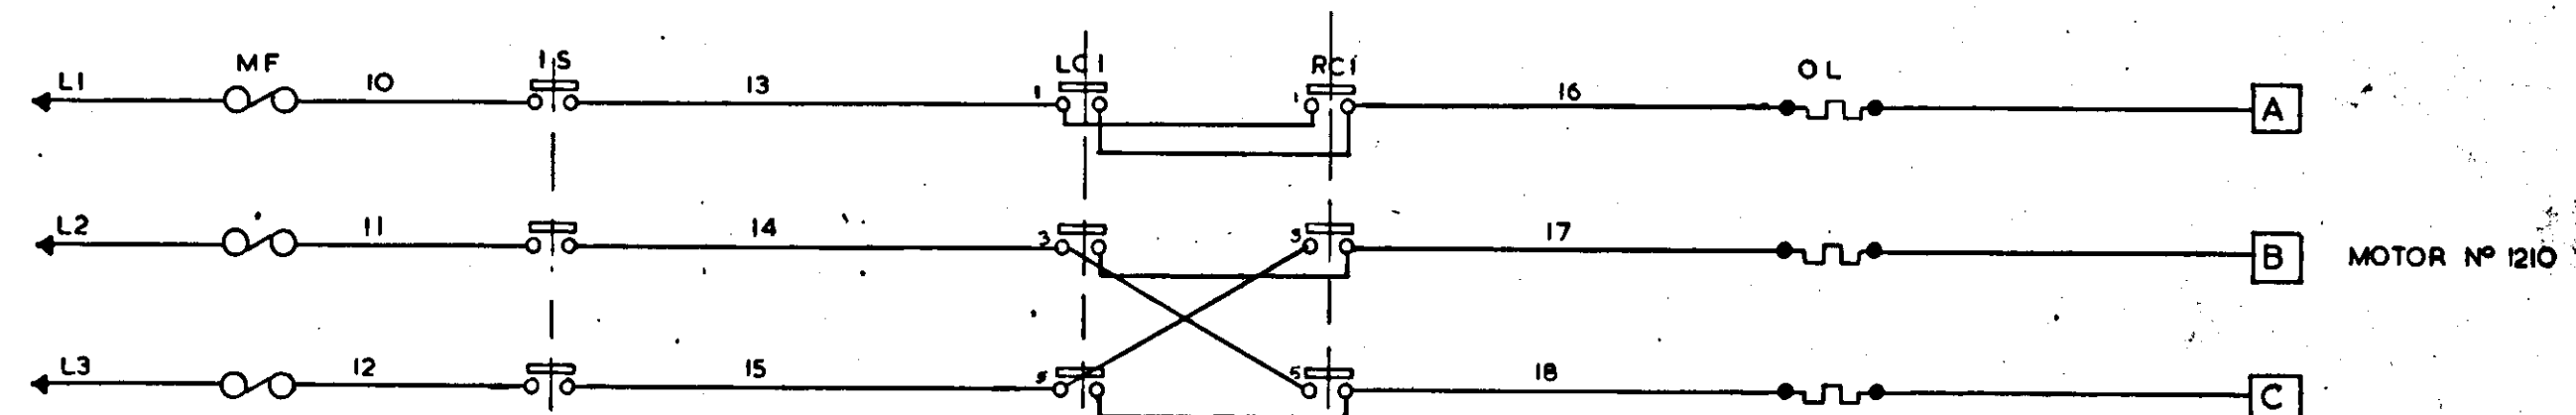
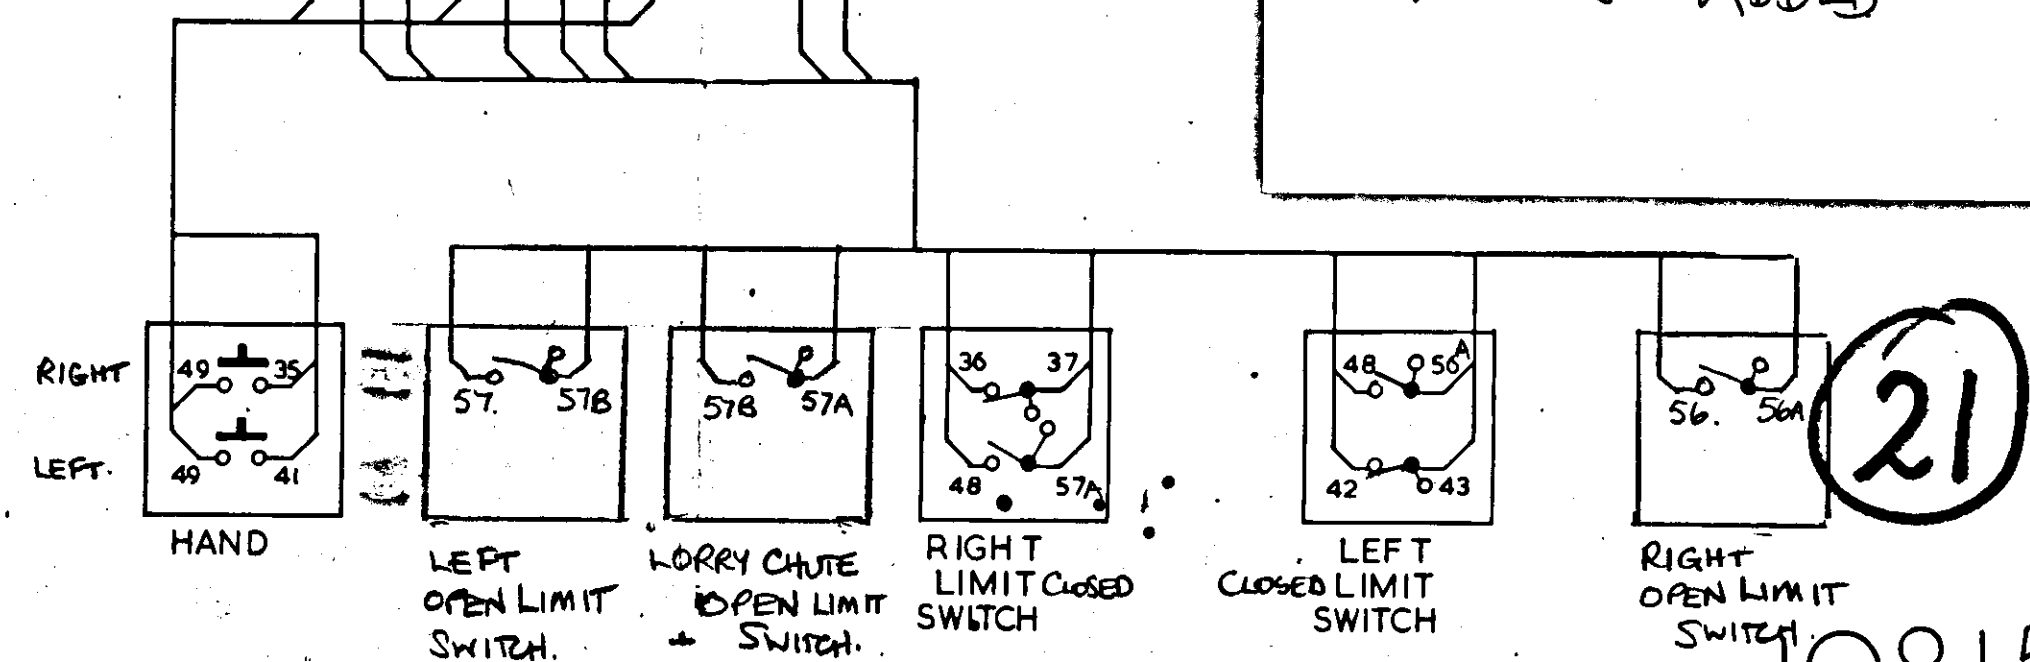
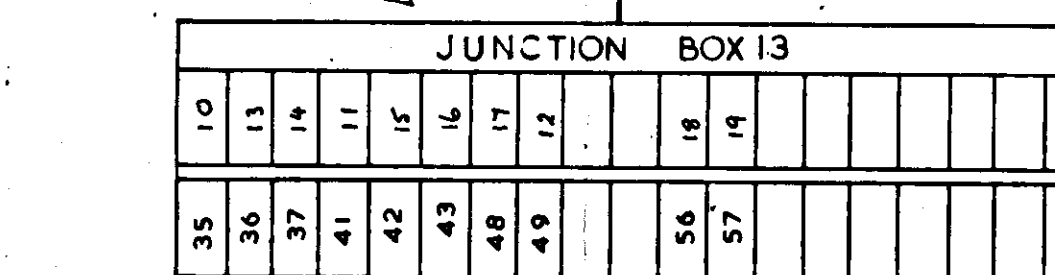
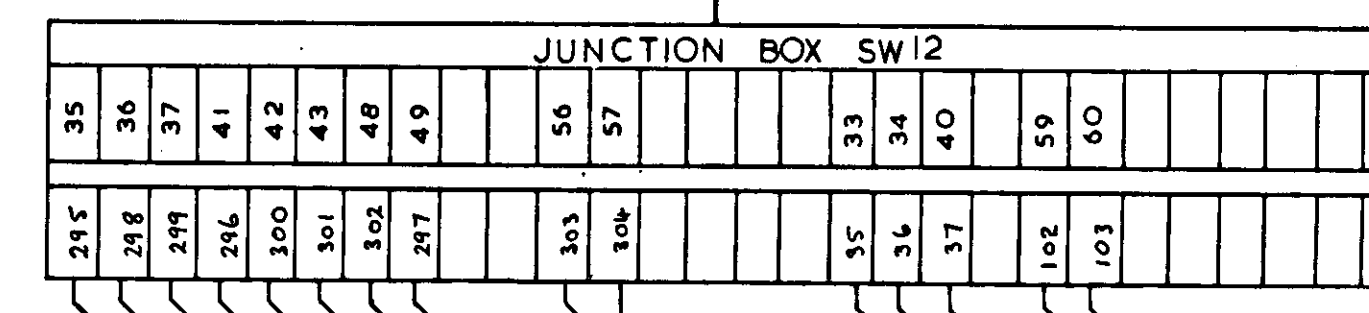


10815

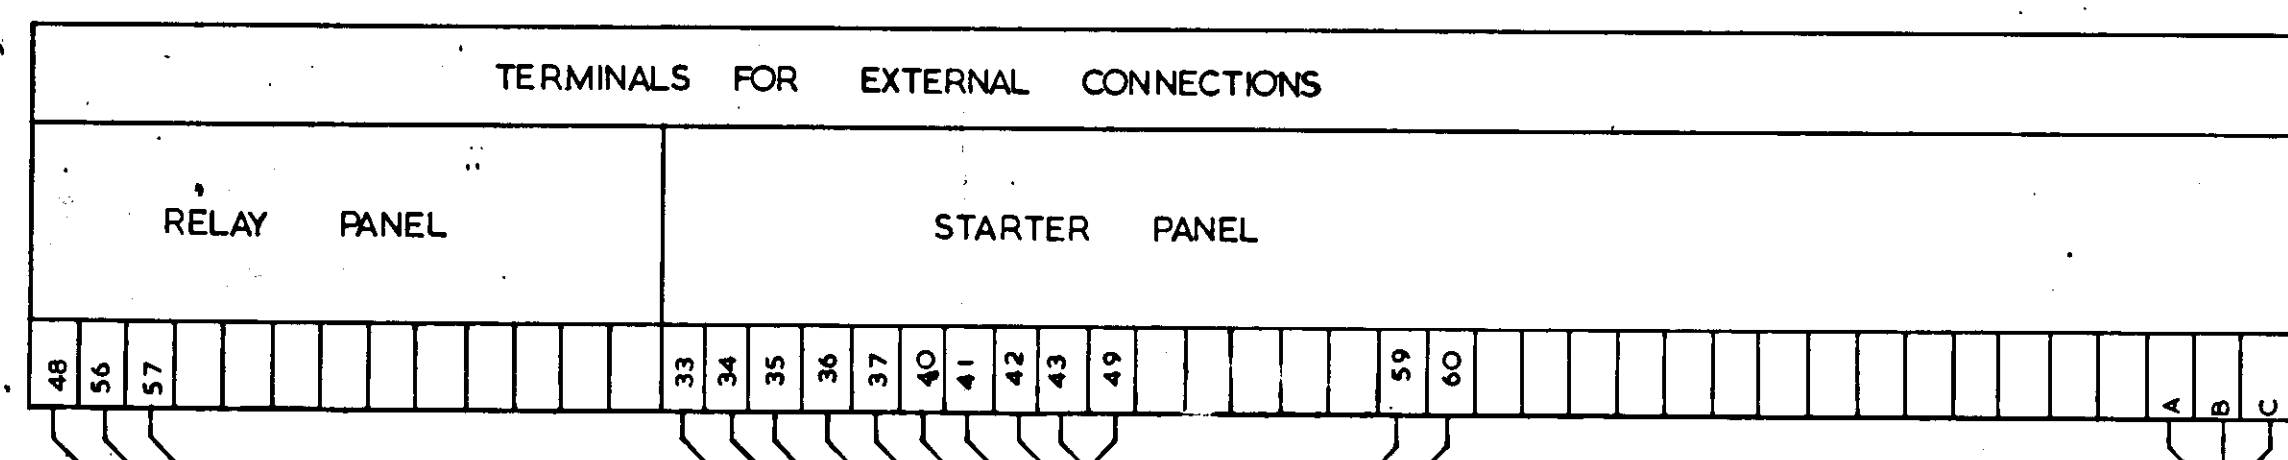

- LOCATED IN SW/CH 2 RELAY PANEL
- * LOCATED IN RELAY PANEL
- EXTERNAL CONTROL COMPONENTS
- ▲ LOCAL CONTROL COMPONENTS ON DOOR.

VALVE RIGHT POSITION ROUTED TO ELEVATOR L1
VALVE LEFT POSITION ROUTED TO ELEVATOR L2

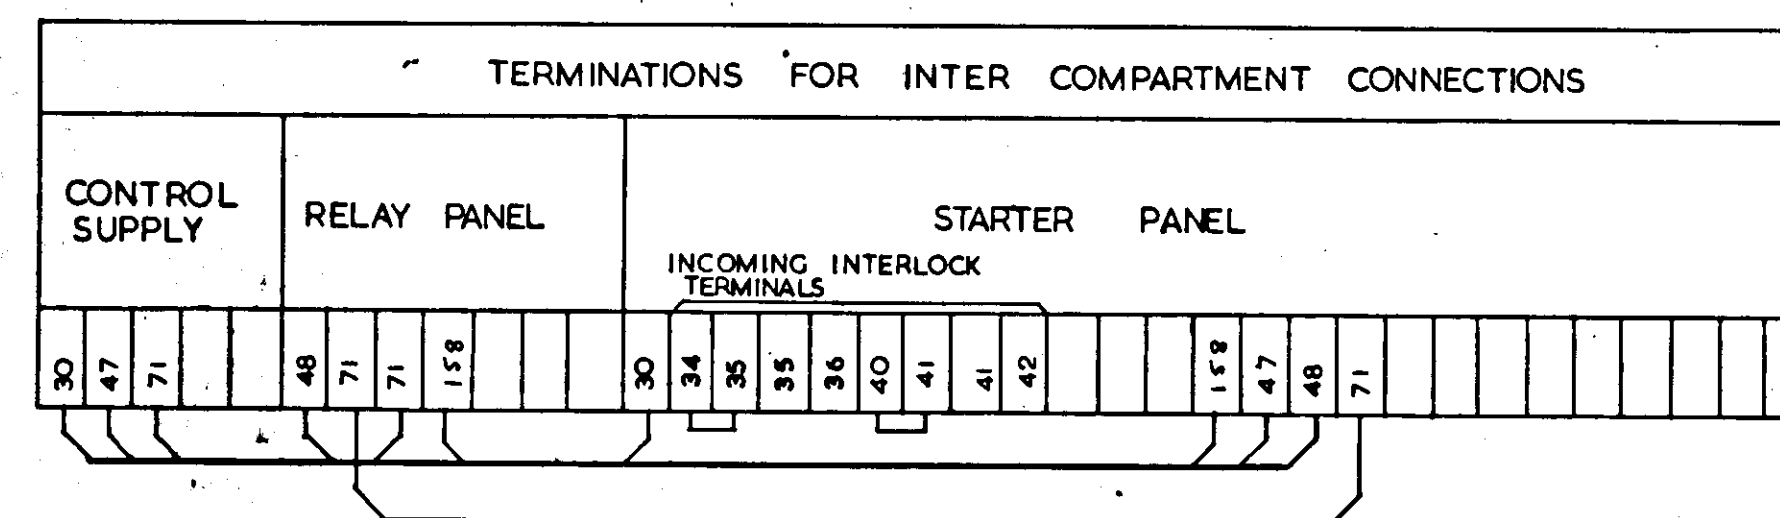

TO BE REVISED
LORRY LOADING CHUTE
LIMITS ADDED

DEWHURST & PARTNER LTD.

MELBOURNE WORKS

HOUNSLOW

TITLE:

BASEMENT BELT 7 VALVE 1

MCC12B

BB7V1

REV 8

LORRY LOADING CHUTE
LIMIT SWITCHESREVISION: 3.
MINOR MODSORIGIN:
29/1/77 SGD. A.M.REVISION: 7
VALVE RIGHT POSITION
ROUTED TO ELEVATOR L1.
VALVE LEFT POSITION
ROUTED TO ELEVATOR L2.
29/4/93 K.M.REVISION: 2
REMOTE STOP POSITION
LAMP ADDED.ORIGIN:
27/1/77 SGD. A.M.REVISION: 6
LEFT & RIGHT LIMIT
REPOSITIONED.
DUE TO OBSERVATION OF
ACTUAL LIMITS
ORIGIN: 100
21/1/78 A.L.J.B.REVISION: 1
LEFT, RIGHT & STOPPED
LAMP ADDED.ORIGIN:
5/12/76 SGD. A.M.REVISION: 5
TRANS. TO SCP ROOM
L1 & R1 ADDED.
+ MINOR MODS.
ORIGIN: 100
24/4/77 A.L.J.B.REVISION: 4
GEN. MODSORIGIN: 100
28/3/77 A.L.J.B.REVISION: 1
DATE 14.10.76

CHECKED BY: [Signature]

APPROVED BY: [Signature]
DATE 5/12/76

ALL CONTROL TERMINALS PREFIXED 12M1

THE DESIGN AND MANUFACTURING
INFORMATION CONTAINED IN
THIS DRAWING IS THE EXCLUSIVE
RIGHT OF DEWHURST & PARTNER
LTD. AND MUST NOT BE COPIED
OR USED FOR MANUFACTURING
PURPOSES.

ISSUE 1 2 3 4 5 6 7 8

CTX361BT

CTX361BT