


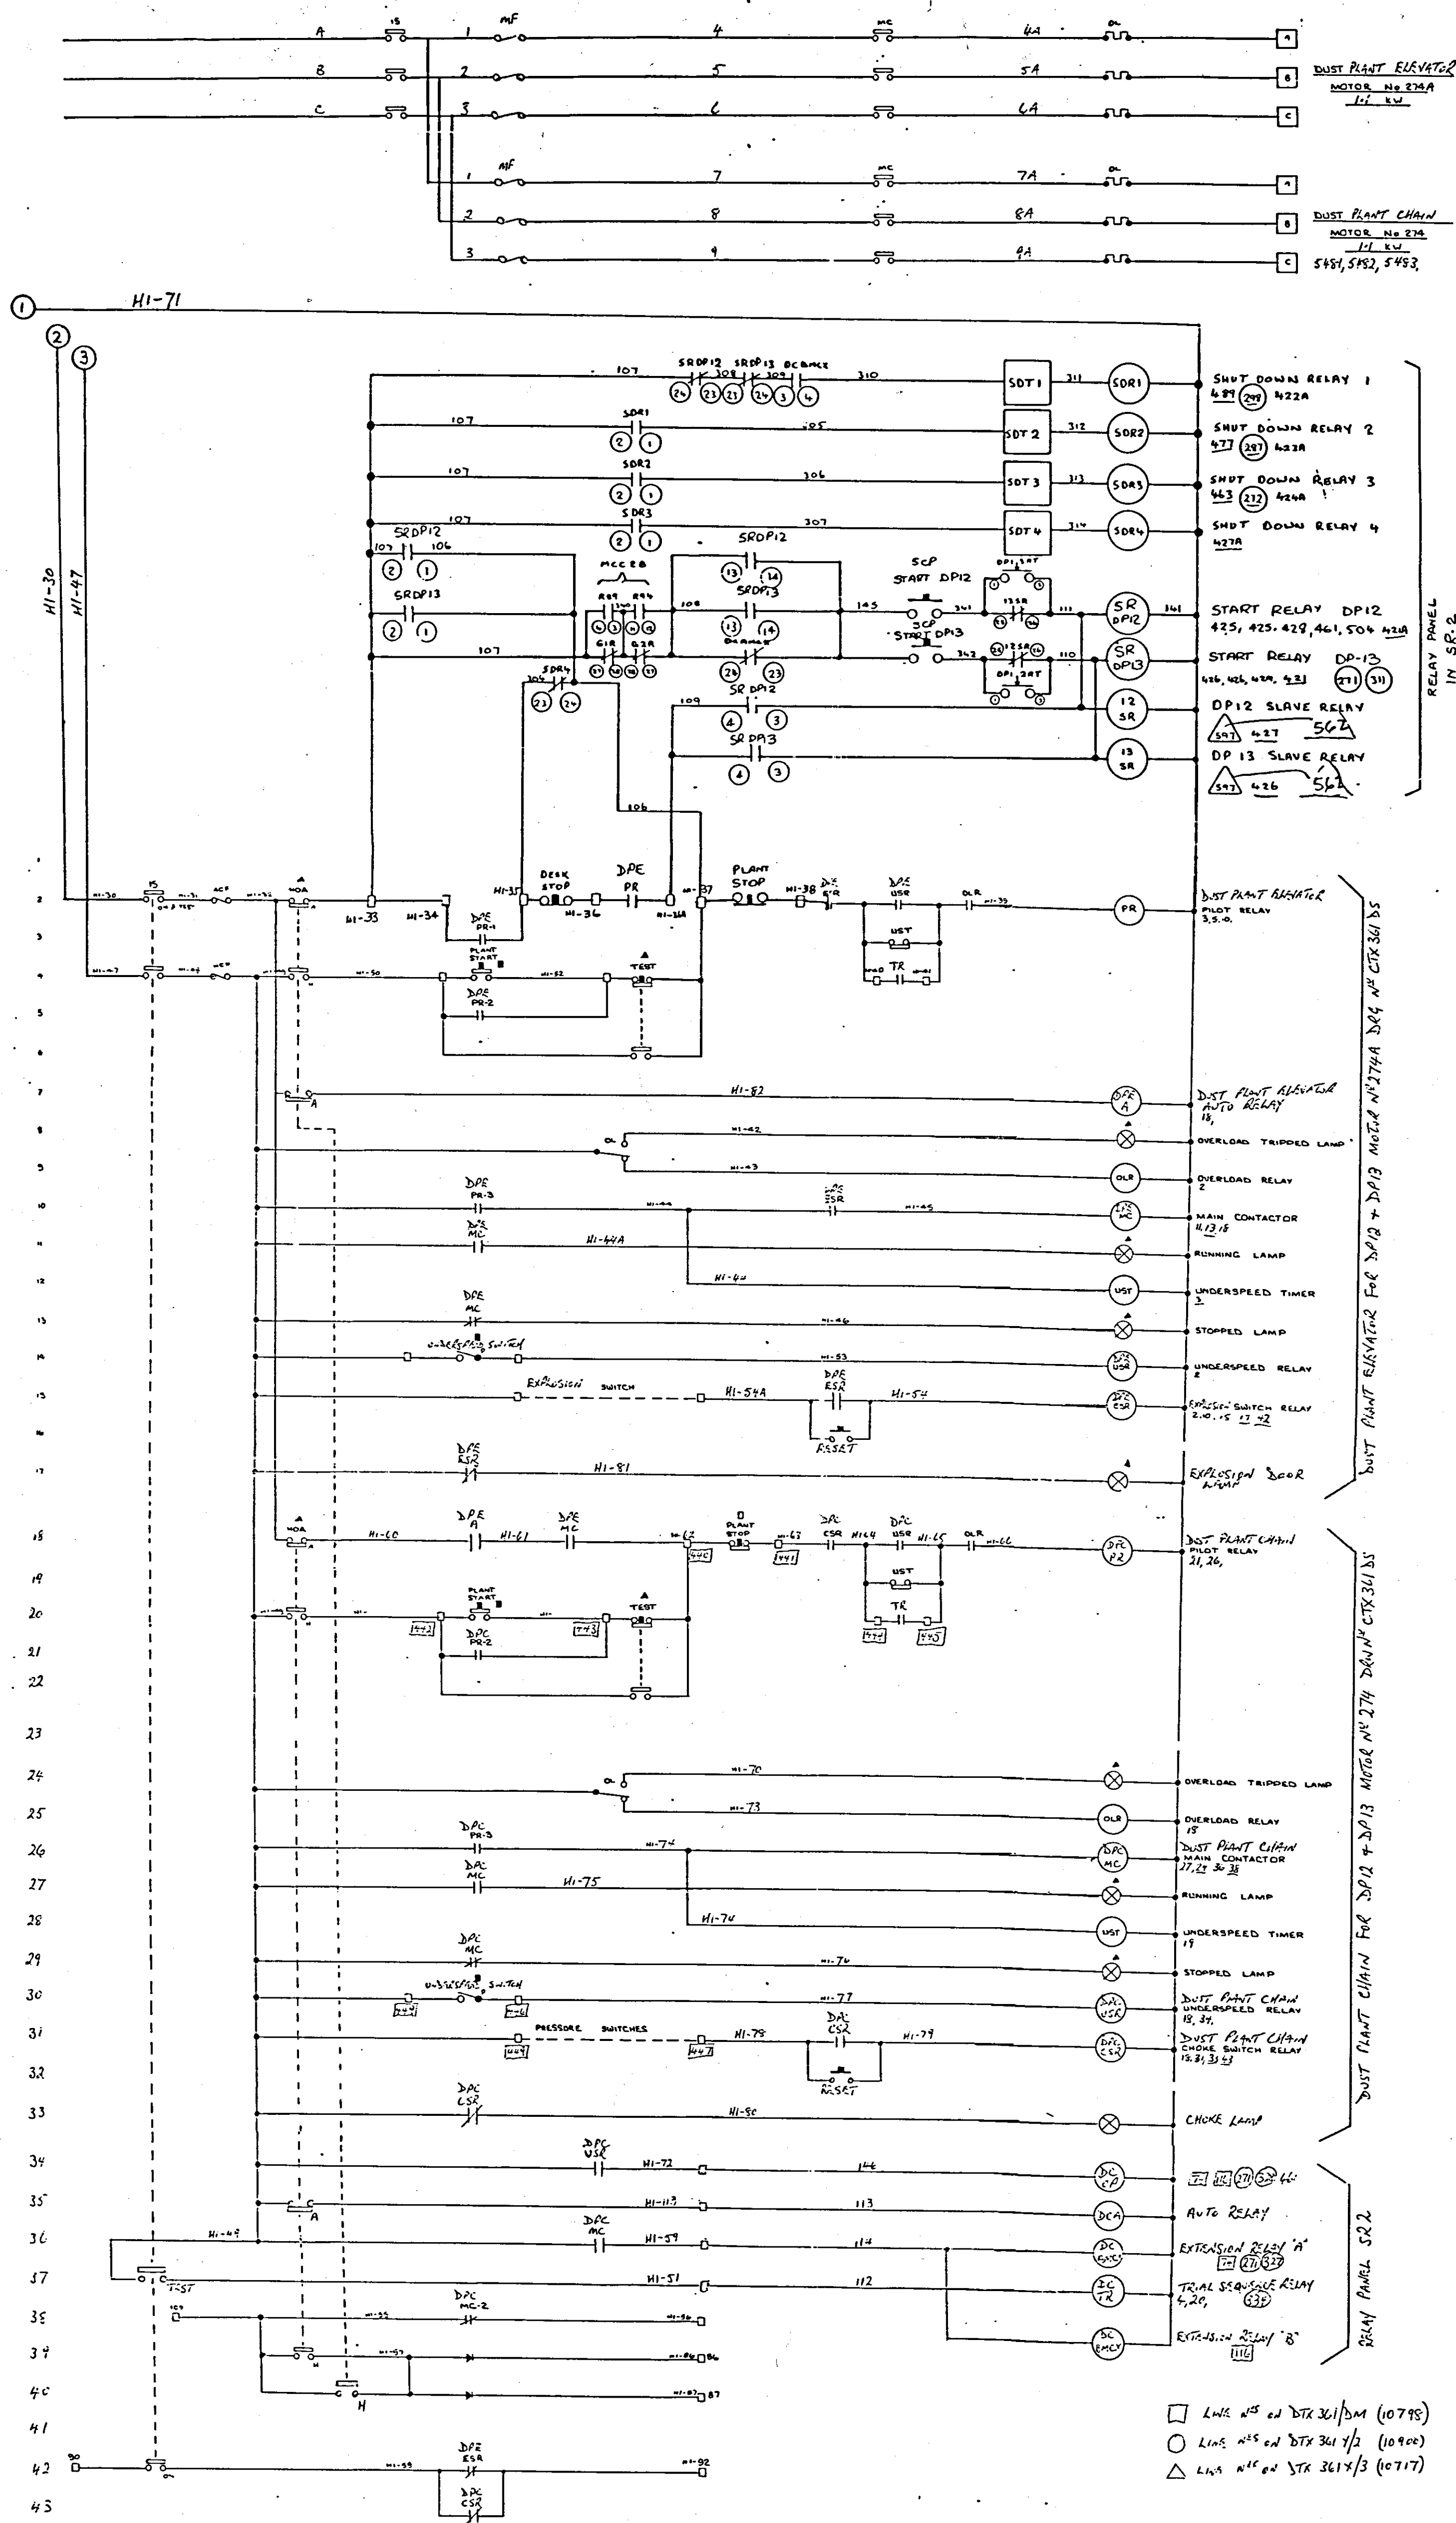

DEWHURST & PARTNER LTD.
MELBOURNE WORKS HOUNSLOW

TITLE: ELEVATOR + CHAIN CONVEYOR
SCHEMATIC FOR DUST PLANT 12 & 13
M.C.C. 22

REVISION: 4
M.C.C. 22
M.C.C. 22
M.C.C. 22
M.C.C. 22

REVISION: 3
M.C.C. 22
M.C.C. 22
M.C.C. 22
M.C.C. 22

REVISION: 2
M.C.C. 22
M.C.C. 22
M.C.C. 22
M.C.C. 22

REVISION: 1
M.C.C. 22
M.C.C. 22
M.C.C. 22
M.C.C. 22

CTX36IDS
CTX36IDS