


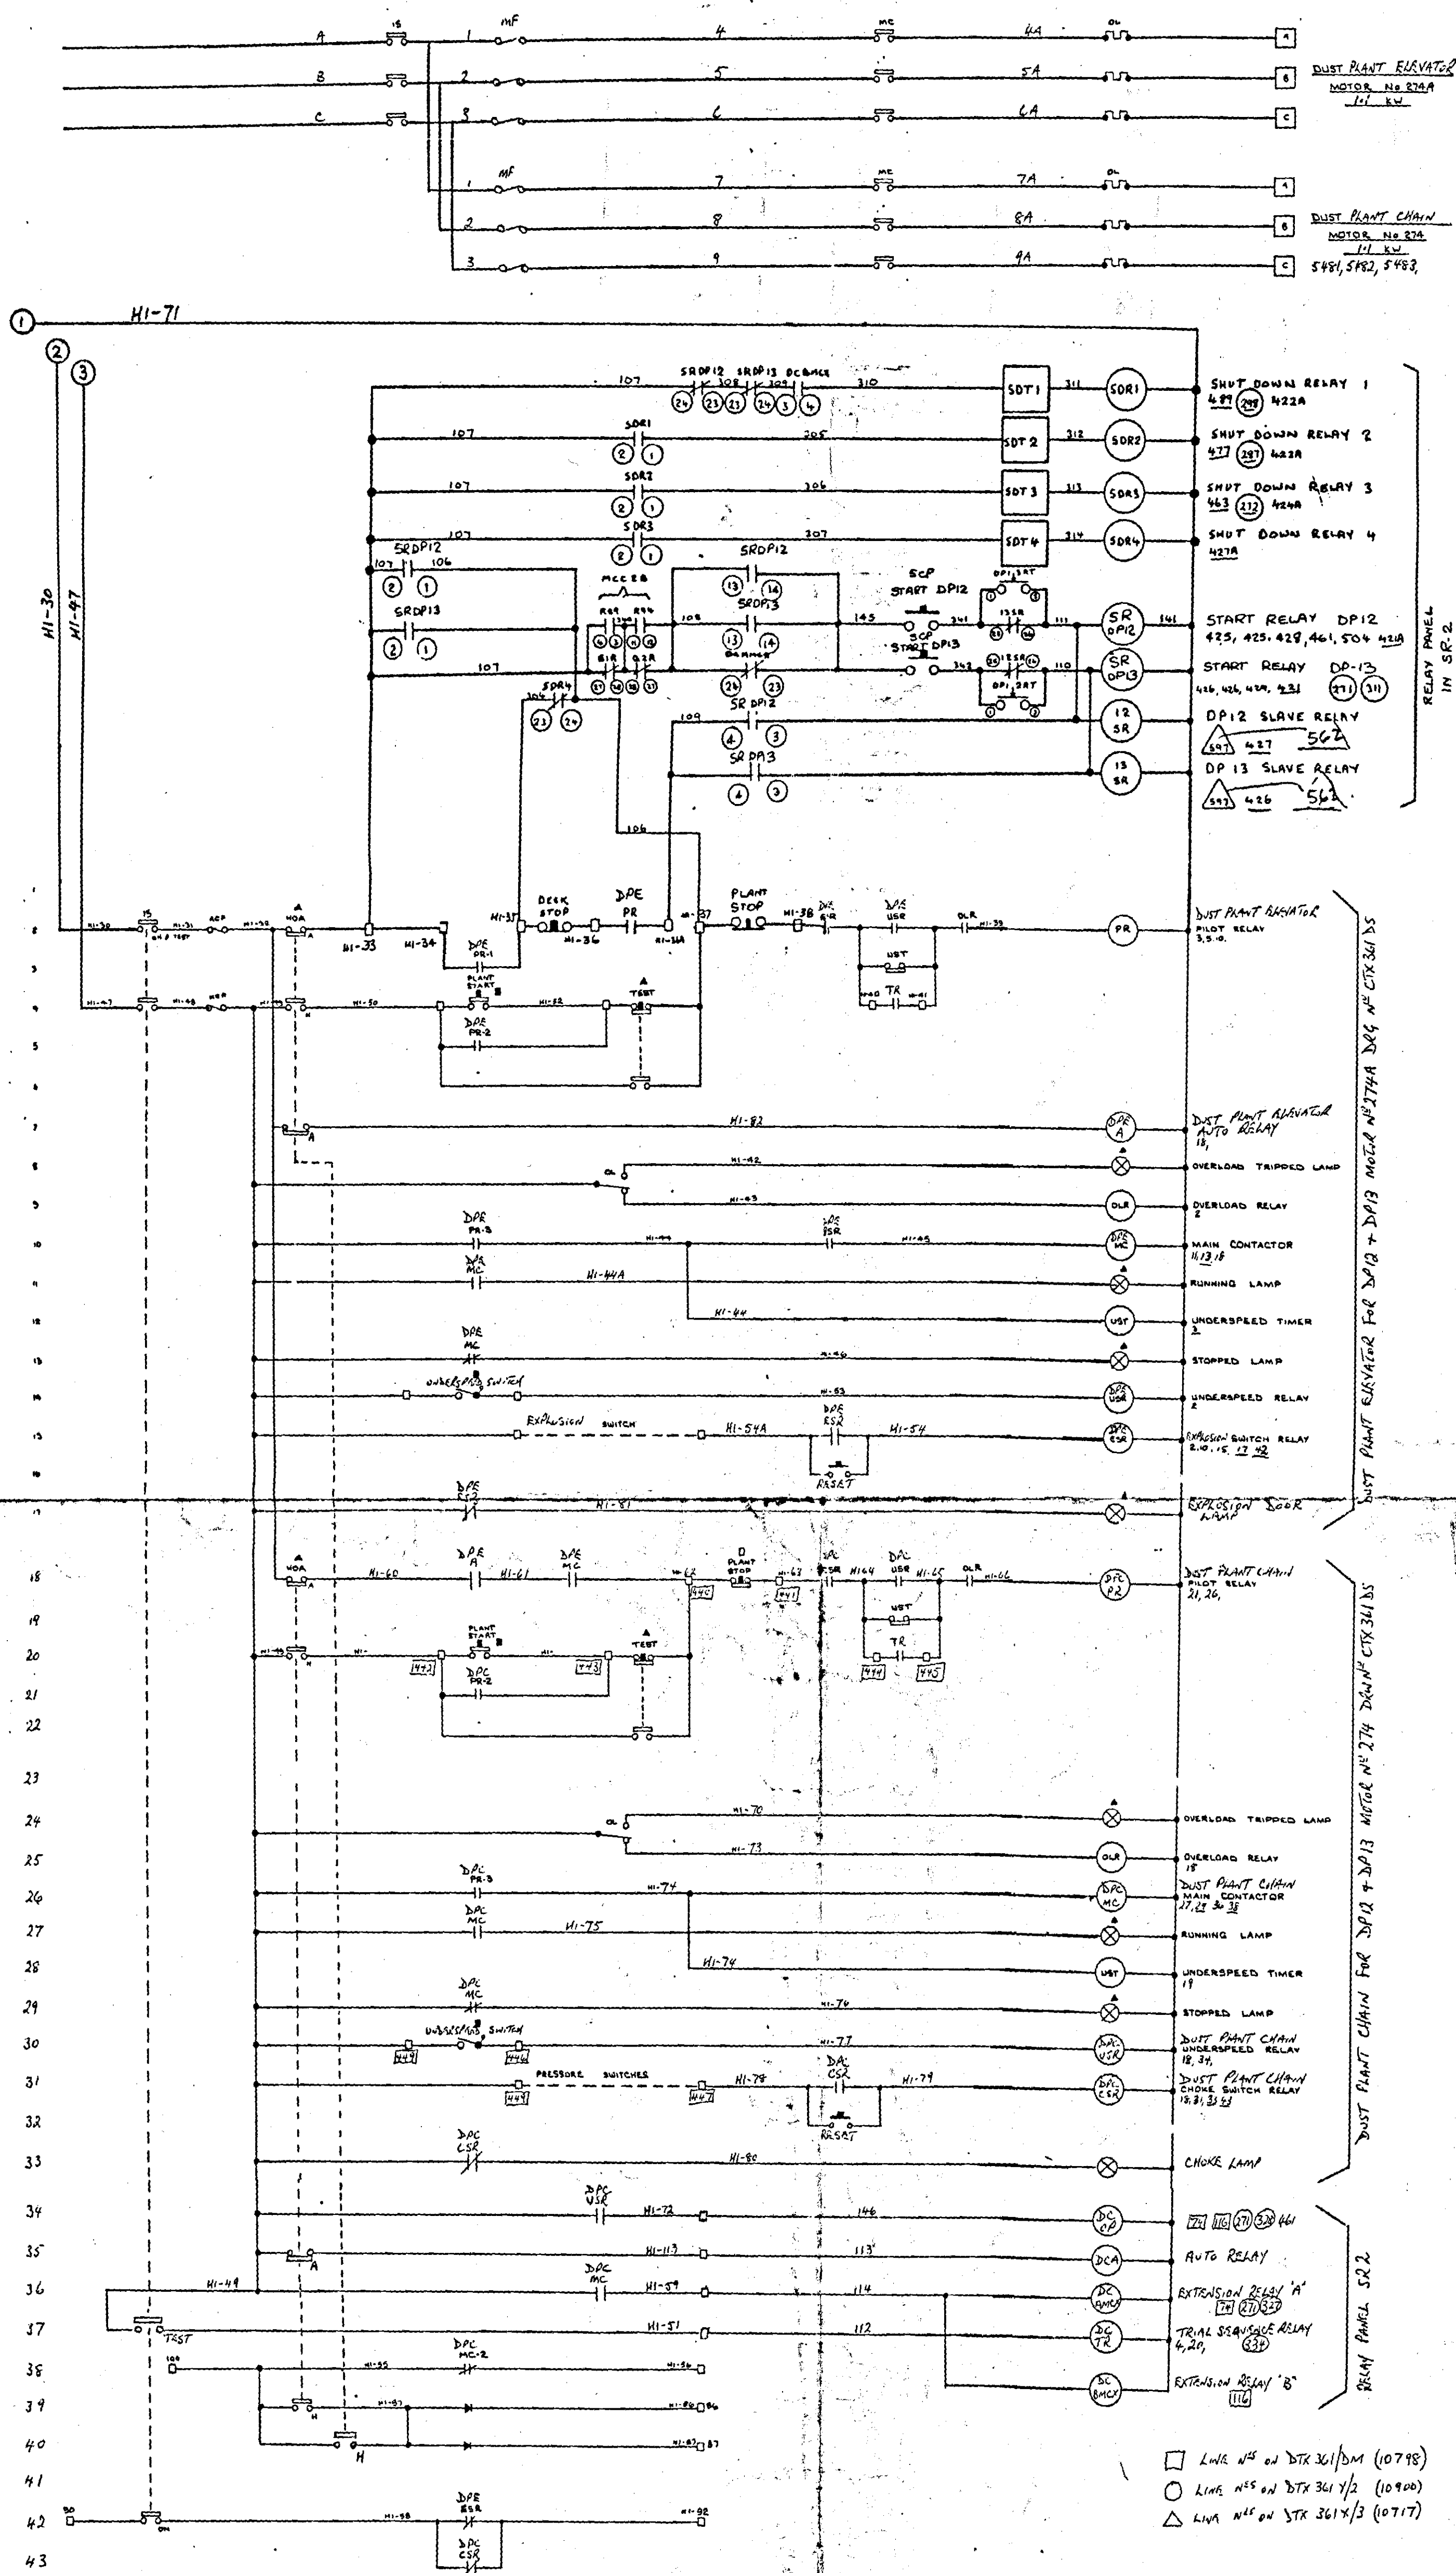

□ LAMP 111 on DTK 361/DM (10798)
 ○ LAMP 111 on DTK 361/2 (10900)
 △ LAMP 111 on DTK 361/3 (10717)

60

DEWHURST & PARTNER LTD.
 MELBOURNE WORKS HOUNSLOW

TITLE: ELEVATOR + CHAIN CONVEYOR
 SCHEMATIC FOR DUST PLANT 12 & 13

REVISION: 4
 BY: S.D. A. H. 15.8
 ORIGIN: 1.08
 DATE: 15.8

REVISION: 3
 BY: S.D. A. H. 15.8
 ORIGIN: 1.08
 DATE: 15.8

REVISION: 2
 BY: S.D. A. H. 15.8
 ORIGIN: 1.08
 DATE: 15.8

ISSUE	1	2	3	4	5	6
CTX36IDS						
CTX36IDS						

DUST PLANT ELEVATOR
 FOR DTK 361/DM
 INTERLOCK FROM
 HI-33 TO HI-37
 ADDS
 REVISION 5

THE DESIGN AND MANUFACTURING
 INFORMATION CONTAINED IN
 THIS DRAWING IS THE EXCLUSIVE
 RIGHT OF DEWHURST & PARTNER
 LTD. AND MUST NOT BE COPIED
 OR USED FOR MANUFACTURING
 PURPOSES.

DRAWN BY: A.H.
 DATE: 15.8
 CHECKED BY: S.D. A. H.
 APPROVED BY: S.D. A. H.
 DATE: 15.8

KEY DIAG NO.
 EXT. DIAG. NO.
 REL. DIAG. NO.
 PANEL LAYOUT NO.