
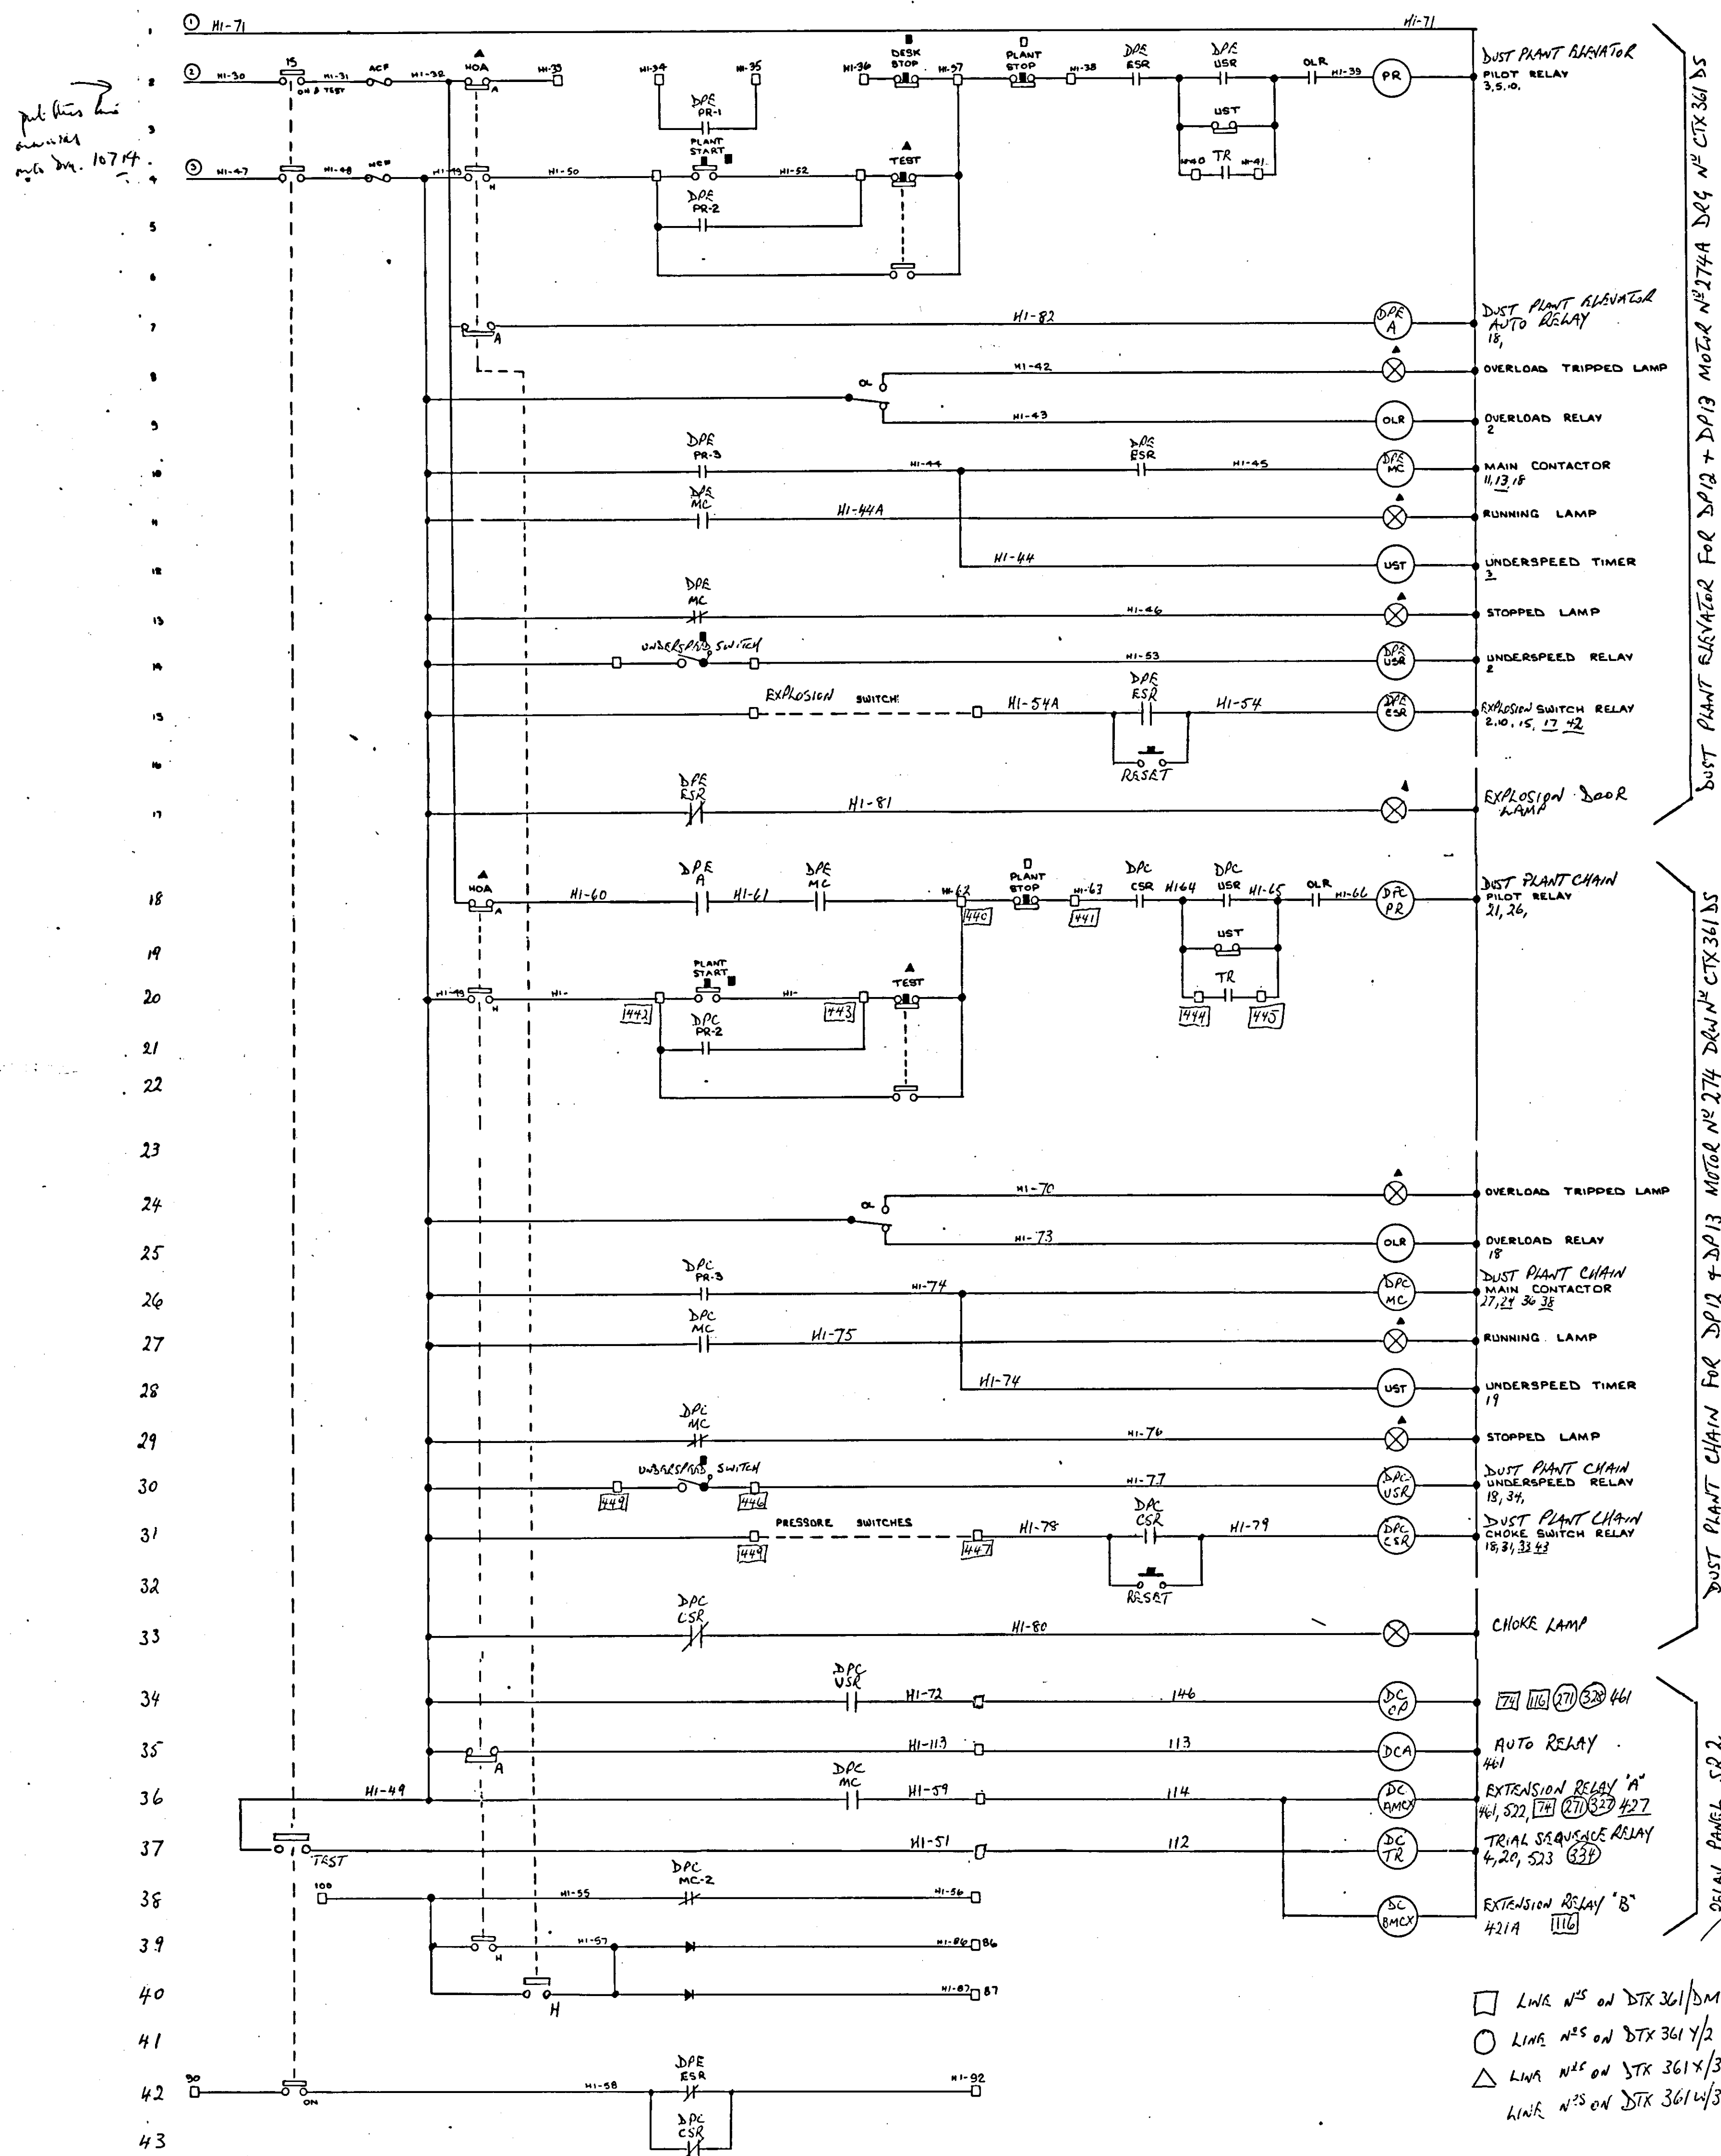


10854

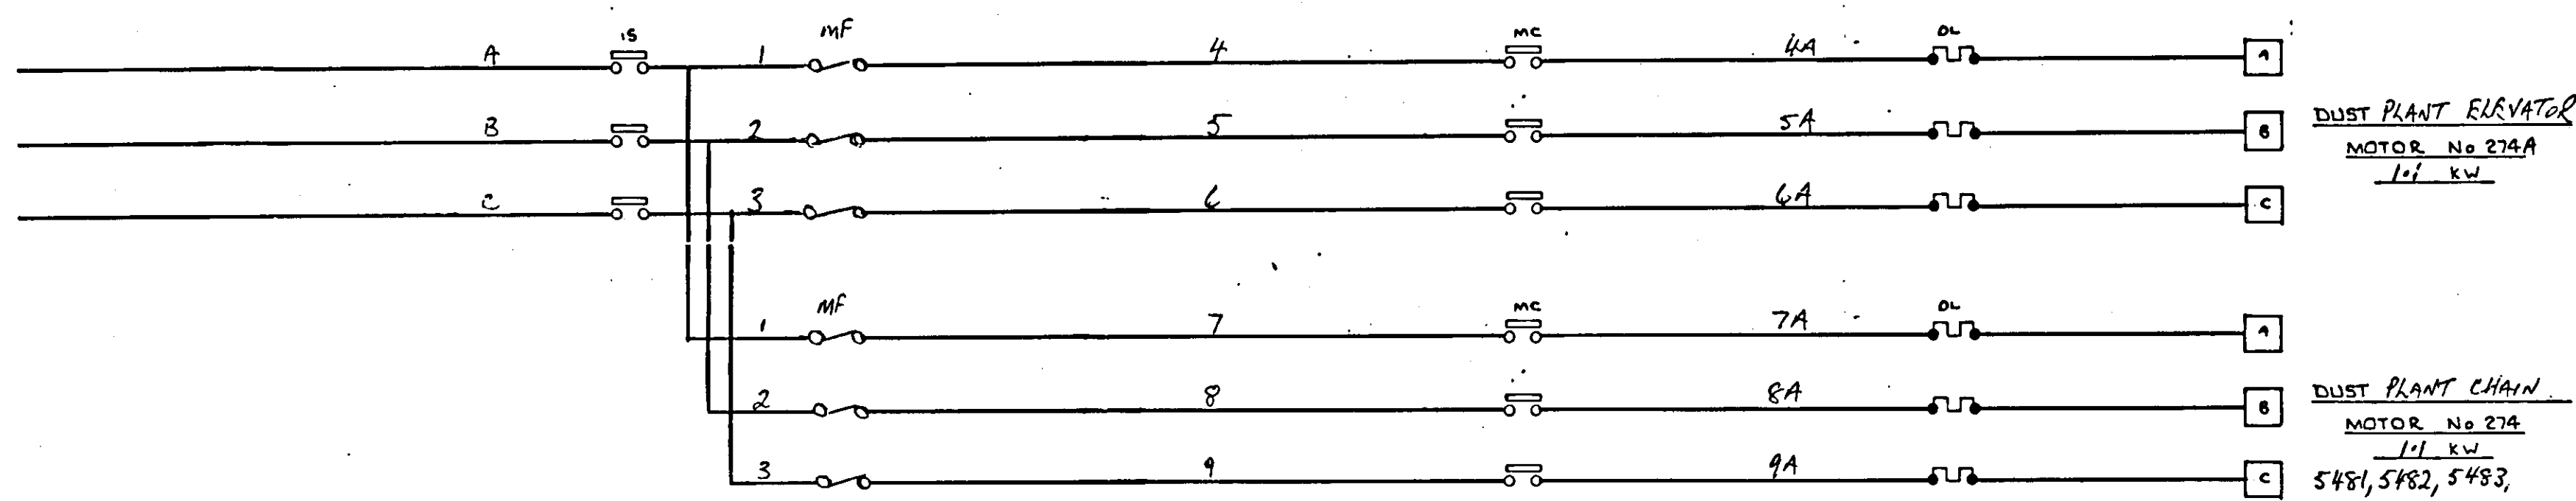

REVISED

DEWHURST & PARTNER LTD.

MELBOURNE WORKS

HOUNSLOW

TITLE: ELEVATOR + CHAIN CONVEYOR
SCHEMATIC FOR DUST PLANT 12 & 13

REVISION: 5. MUST PLANT ELEV. FOR DP12 & 13 ADDED INTERLOCK FROM H1-33 TO H1-37 ADDED. 1-10-74 EB	REVISION: 4 KW RATING ADDED TO MOTOR NO. 274 ORIGIN: 1 CD 24/5/77 SGD. A. J. J.
---	---

REVISION : 3
MOTOR HEATER
ADDED.

ORIGIN :
274 / 77 SGD.T.R

REVISION : 2.
DUST SCREW CONVEYOR
REMOVED.
ORIGIN :
29/3/77 SGD. A.M.

DRAWN BY	A.M.
DATE	
CHECKED BY	
APPROVED BY	
DATE	

THE DESIGN AND MANUFACTURING
INFORMATION CONTAINED IN
THIS DRAWING IS THE EXCLUSIVE
RIGHT OF DEWHURST & PARTNER
LTD. AND MUST NOT BE COPIED
OR USED FOR MANUFACTURING
PURPOSES.

ISSUE	1	2	3	4	5	6					
-------	---	---	---	---	---	---	--	--	--	--	--

CTX36IDS

CTX36IDS

10854