


10898.

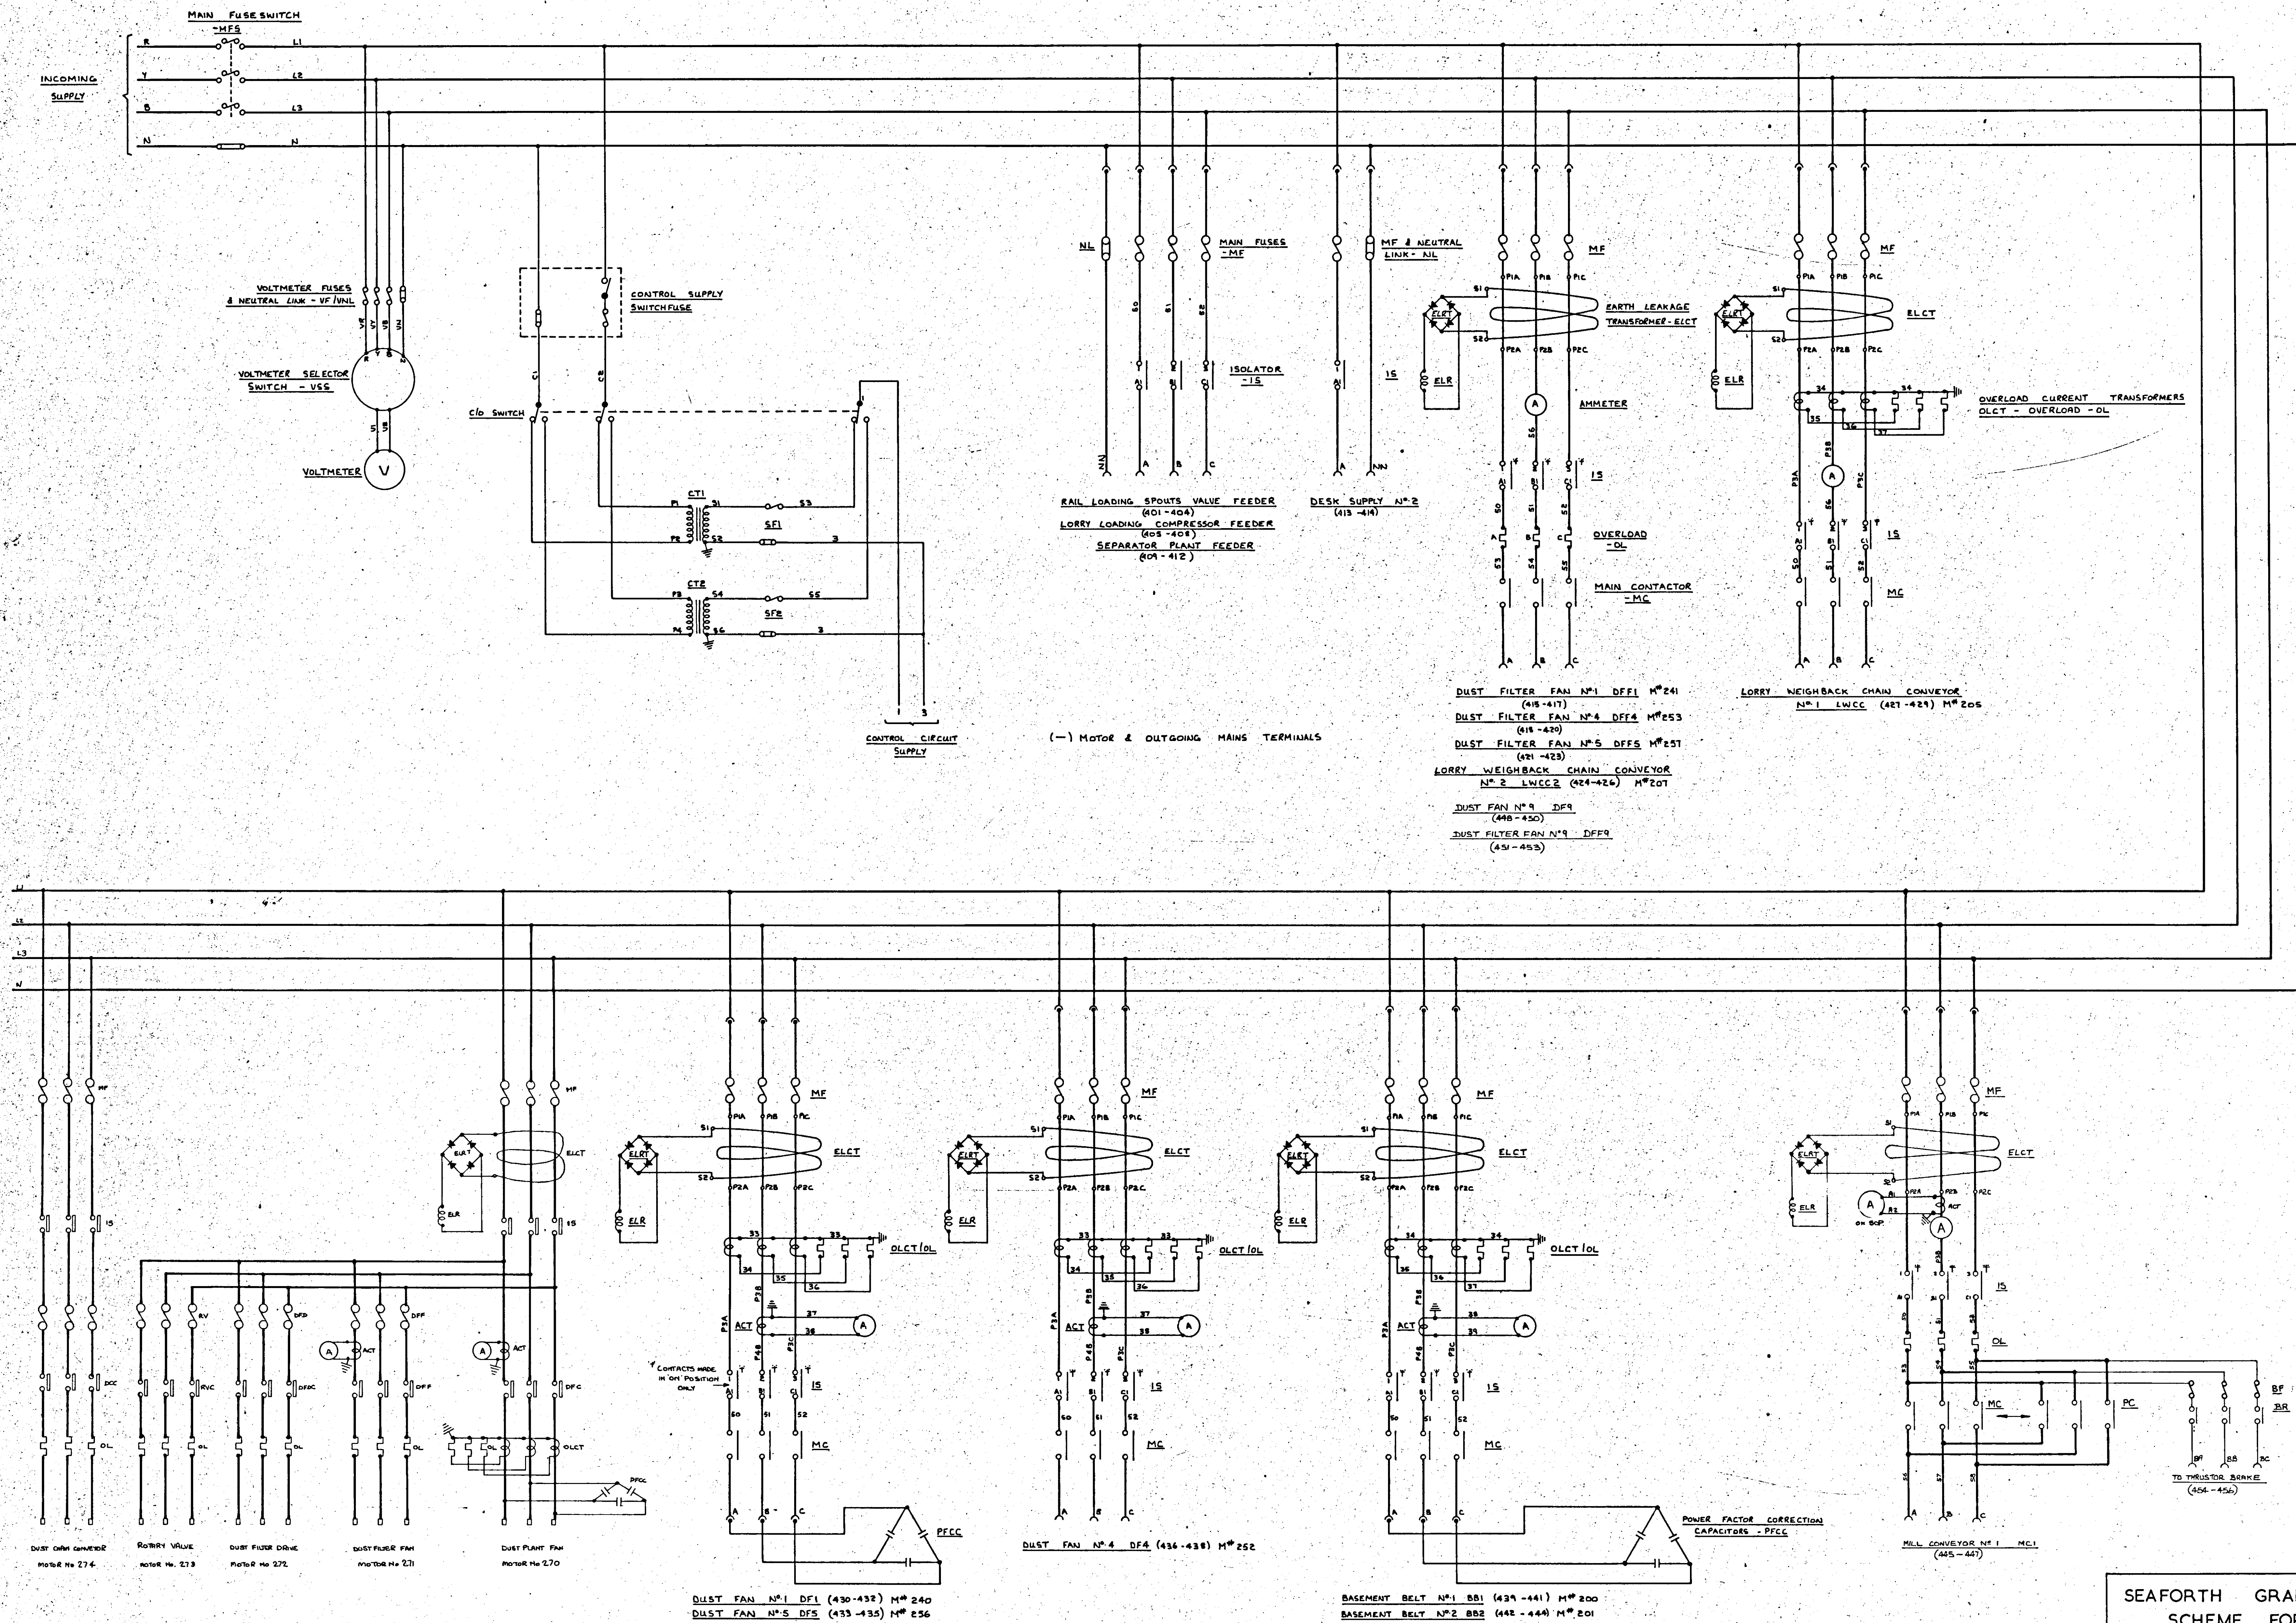

10898.

DEWHURST & PARTNER LTD.
MELBOURNE WORKS HOUNSLOW

SCHEME FOR PANEL MCC2A - SEAFORTH GRAIN TERMINAL

REVISION: 5
DUST PLANT 12
REVISION: 4
BF ADDED
REVISION: 3
ARMATURE ON BCP RATED
TO RAIL DIVISION 14.1
REVISION: 2
DFF, DFF 8 & MC1
12226.2
REVISION: 1
12226.2
DATE 2-12-70
CHECKED BY
APPROVED BY
DATE

SEAFORTH GRAIN TERMINAL -
SCHEME FOR PANEL MCC2A

THE DESIGN AND MANUFACTURING
INFORMATION CONTAINED IN
THIS DRAWING IS THE EXCLUSIVE
RIGHT OF DEWHURST & PARTNER
LTD. AND MUST NOT BE COPIED
OR USED FOR MANUFACTURING
PURPOSES.

ISSUE 1 2 3 4 5 6

DTX361W/4

DTX361W/4