10898.

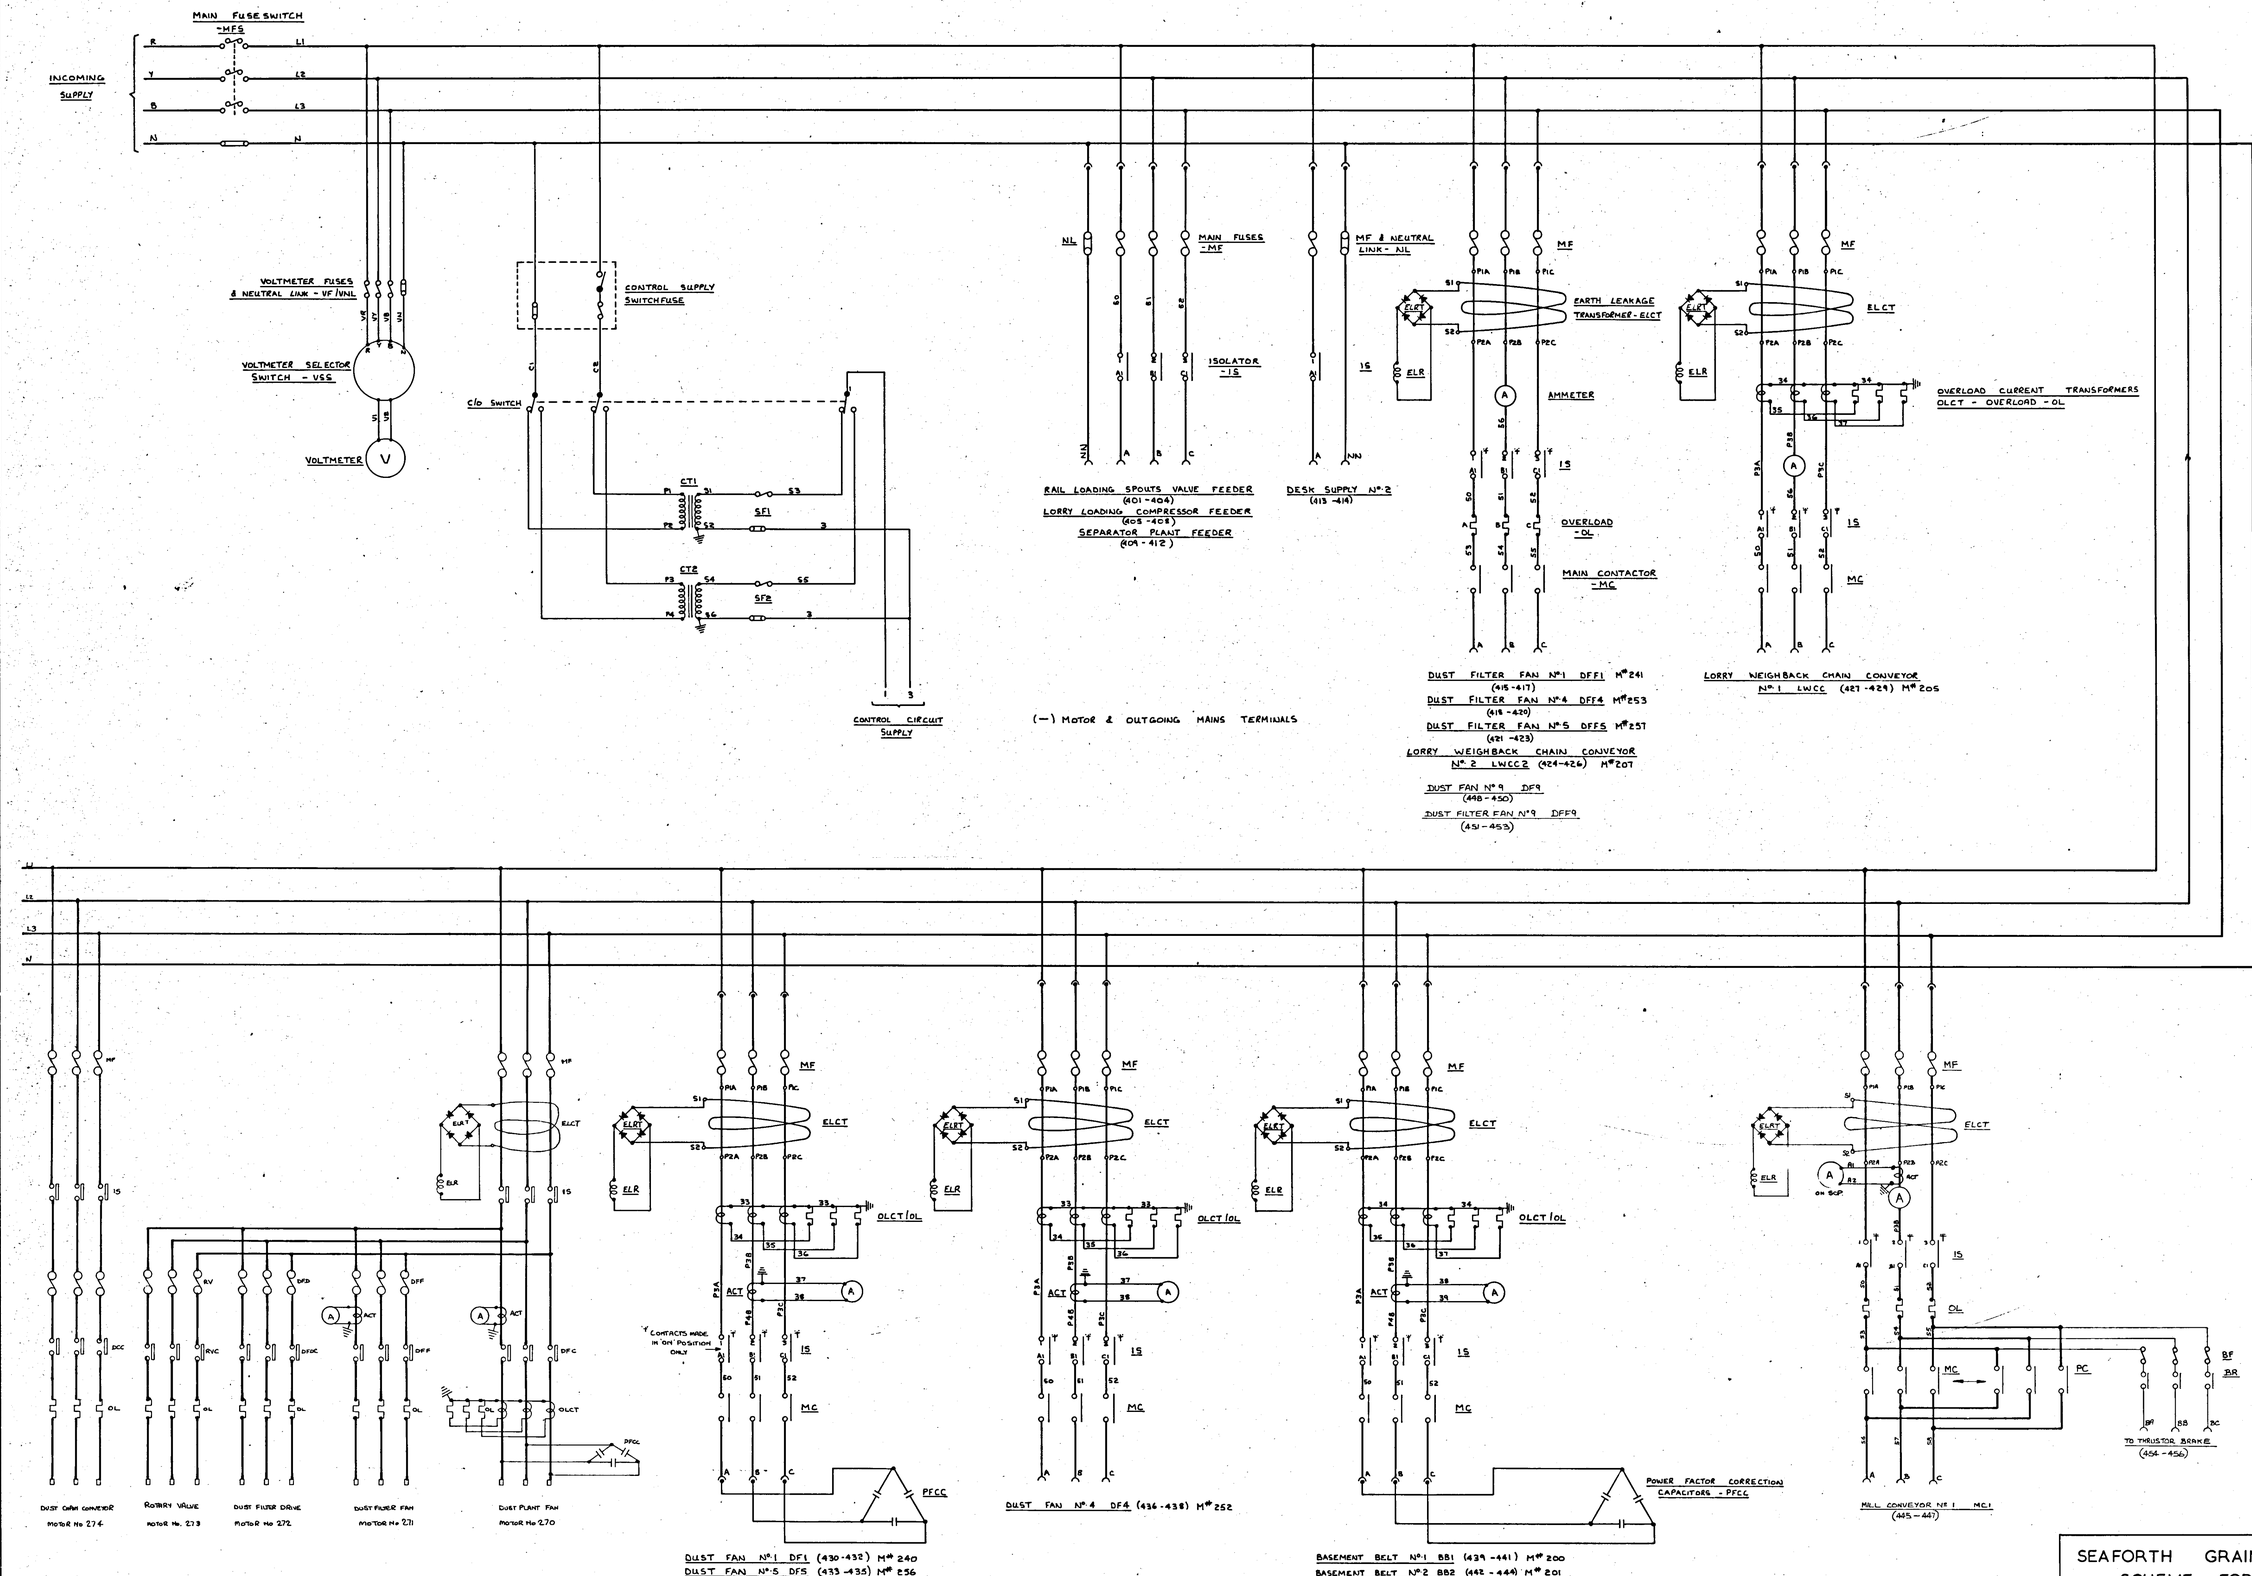

10898.

SEAFORTH GRAIN TERMINAL — SCHEME FOR PANEL MCC 2 A

THE DESIGN AND MANUFACTURING INFORMATION CONTAINED IN THIS DRAWING IS THE EXCLUSIVE RIGHT OF DEWHURST & PARTNER LTD. AND MUST NOT BE COPIED OR USED FOR MANUFACTURING PURPOSES.

ISSUE 1 2 3 4 5 6

DTX361W/4

DEWHURST & PARTNER LTD.
MELBOURNE WORKS HOUNSLOW

TITLE: SCHEME FOR PANEL MCC 2A - SEAFORTH GRAIN TERMINAL

REVISION: 5	REVISION: 4	REVISION: 3	REVISION: 2	REVISION: 1	
DUST PLANT 12 ADDED. PAGE No. WAS 12	BF ADDED.	AMMETER ON SCP ADDED TO MILL CONVEYOR No. 1.	DF9, DFF9 & MC1 ADDED.	ISOLATOR NOTE ADDED.	DRAWN BY :- J.S.
ORIGIN: 15/4/77 SGD.	ORIGIN: ICD. 27/6/72 SGD JS.	ORIGIN: ICD. 20/3/73 SGD JS.	ORIGIN: ICD 15/6/72 SGD	ORIGIN: CUST 7/1/71 SGD	DATE 2-12-70
					CHECKED BY
					APPROVED BY
					DATE

KEY DIAG. No. —
EXT. DIAG No.
REL. DIAG No.
PANEL LAYOUT No. HTX361W

DTX361W/4