10898.

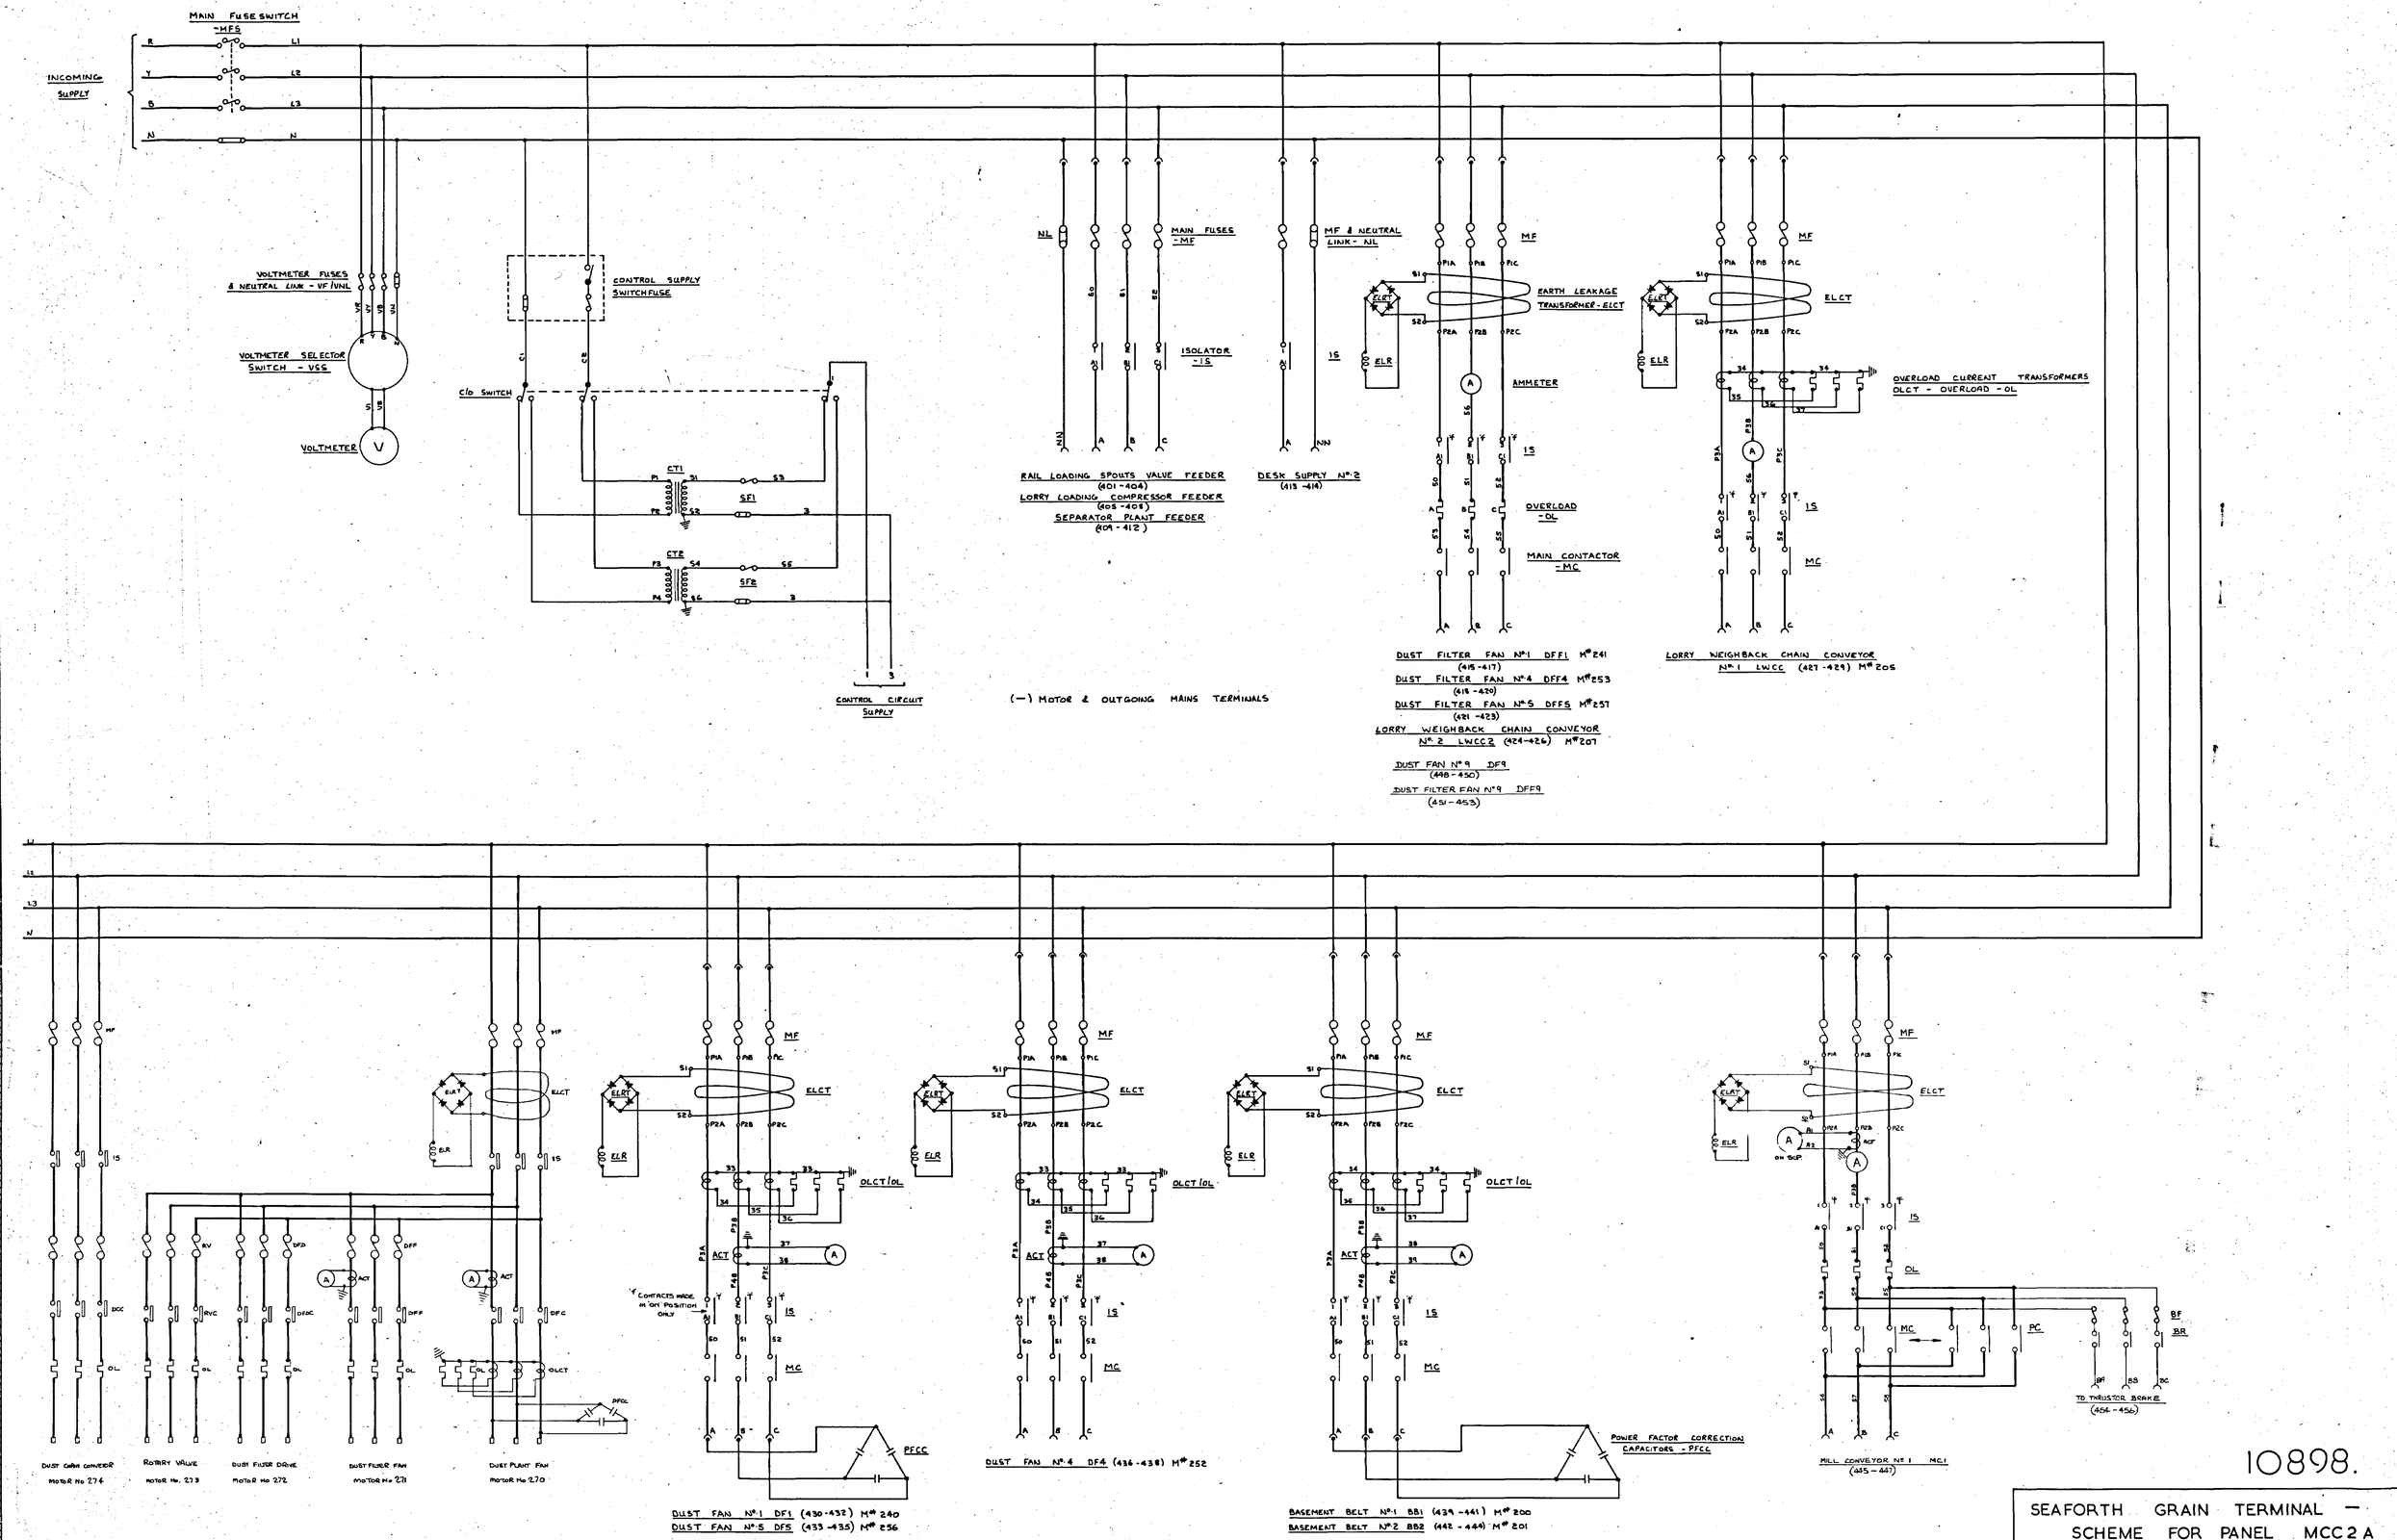

10898.

DEWHURST & PARTNER LTD. MELBOURNE WORKS HOUNSLOW	TITLE: SCHEME FOR PANEL MCC 2A - SEAFORTH GRAIN TERMINAL
REVISION: 5 DUST PLANT 12 ADDED. PAGE No WAS 12. ORIGIN: 15/4/73 SGD.	REVISION: 4 BF ADDED. ORIGIN: ICD. 21/6/72 SGD.
REVISION: 3 AMMETER ON SCP ADDED. TO MILL CONVEYOR No.1. ORIGIN: ICD. 20/3/73 SGD.	REVISION: 2 DF9, DFF9 & MC1 ADDED. ORIGIN: ICD 15/6/72 SGD.
REVISION: 1 (ERRATUM NOTE A3343) ORIGIN. COST 7/11/71 SGD.	DRAWN BY :- J.S. DATE 2-12-70 CHECKED BY APPROVED BY DATE

SEAFORTH GRAIN TERMINAL — SCHEME FOR PANEL MCC 2A

THE DESIGN AND MANUFACTURING INFORMATION CONTAINED IN THIS DRAWING IS THE EXCLUSIVE RIGHT OF DEWHURST & PARTNER LTD. AND MUST NOT BE COPIED OR USED FOR MANUFACTURING PURPOSES.

ISSUE 1 2 3 4 5 6

KEY DIAG. No. —

EXT. DIAG No.

REL. DIAG No.

PANEL LAYOUT No. MTX361W

DTX361W/4 (1 OF 4)

DTX361W/4