


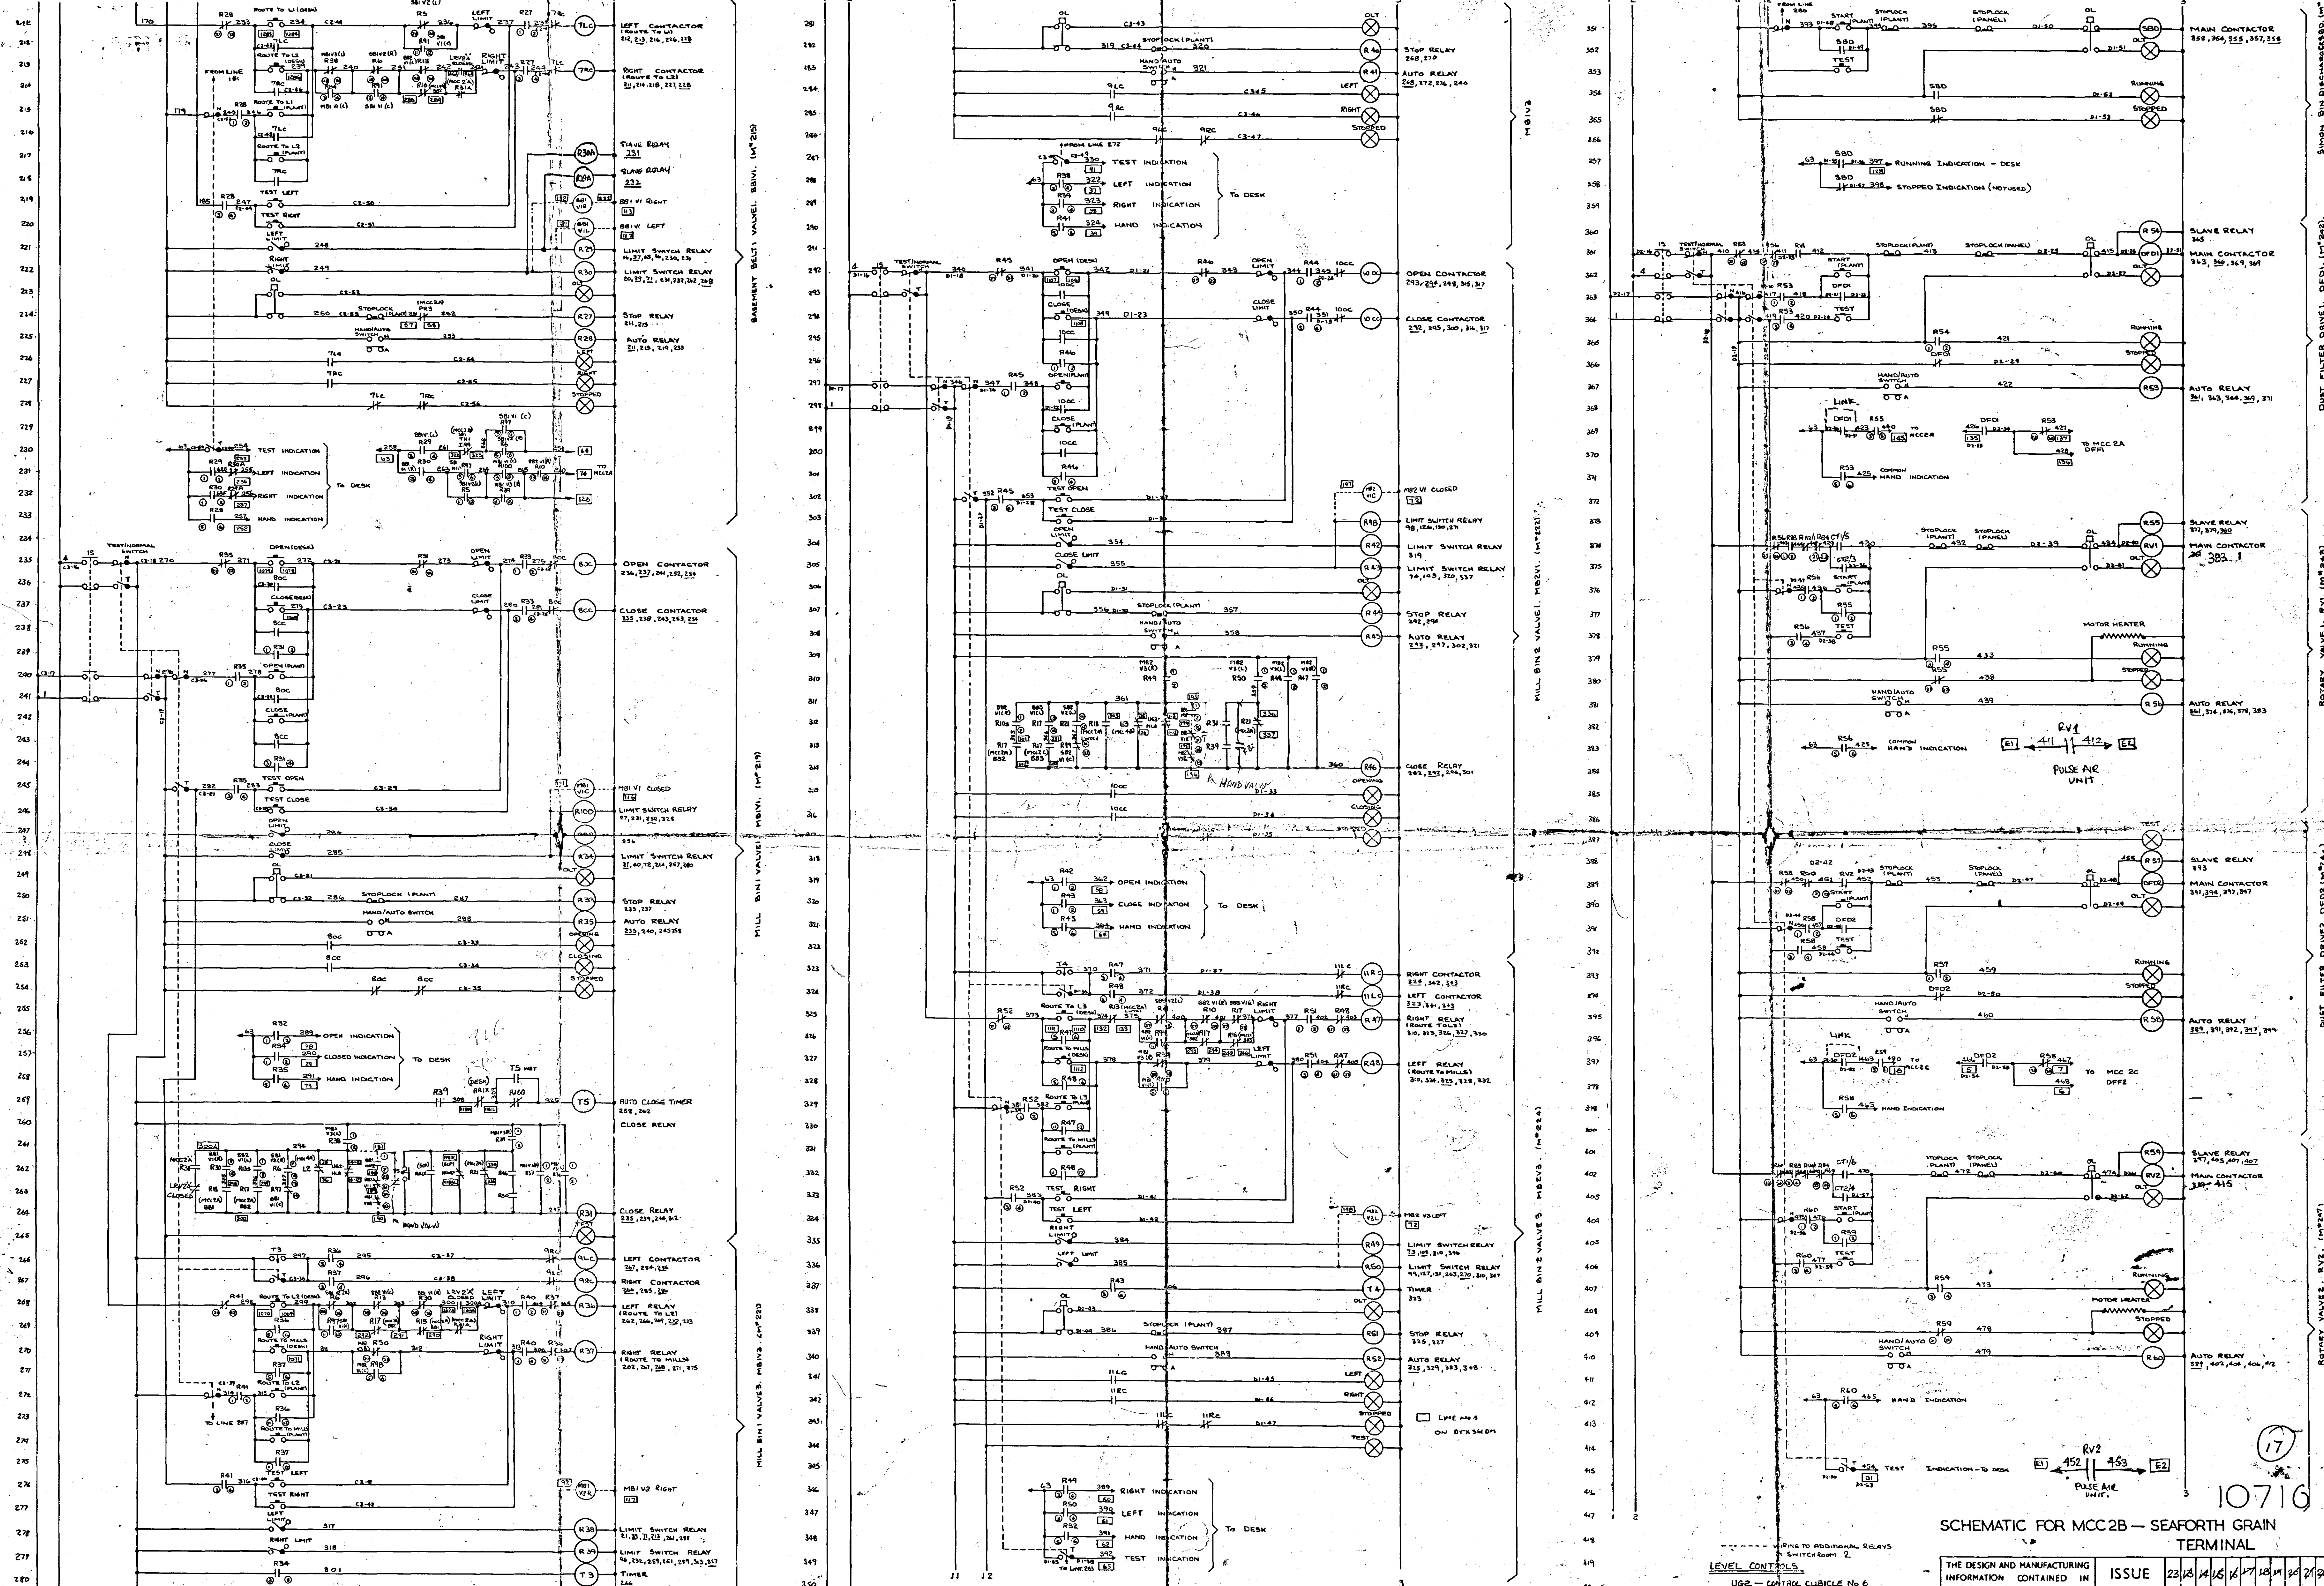

SCHEMATIC FOR MCC2B — SEAFORTH GRAIN  
TERMINAL

|   |            |    |    |    |    |   |   |    |    |    |    |    |  |
|---|------------|----|----|----|----|---|---|----|----|----|----|----|--|
| THE DESIGN AND MANUFACTURING INFORMATION CONTAINED IN THIS DRAWING IS THE EXCLUSIVE RIGHT OF DEWHURST & PARTNER LTD AND MUST NOT BE COPIED OR USED FOR MANUFACTURING PURPOSES<br><br>KEY DIAG No.<br>EXT. DIAG No. STX 36IX<br>REL. DIAG No.<br>PANEL LAYOUT No. HTY33WIX | ISSUE      | 23 | 18 | 14 | 10 | 7 | 3 | 19 | 11 | 04 | 27 | 20 |  |
|   | DTX 36IX/2 |    |    |    |    |   |   |    |    |    |    |    |  |
|   | DTX 36IX/2 |    |    |    |    |   |   |    |    |    |    |    |  |
|   |            |    |    |    |    |   |   |    |    |    |    |    |  |
|   |            |    |    |    |    |   |   |    |    |    |    |    |  |
|   |            |    |    |    |    |   |   |    |    |    |    |    |  |