


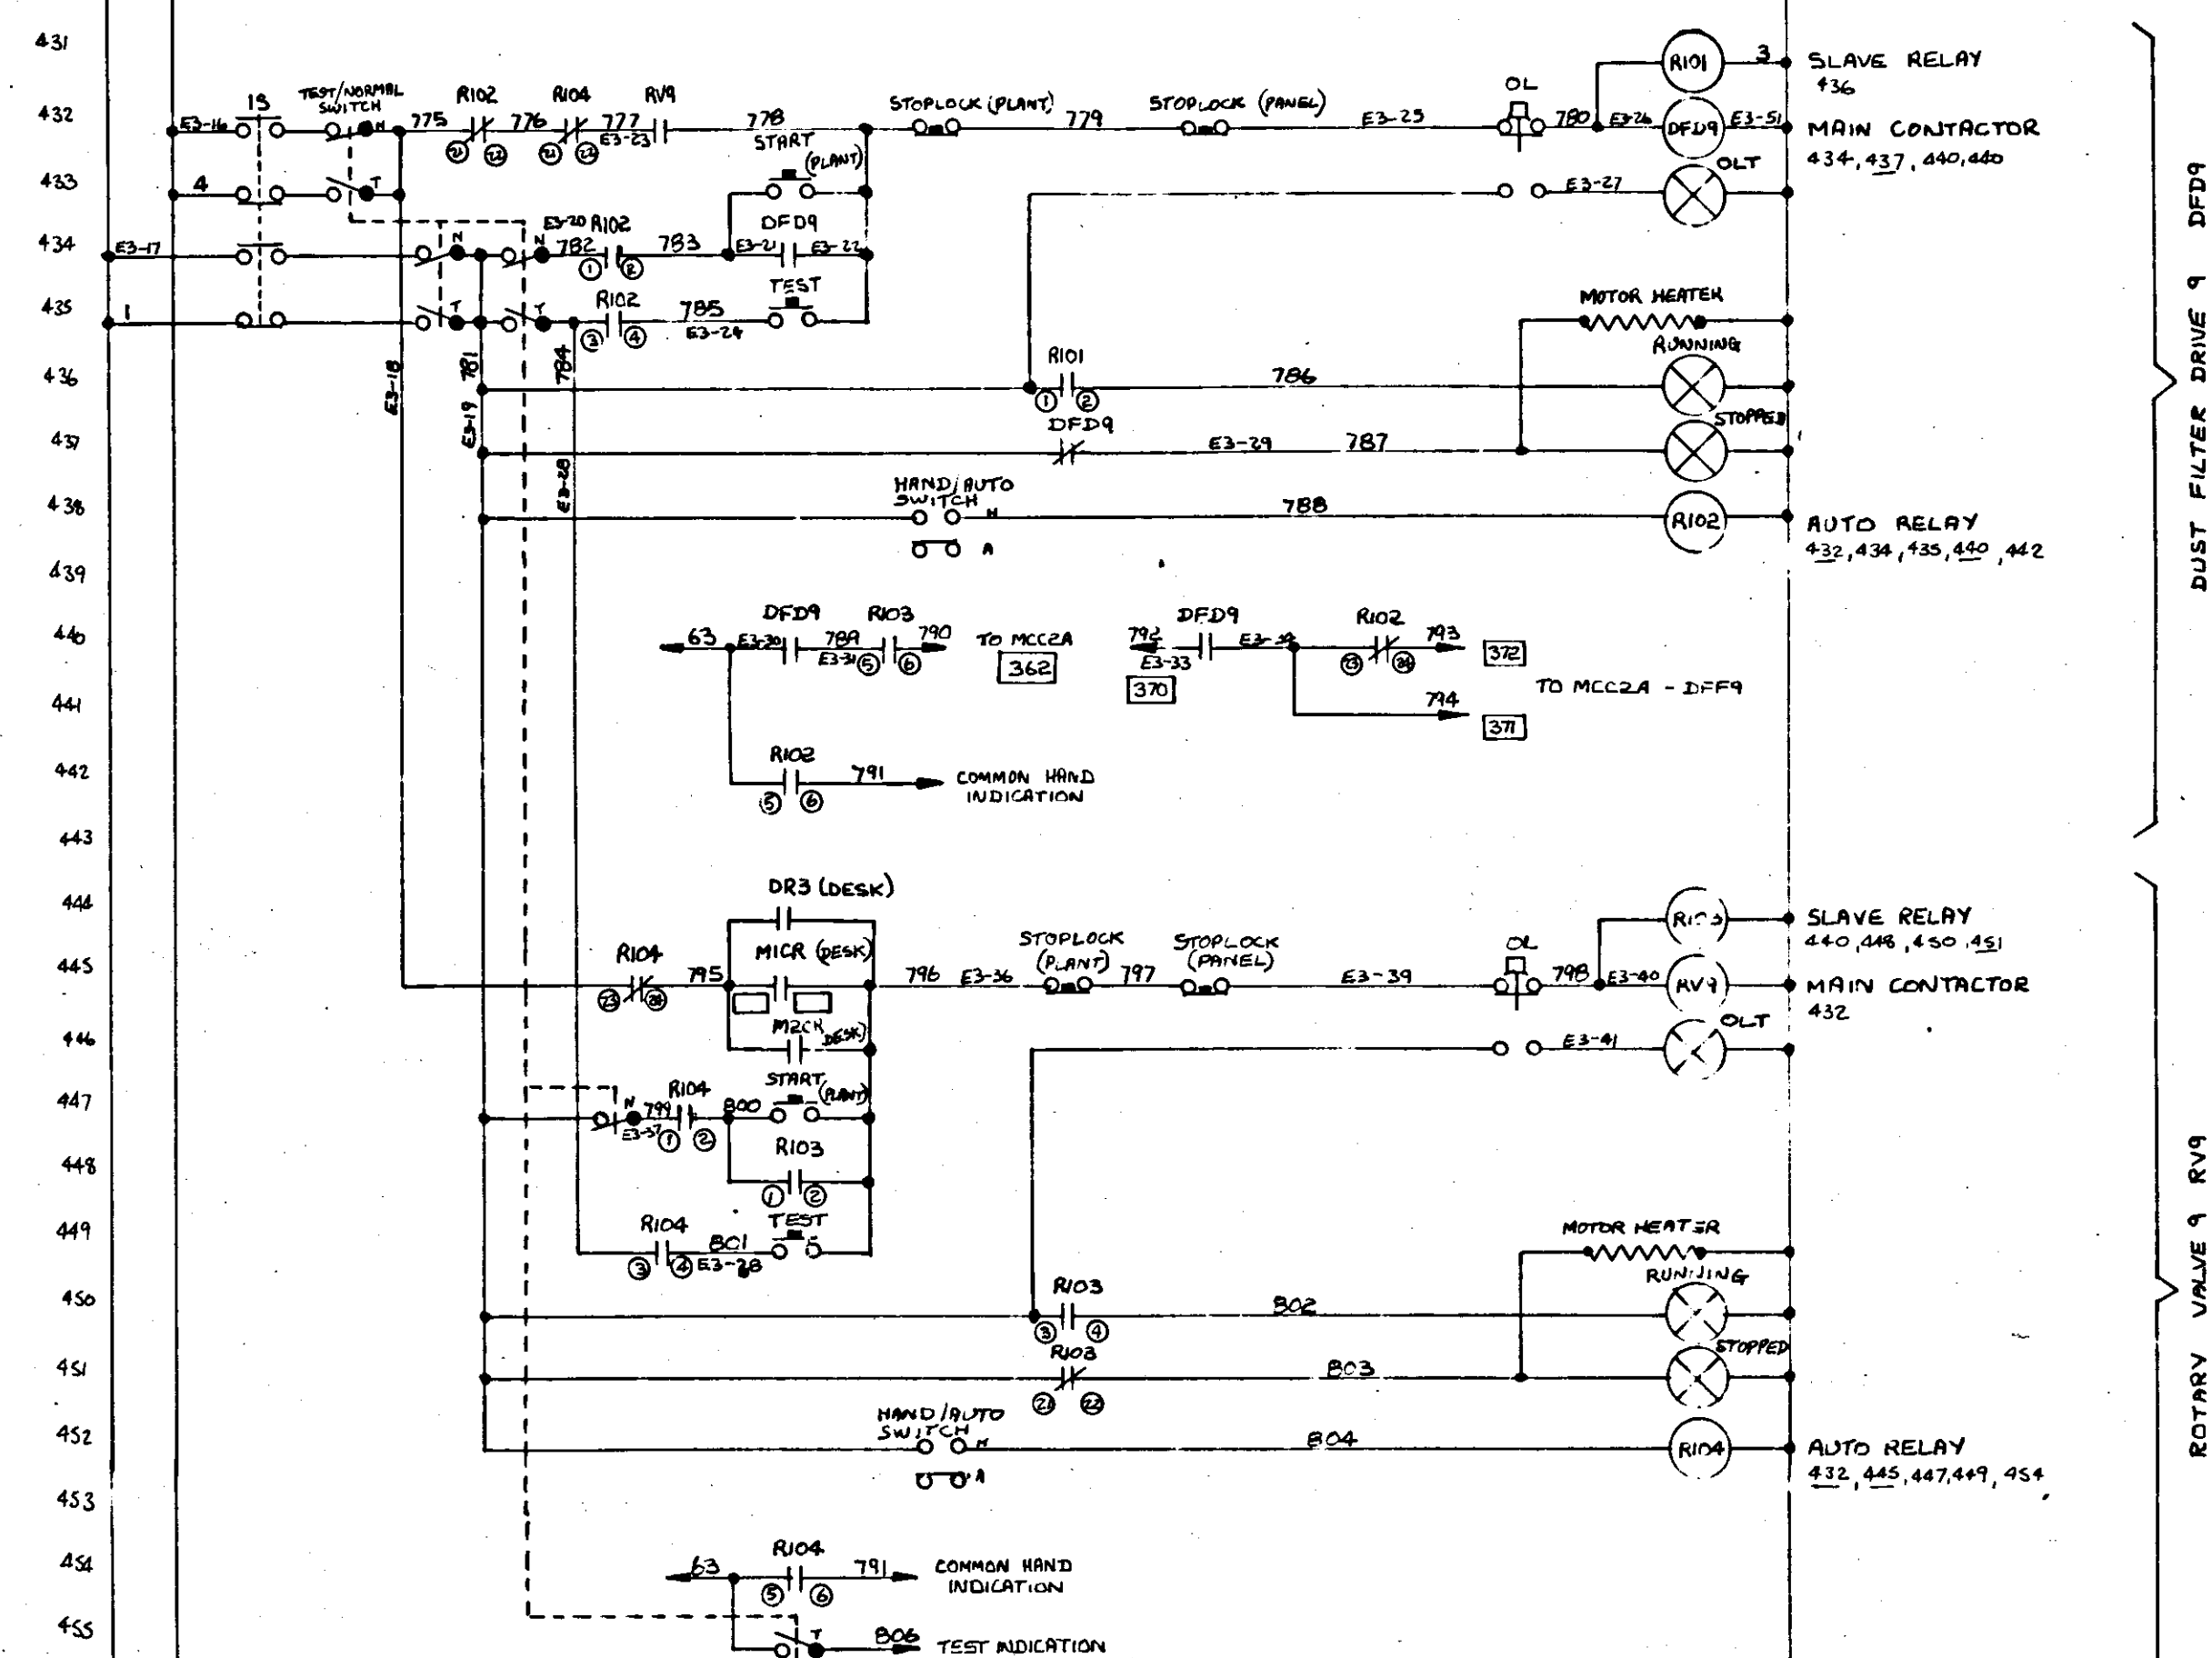

DEWHURST & PARTNER LTD.
MELBOURNE WORKS HOUNSLOW

TITLE
SCHEMATIC DIAGRAM FOR MCC2B — SEAFORTH GRAIN TERMINAL

REVISION:	REVISION:	REVISION: 2	REVISION:	REVISION: 1	DRAWN BY
ORIGIN:	ORIGIN:	ORIGIN: ICP	ORIGIN:	ORIGIN: ICD	DATE
1 / 1 SGD	1 / 1 SGD	3 / 5 177SGD JS	1 / 1 SGD	1 / 1 173SGD JS	5-7-72

KEY DIAG. No.	EXT. DIAG. No.
REL. DIAG. No.	PANEL LAYOUT No.
DATE	

SCHEMATIC DIAGRAM FOR MCC2B —
SEAFORTH GRAIN TERMINAL

THE DESIGN AND MANUFACTURING
INFORMATION CONTAINED IN
THIS DRAWING IS THE EXCLUSIVE
RIGHT OF DEWHURST & PARTNER
LTD. AND MUST NOT BE COPIED
OR USED FOR MANUFACTURING
PURPOSES.

ISSUE 1 2 3 4 5 6 7 8 9 10 11 12

DTX361X/4

DTX361X/4

OF 6