
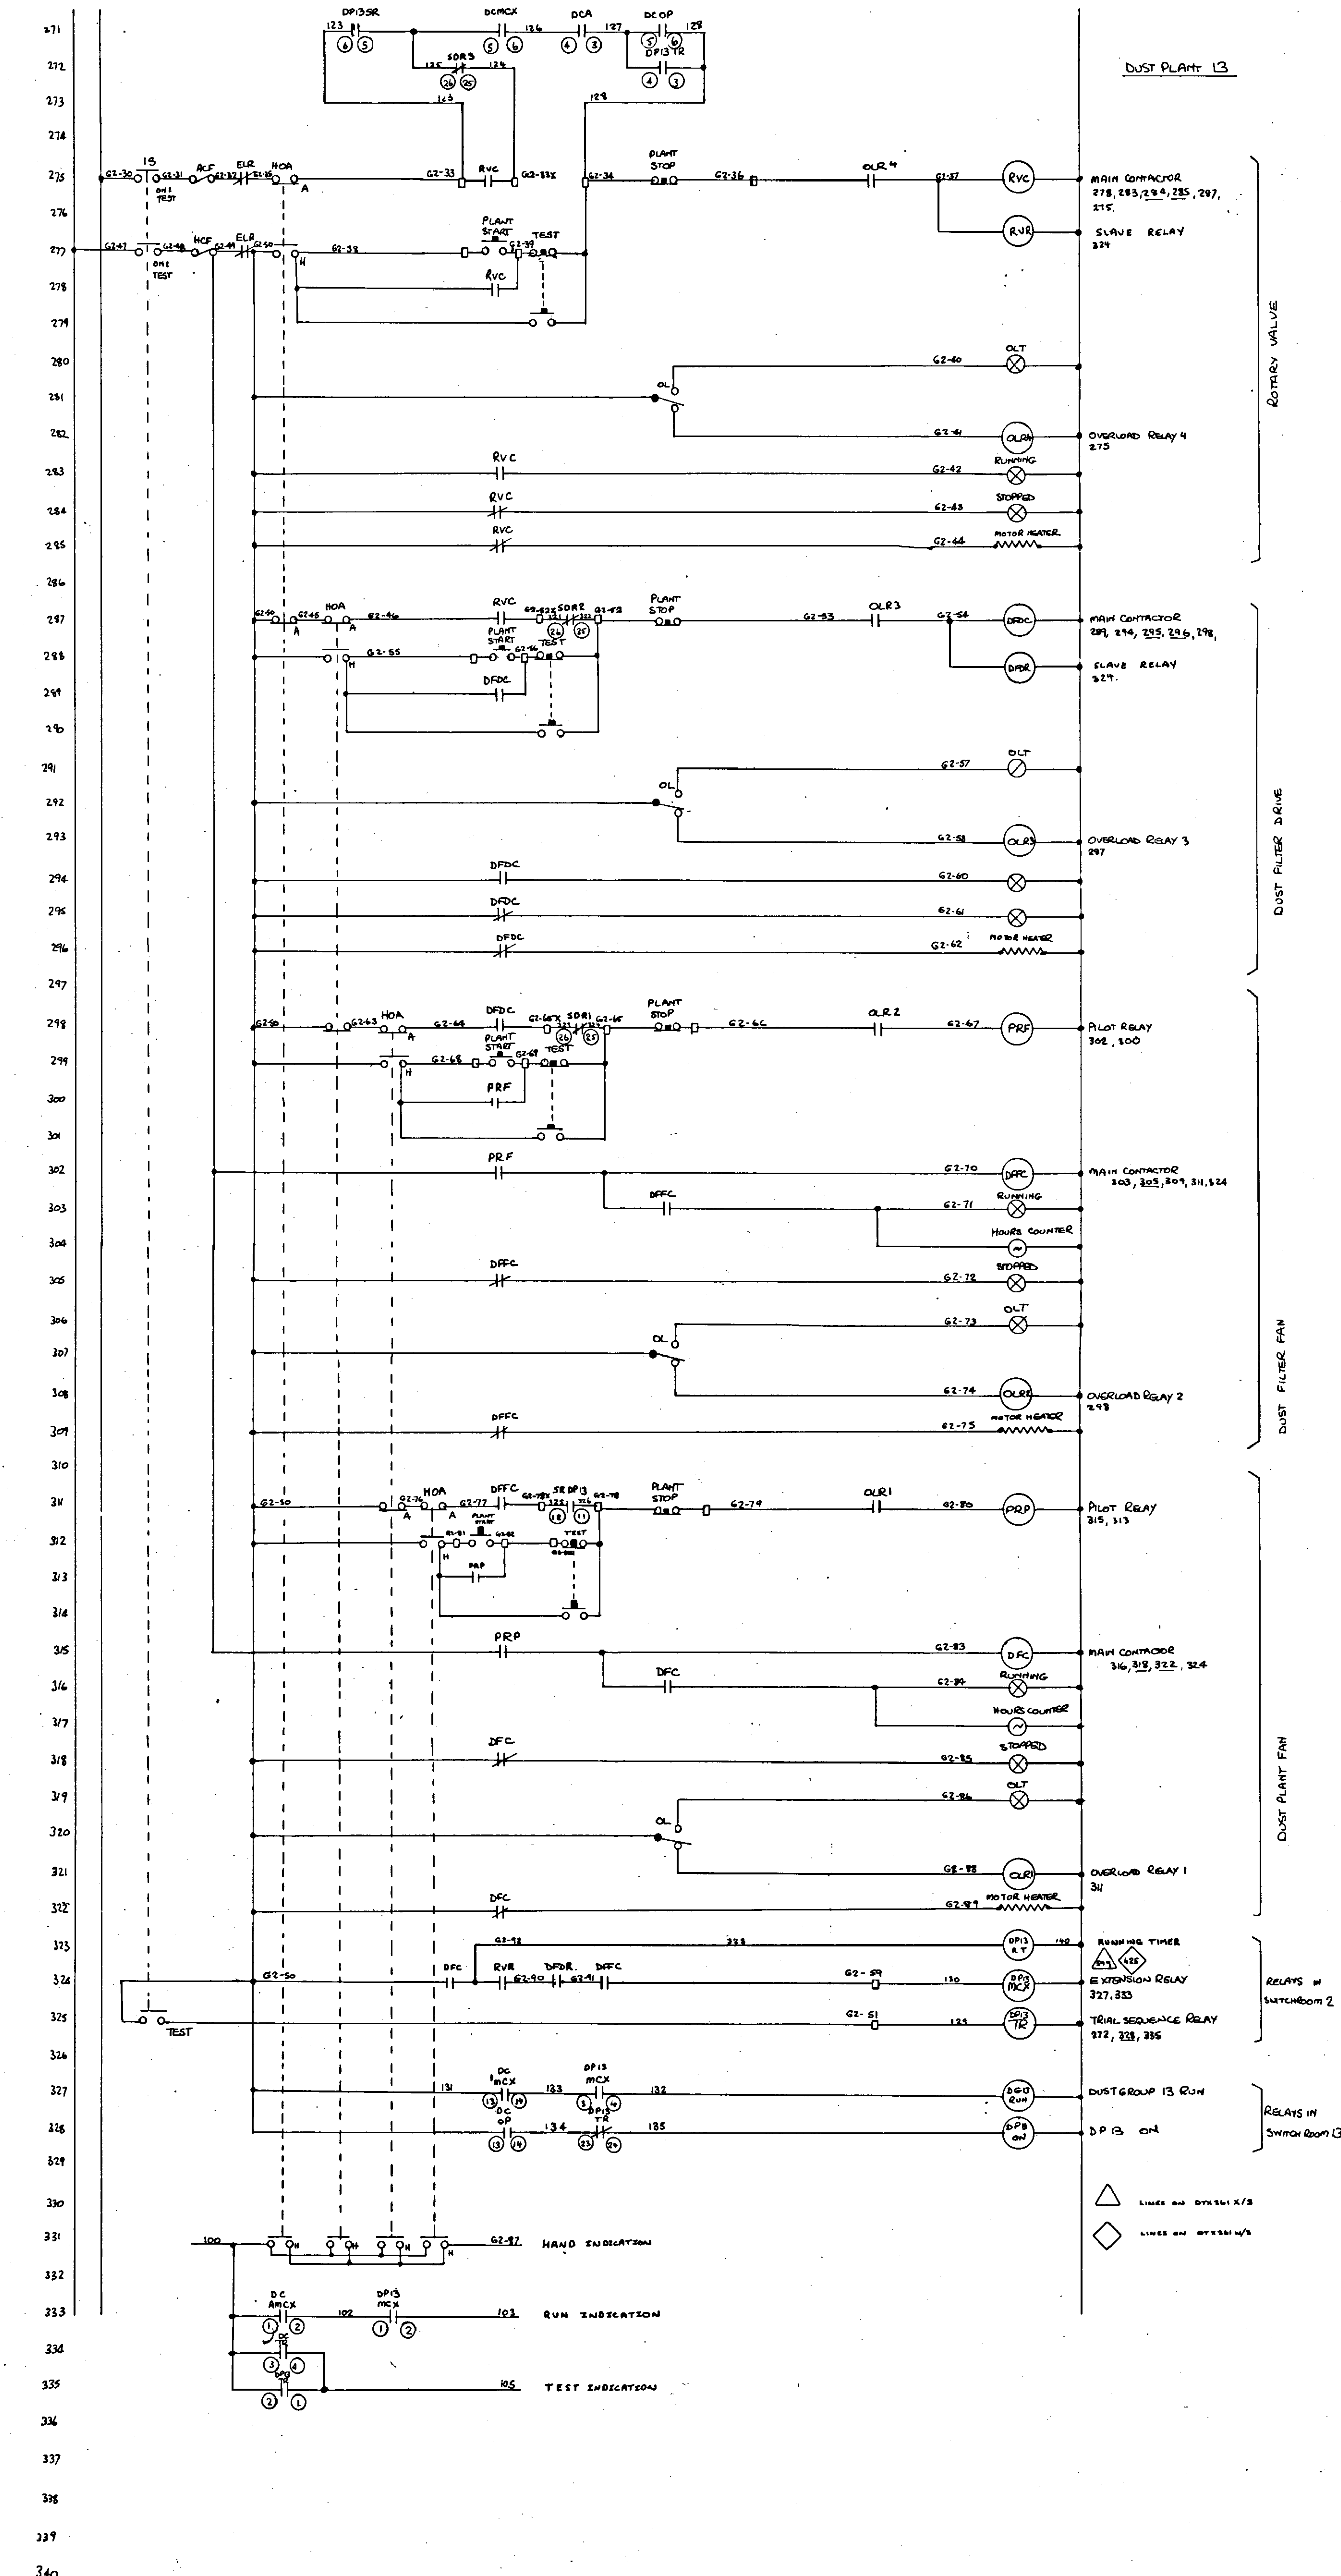


109000

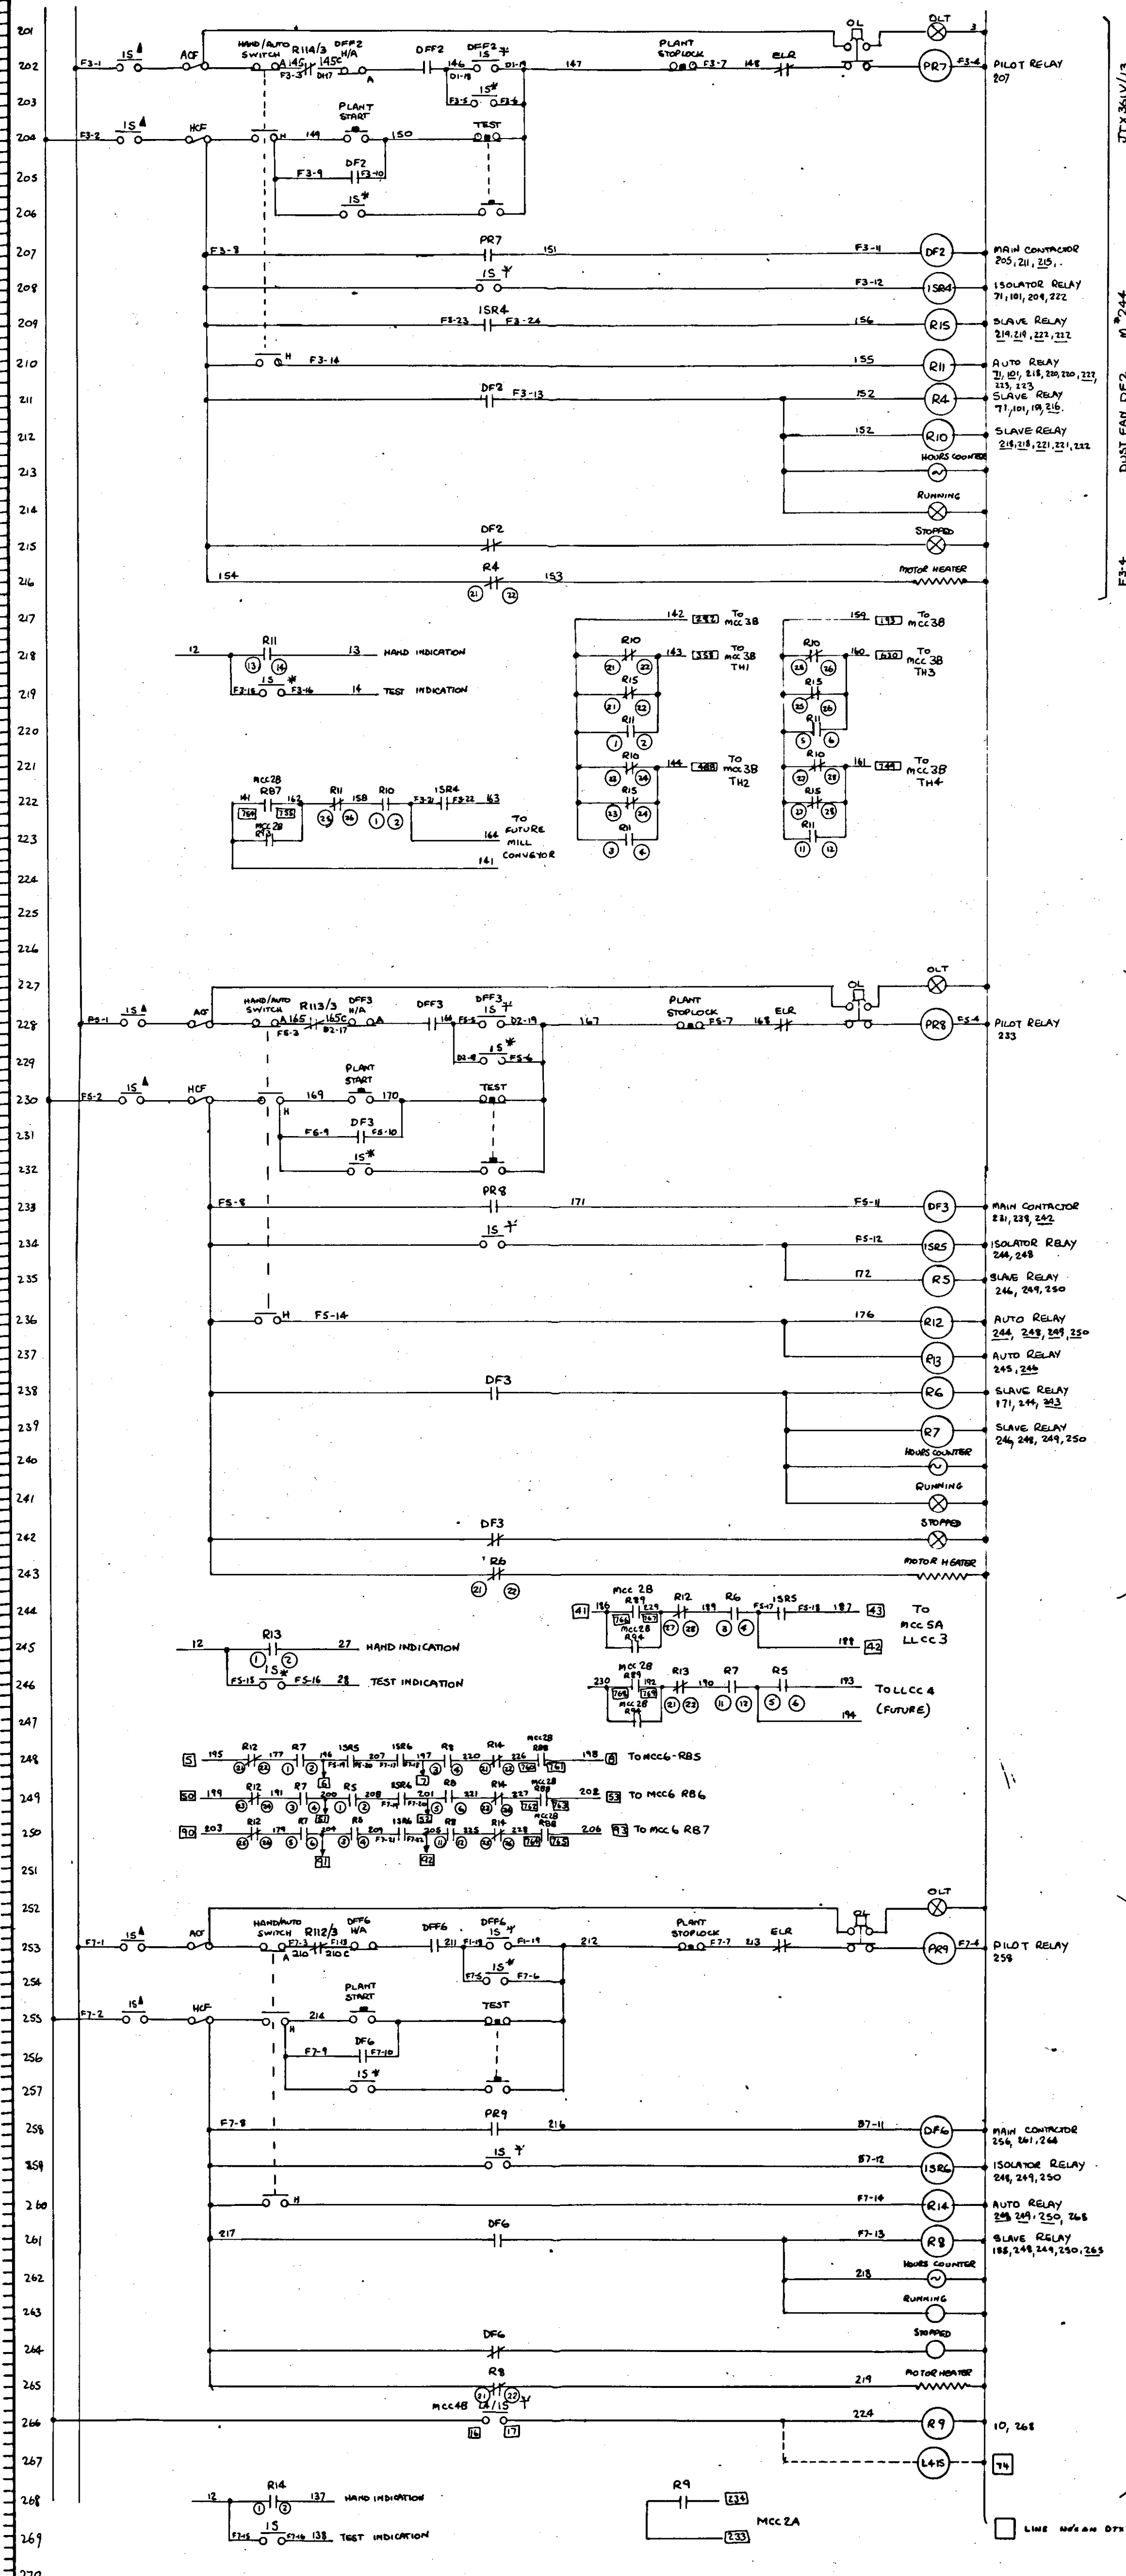

20A.

109000

THE DESIGN AND MANUFACTURING INFORMATION CONTAINED IN THIS DRAWING IS THE EXCLUSIVE RIGHT OF DEWHURST & PARTNER LTD. AND MUST NOT BE COPIED OR USED FOR MANUFACTURING PURPOSES.	ISSUE	1st	16	17	18	19	20	21											
	DTX 361Y / 2																		
	DTX 361Y / 2																		
KEY DIAG. No.																			
EXT. DIAG. No.	SDA 261Y																		
REL. DIAG. No.																			
PANEL LAYOUT No.	HTX 36Y																		

DEWHURST & PARTNER LTD.
MELBOURNE WORKS HOUNSLOW

TITLE:	SCHEME FOR MCC 2C - SEAFORTH GRAIN TERMINAL
--------	---

[illegible]

REVISION 20
Dust plant sequenced
shut down— Mods on
lines 202, 228, 253,
21-6-77

REVISION : 14	DRAWN
REDRAWN	DATE
	CHECK
	APPRO
ORIGIN : ICD 21 / 1 / 75GD. <i>Di...</i>	DATE

REVISION : 19
AIR REGD CONTRACTS W
ON LINE SIS. ANOTHER
ON DPISAT USED.
ORIGINALD
8/8/78 AJSB
N BY A.M.
26/1/79
ED BY
VED BY