

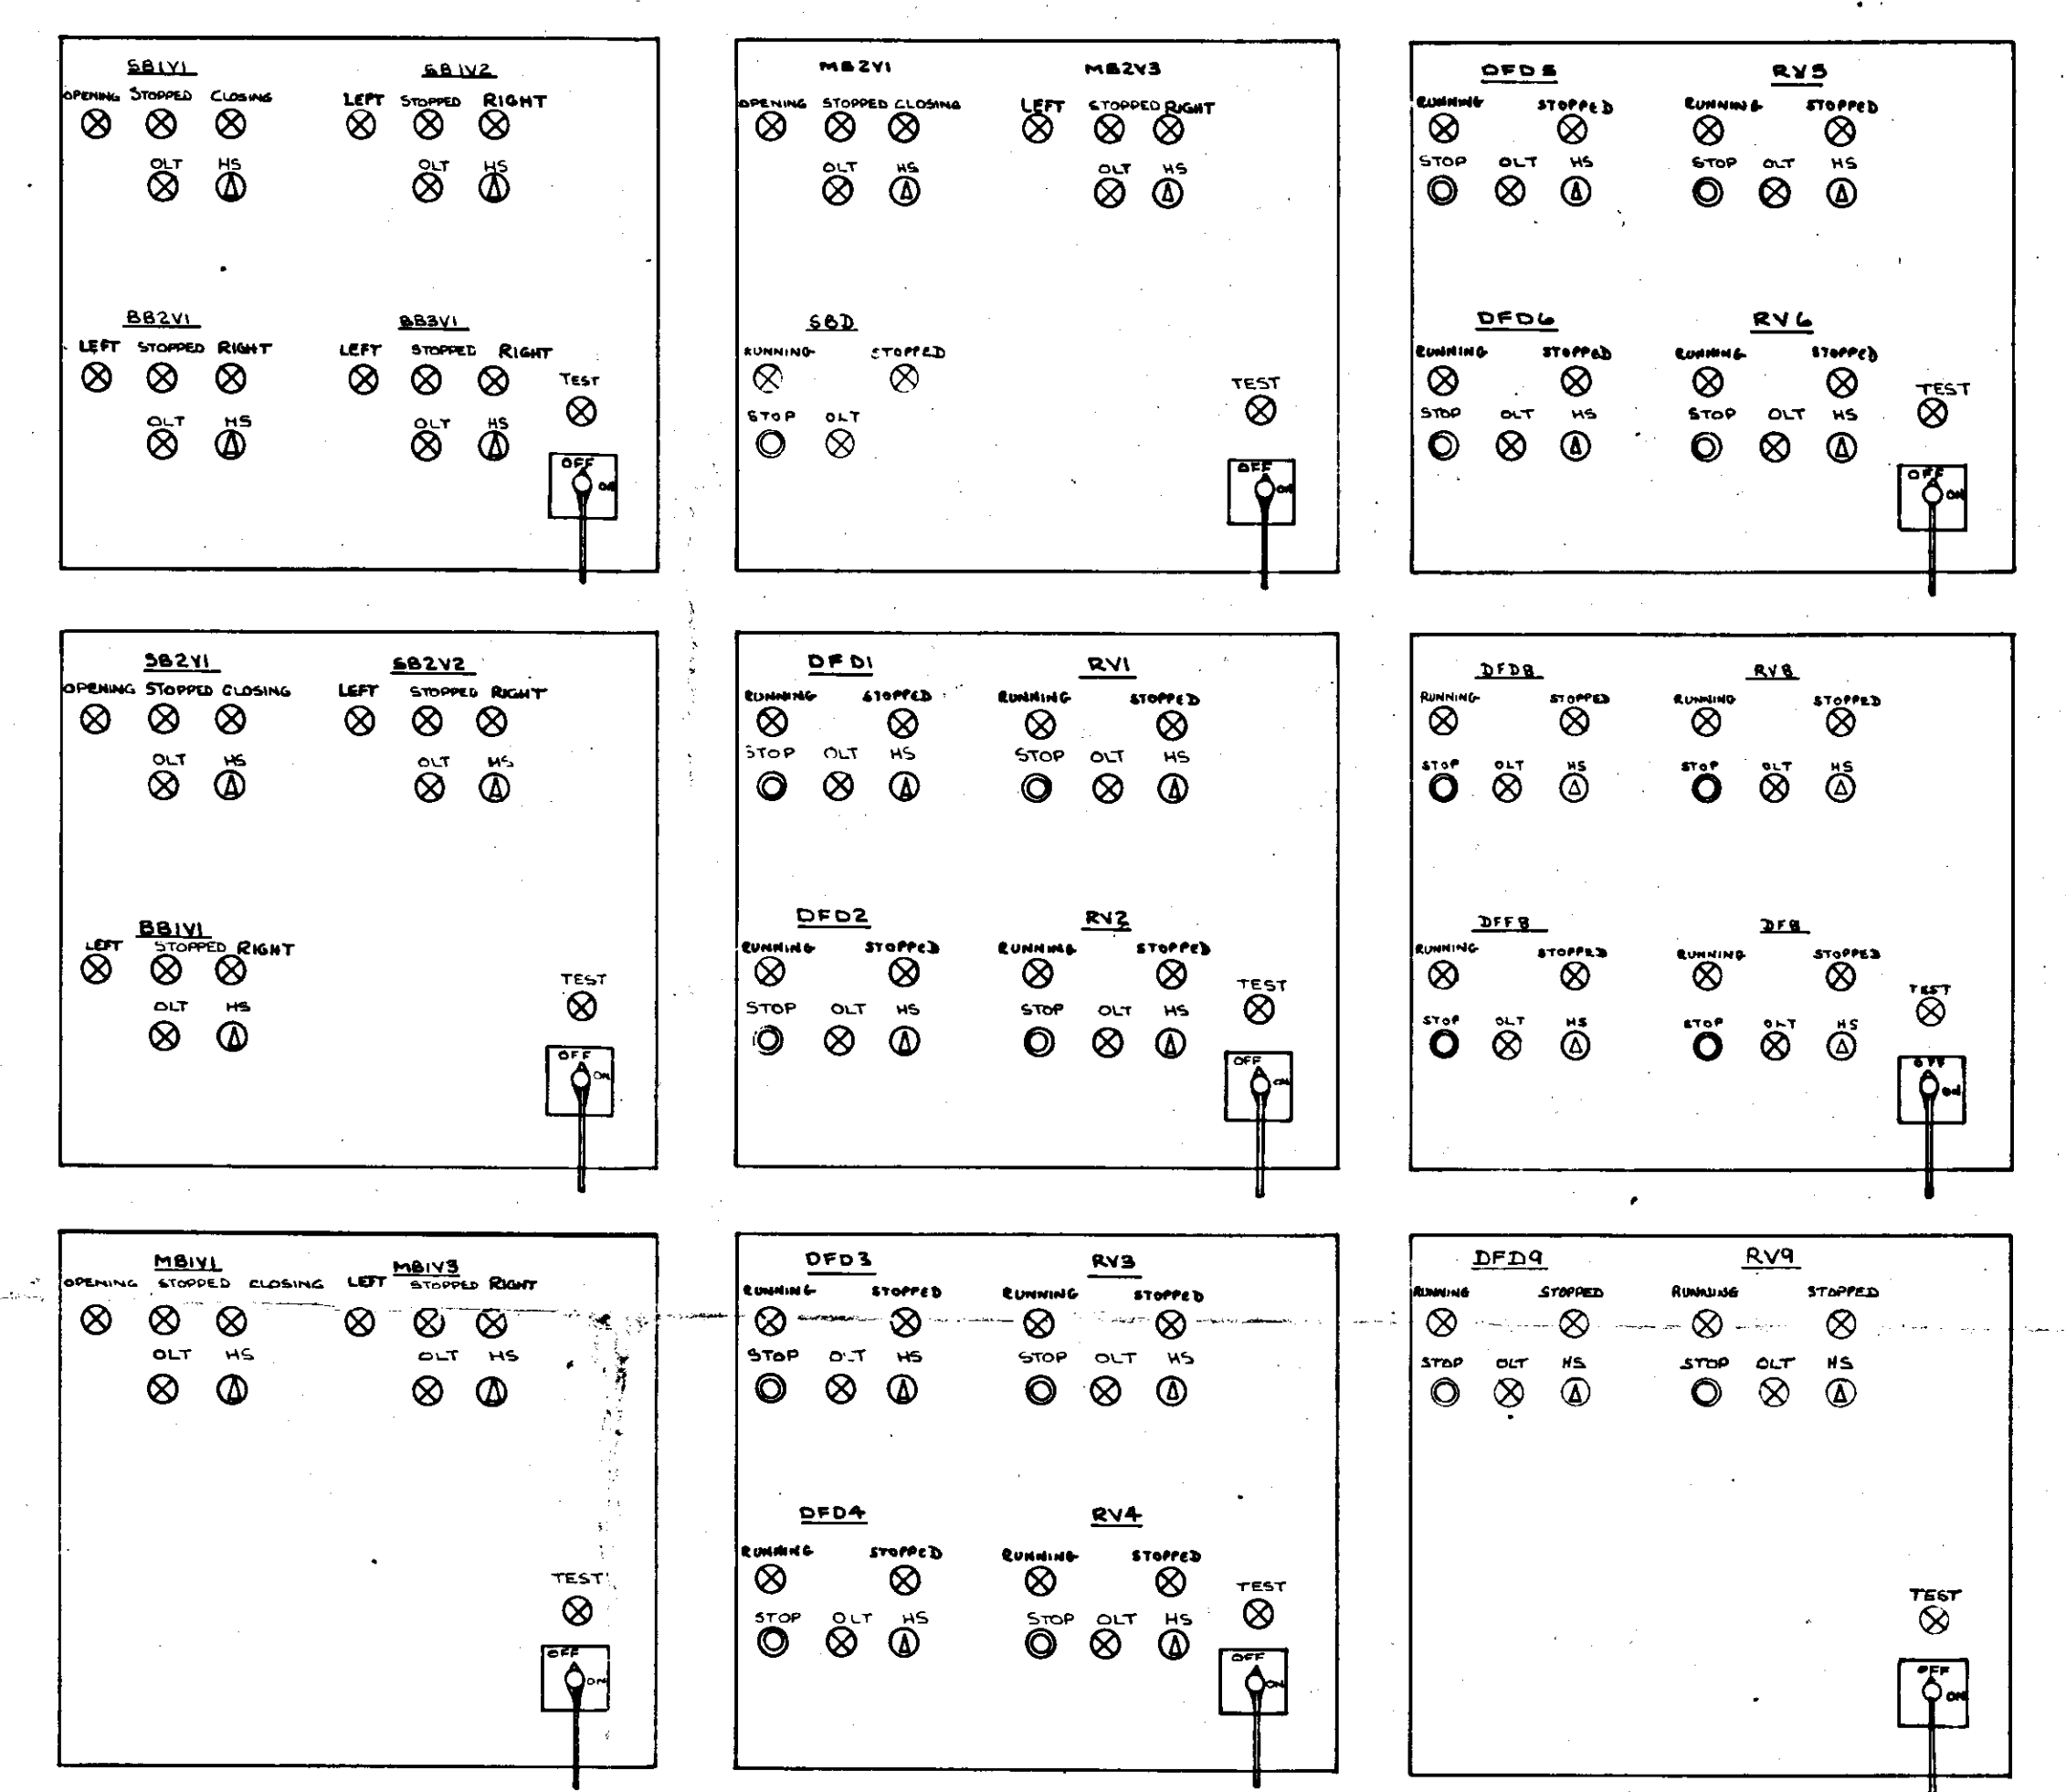
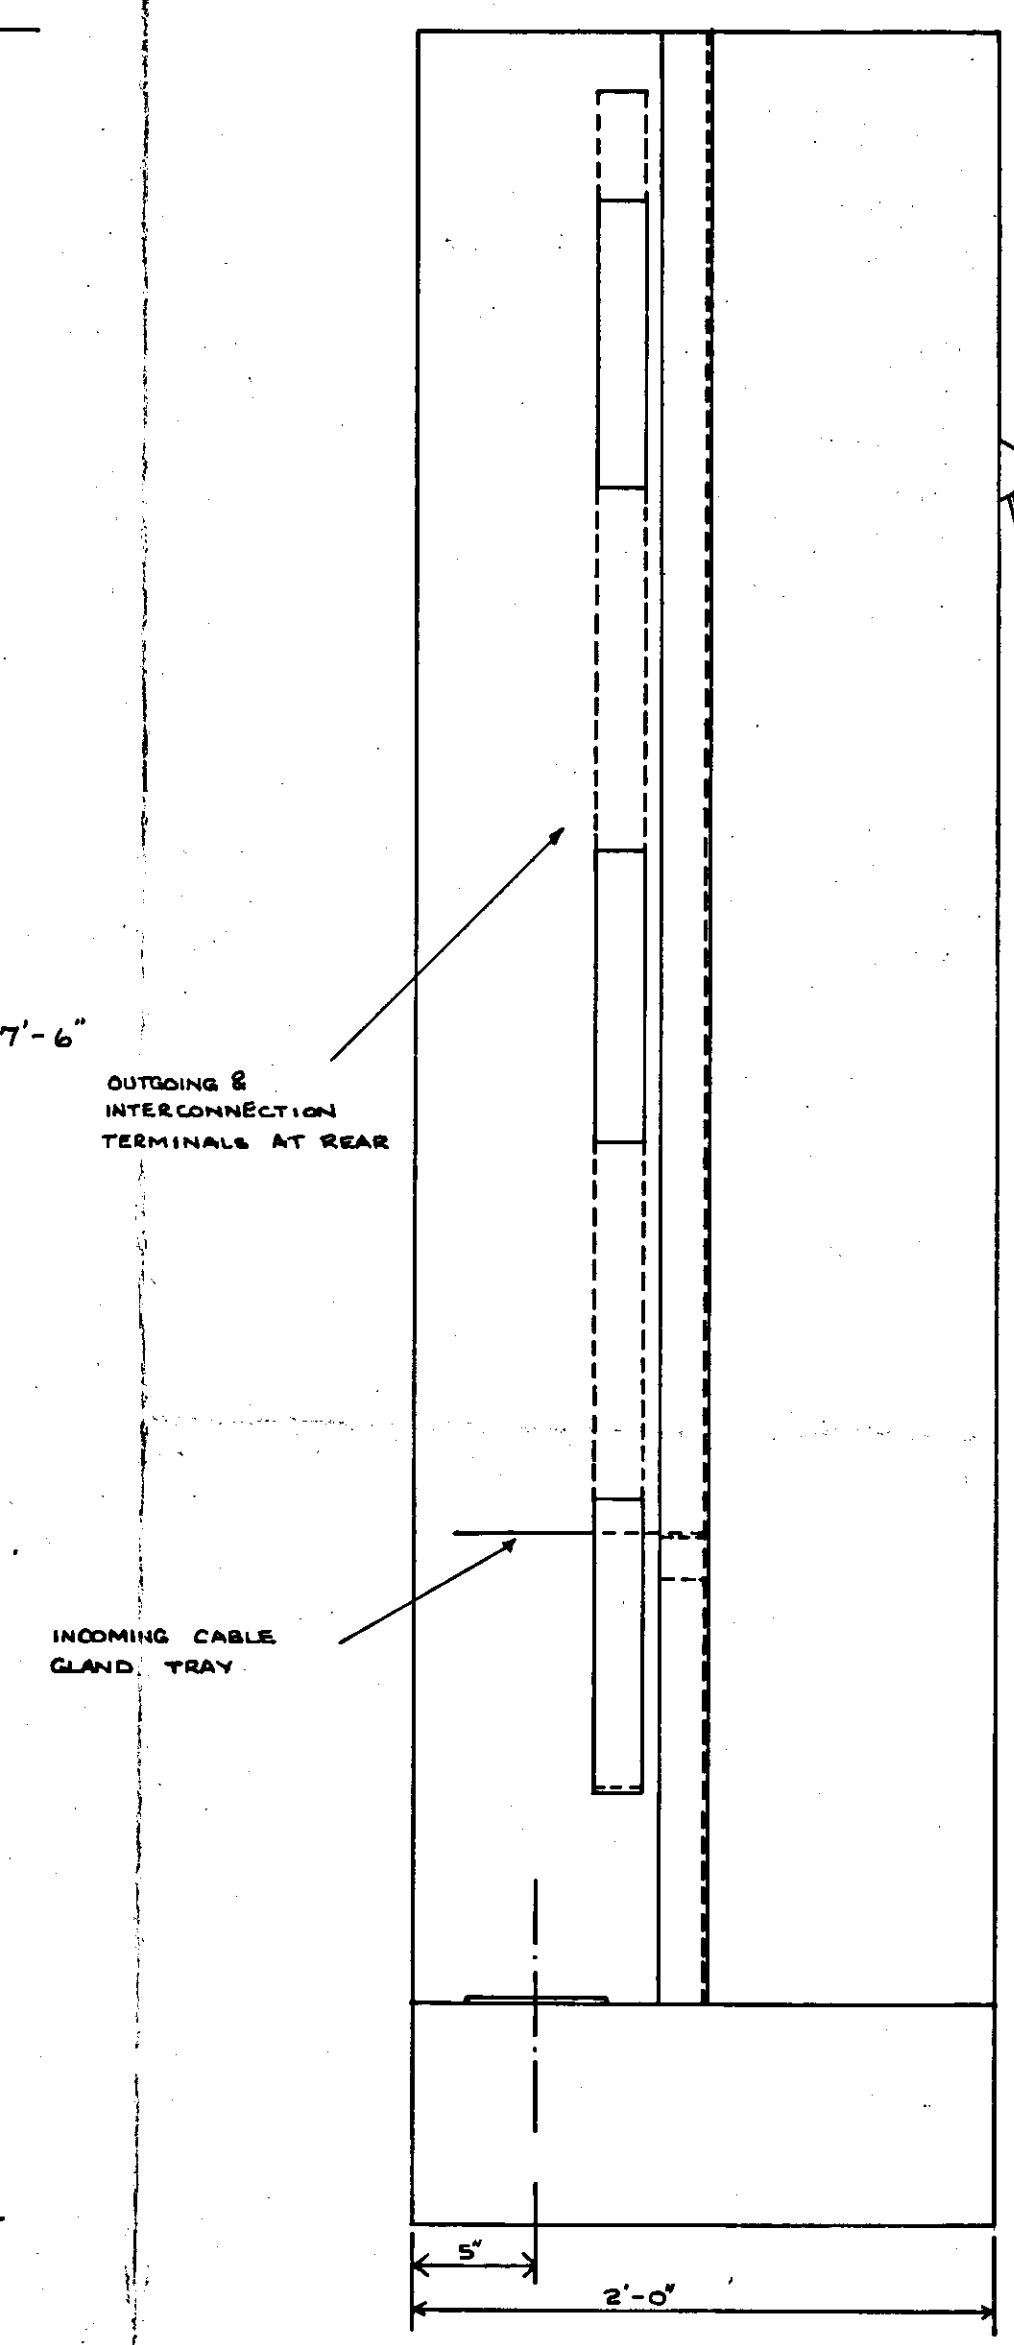


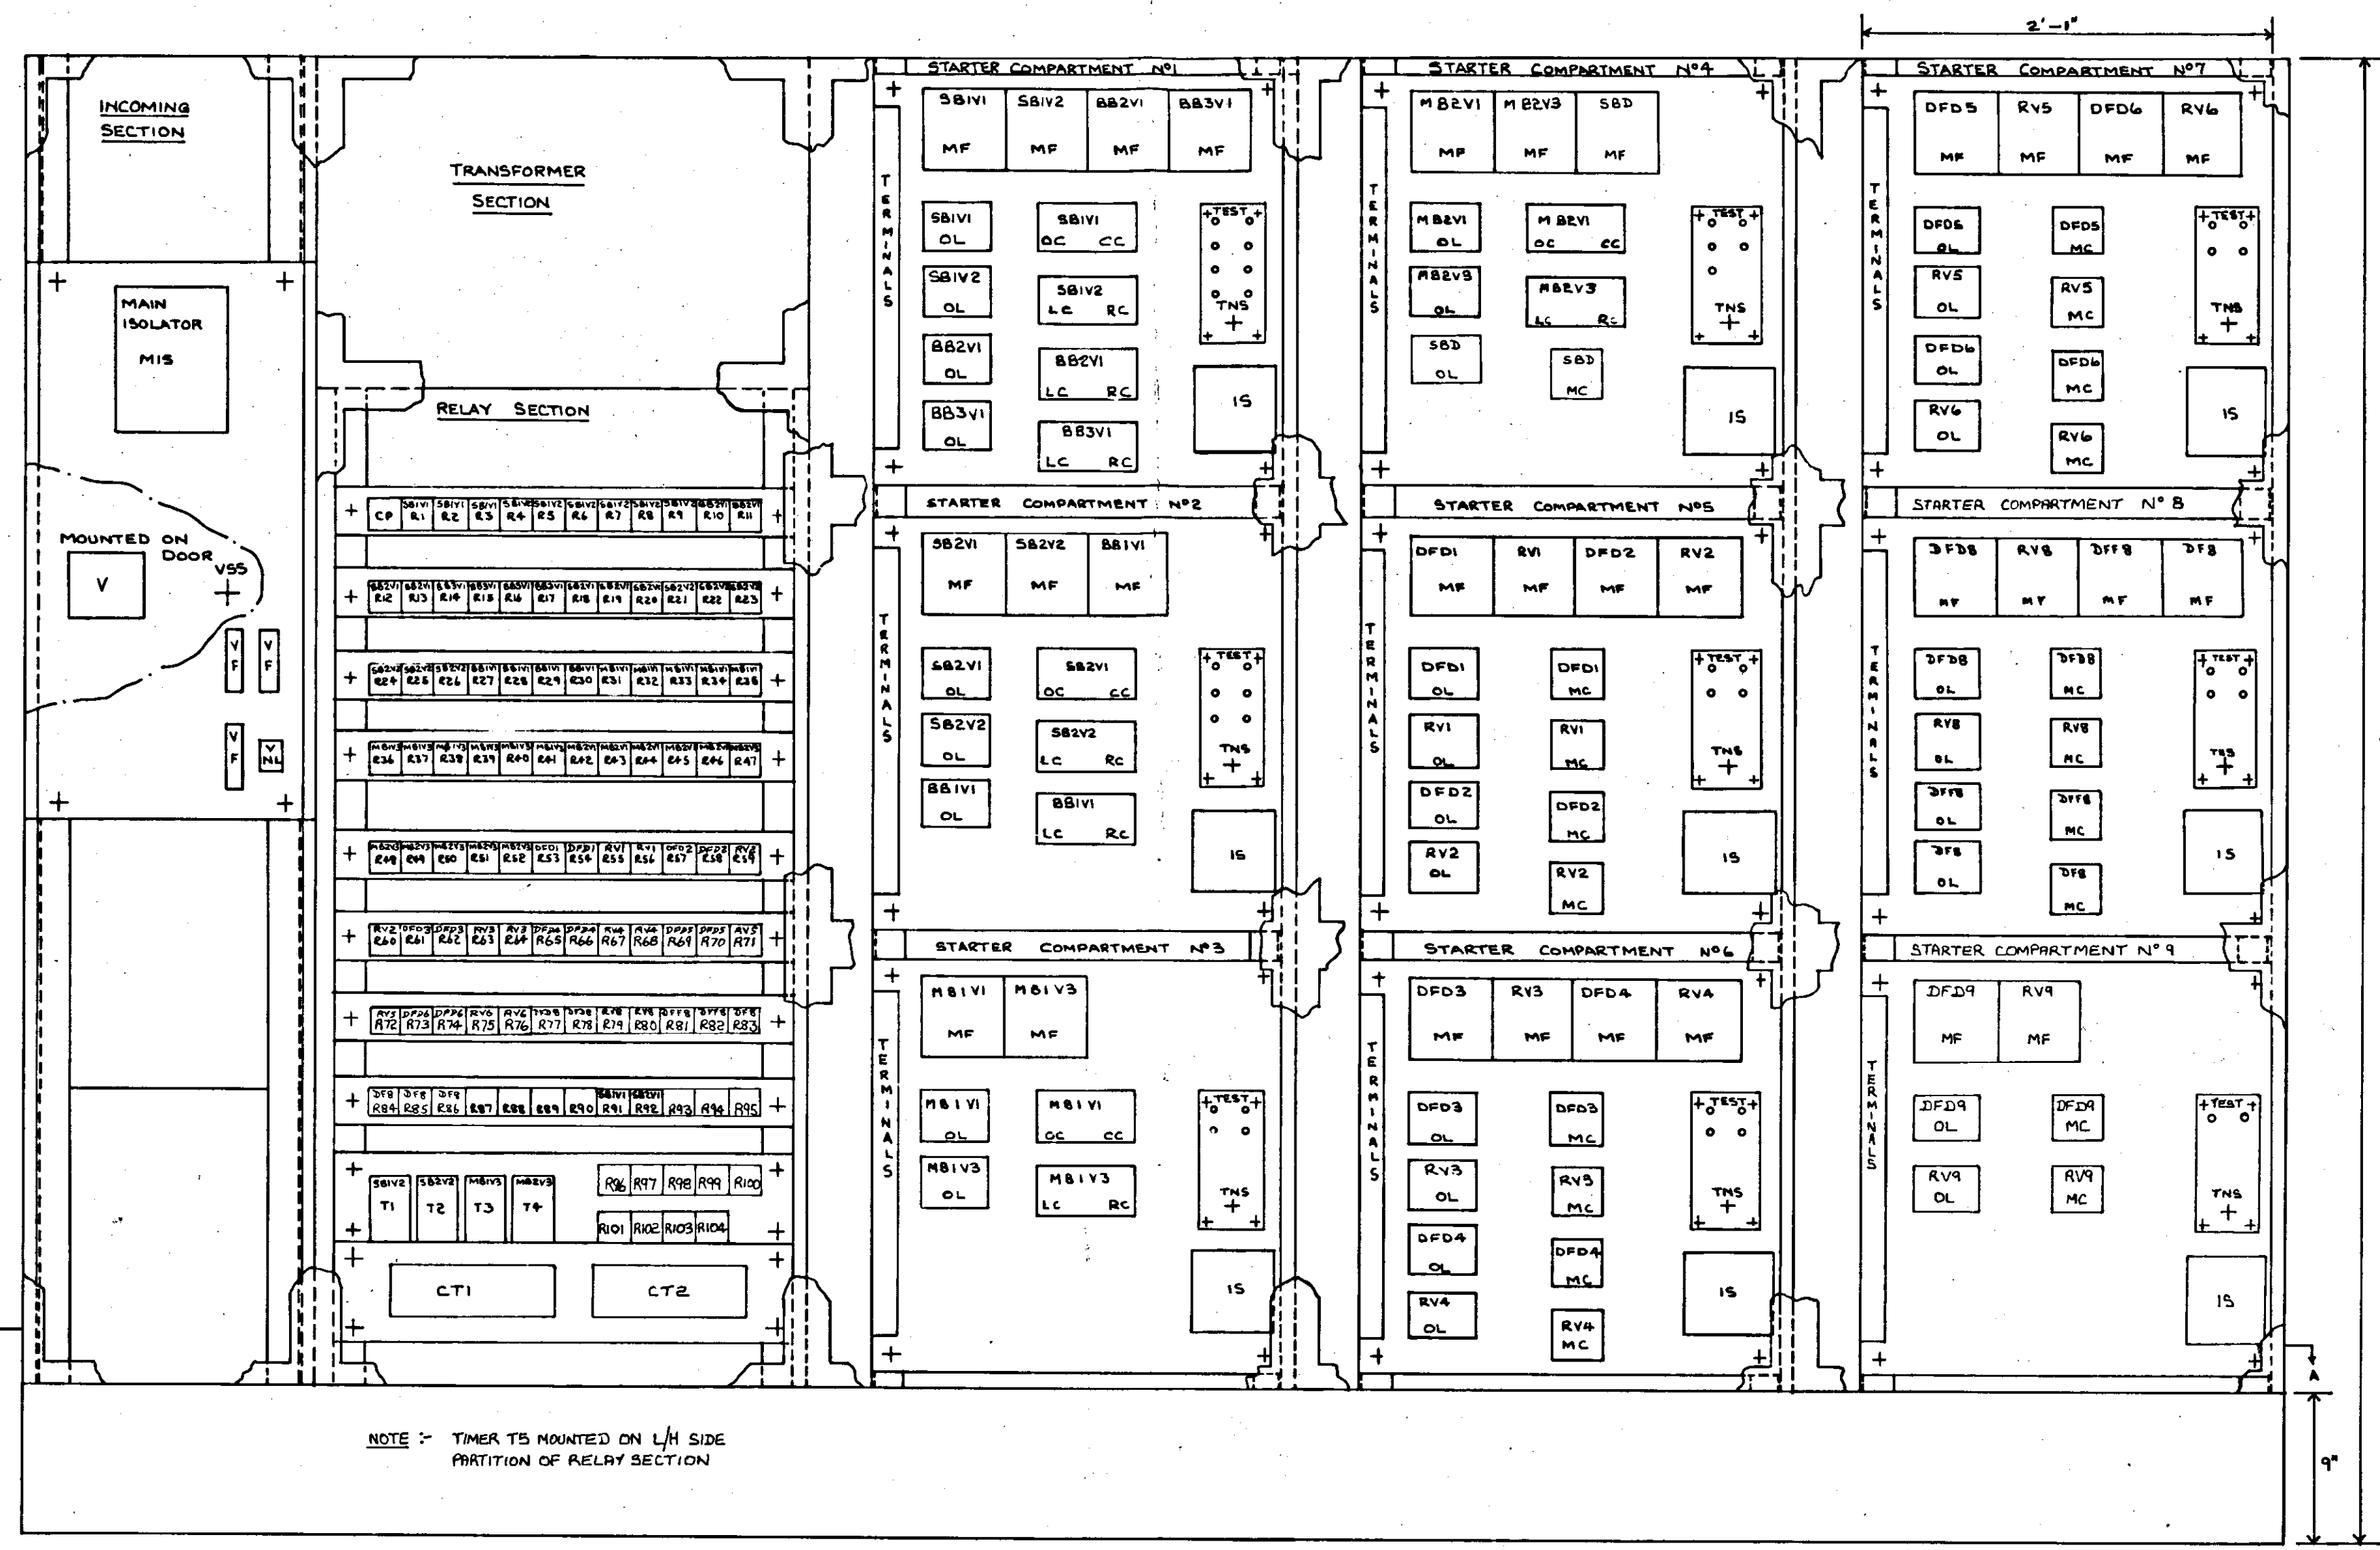

TO BE REVISED
 JUST PLANT SYSTEM MODIFIED
 SOME PANELS REDUNDANT IN PART.

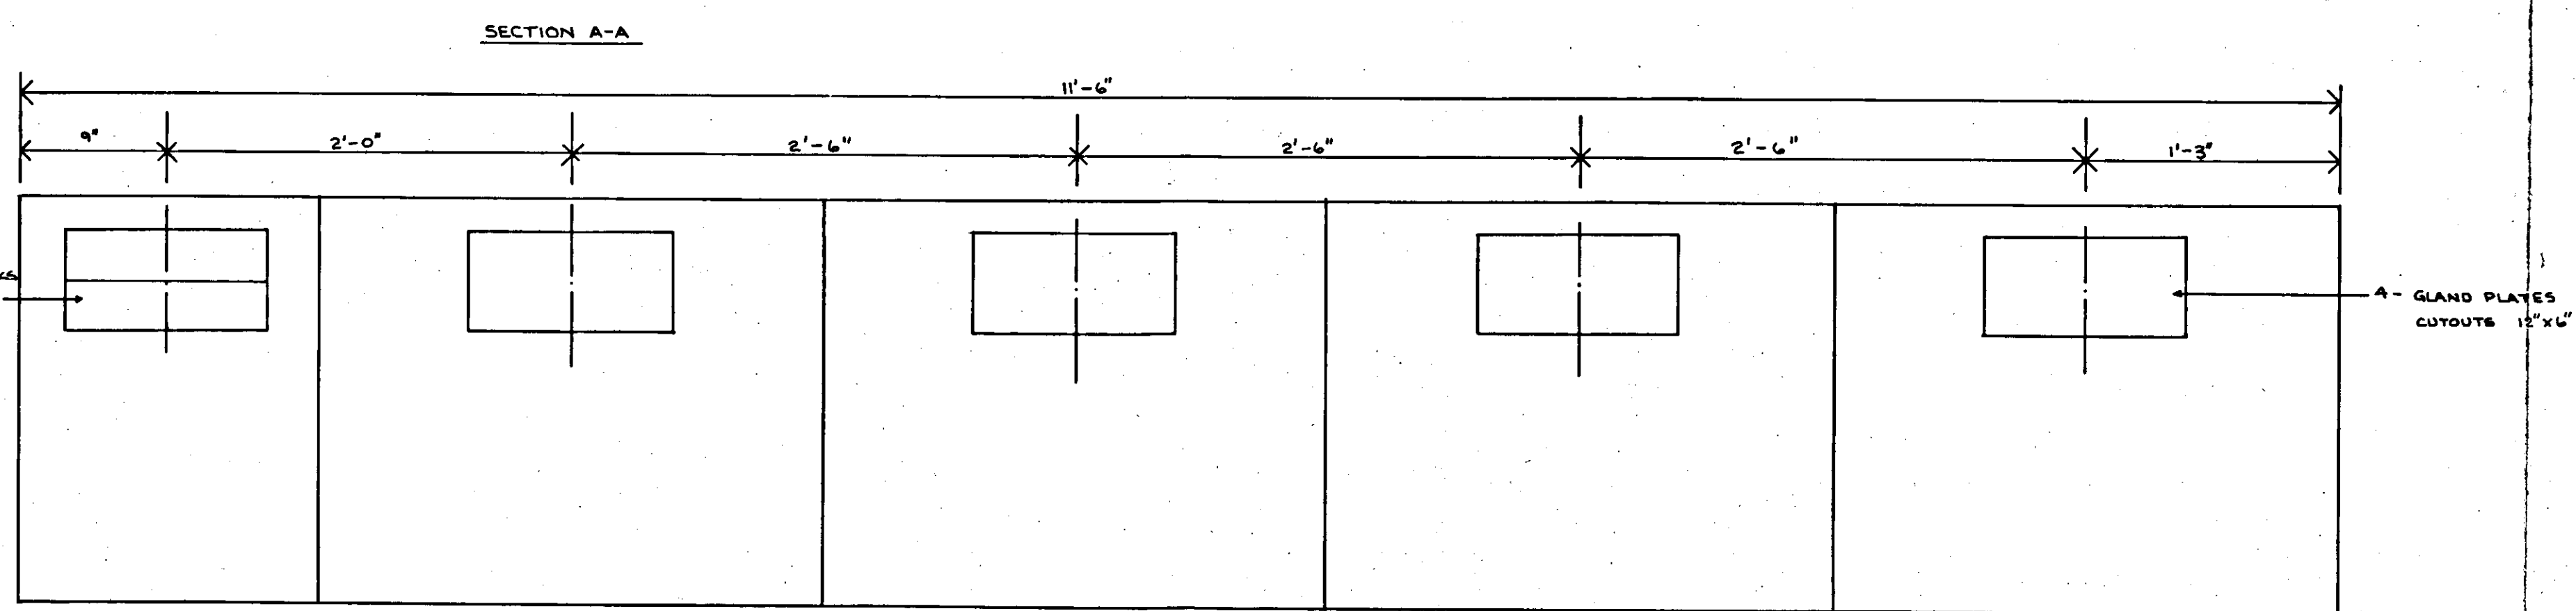

LAYOUT FOR MCC 2B-SEAFORTH GRAIN TERMINAL

DEWHURST & PARTNER LTD.
 MELBOURNE WORKS HOUNSLOW

TITLE:
 LAYOUT FOR MCC 2B-SEAFORTH GRAIN TERMINAL

REVISION: 7 R101 TO R104 ADDED.	REVISION: 6 R105 TO R108 ADDED.	REVISION: 5 C11 & C12 ADDED.	REVISION: 4 STARTER COMPARTMENT N°1 & N°2 ADDED.	REVISION: 3 R109 & R110 ADDED.	REVISION: 2 R111 & R112 ADDED.	REVISION: 1 R113 & R114 ADDED.
ORIGIN: ICD 4/7/72	ORIGIN: CUST 8/5/72	ORIGIN: CUST 8/5/72	ORIGIN: ICD 7/3/72	ORIGIN: CUST 6/3/71	ORIGIN: CUST 2/1/71	ORIGIN: CUST 5/1/71

DRAWN BY: GMB
 DATE: 14.12.70
 CHECKED BY:
 APPROVED BY:
 DATE:

THE DESIGN AND MANUFACTURING INFORMATION CONTAINED IN THIS DRAWING IS THE EXCLUSIVE RIGHT OF DEWHURST & PARTNER LTD. AND MUST NOT BE COPIED OR USED FOR MANUFACTURING PURPOSES.	ISSUE: 1 2 3 4 5 6 7
KEY DIAG. No. 273311-2 EXT. DIAG. No. 273311-X REL. DIAG. No. 273311-Y PANEL LAYOUT No. 273311-Z	HTX361X
	HTX361X