

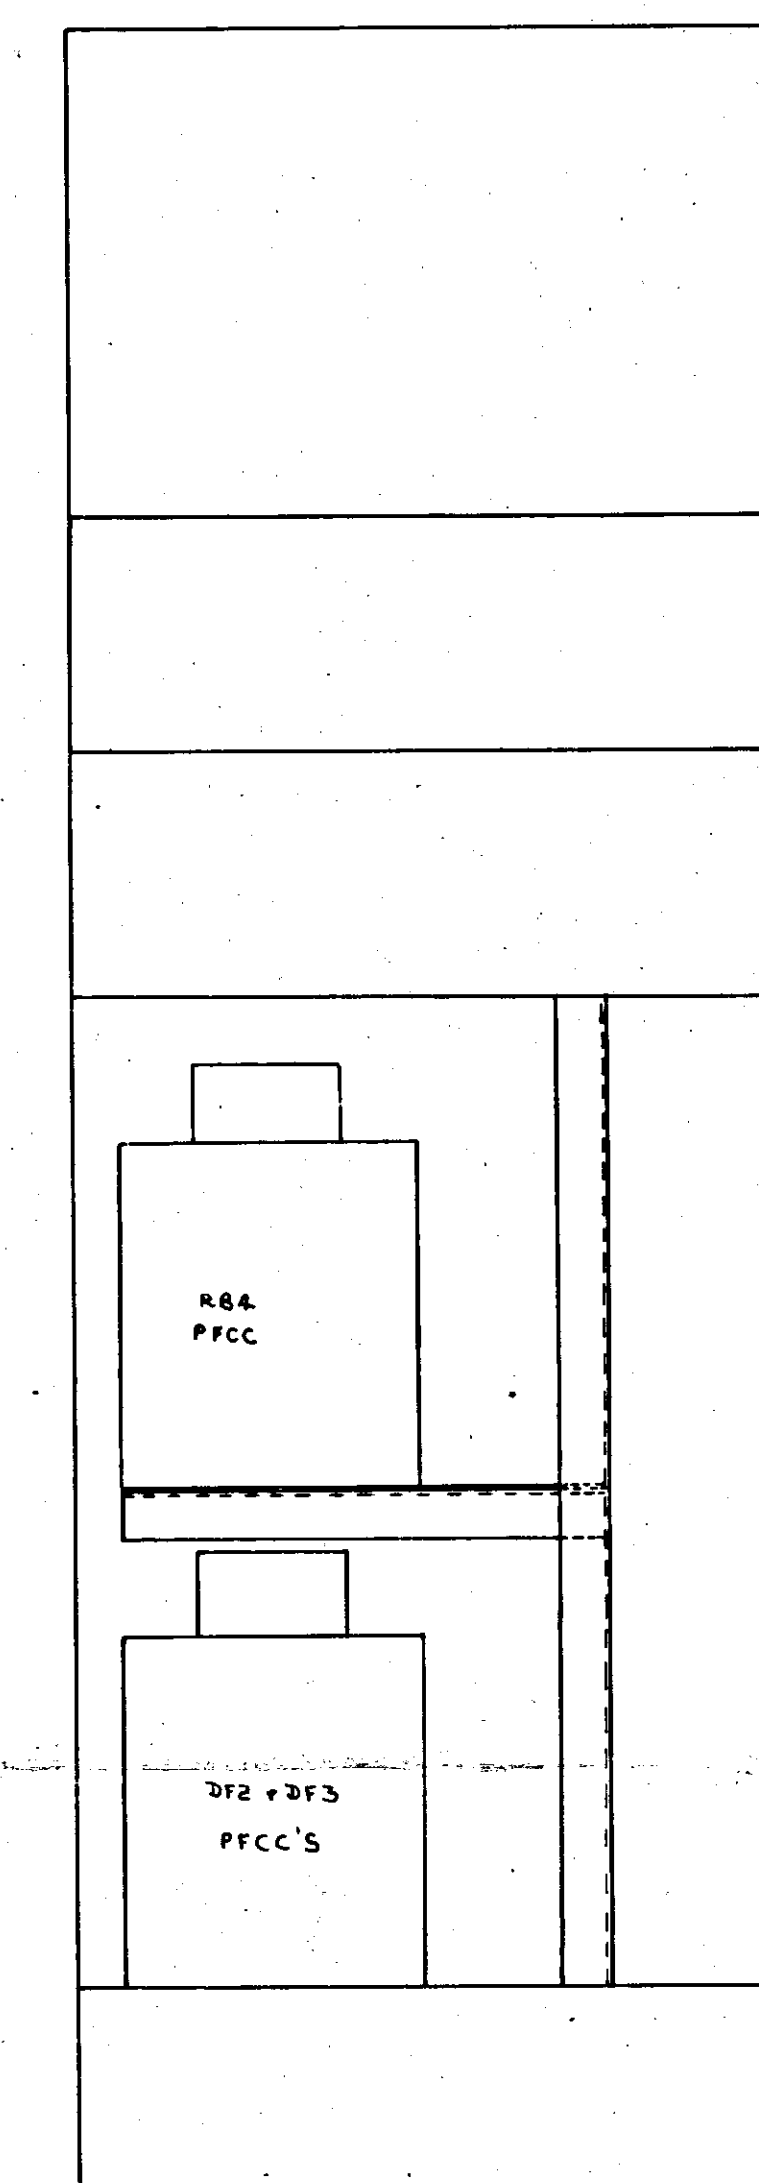
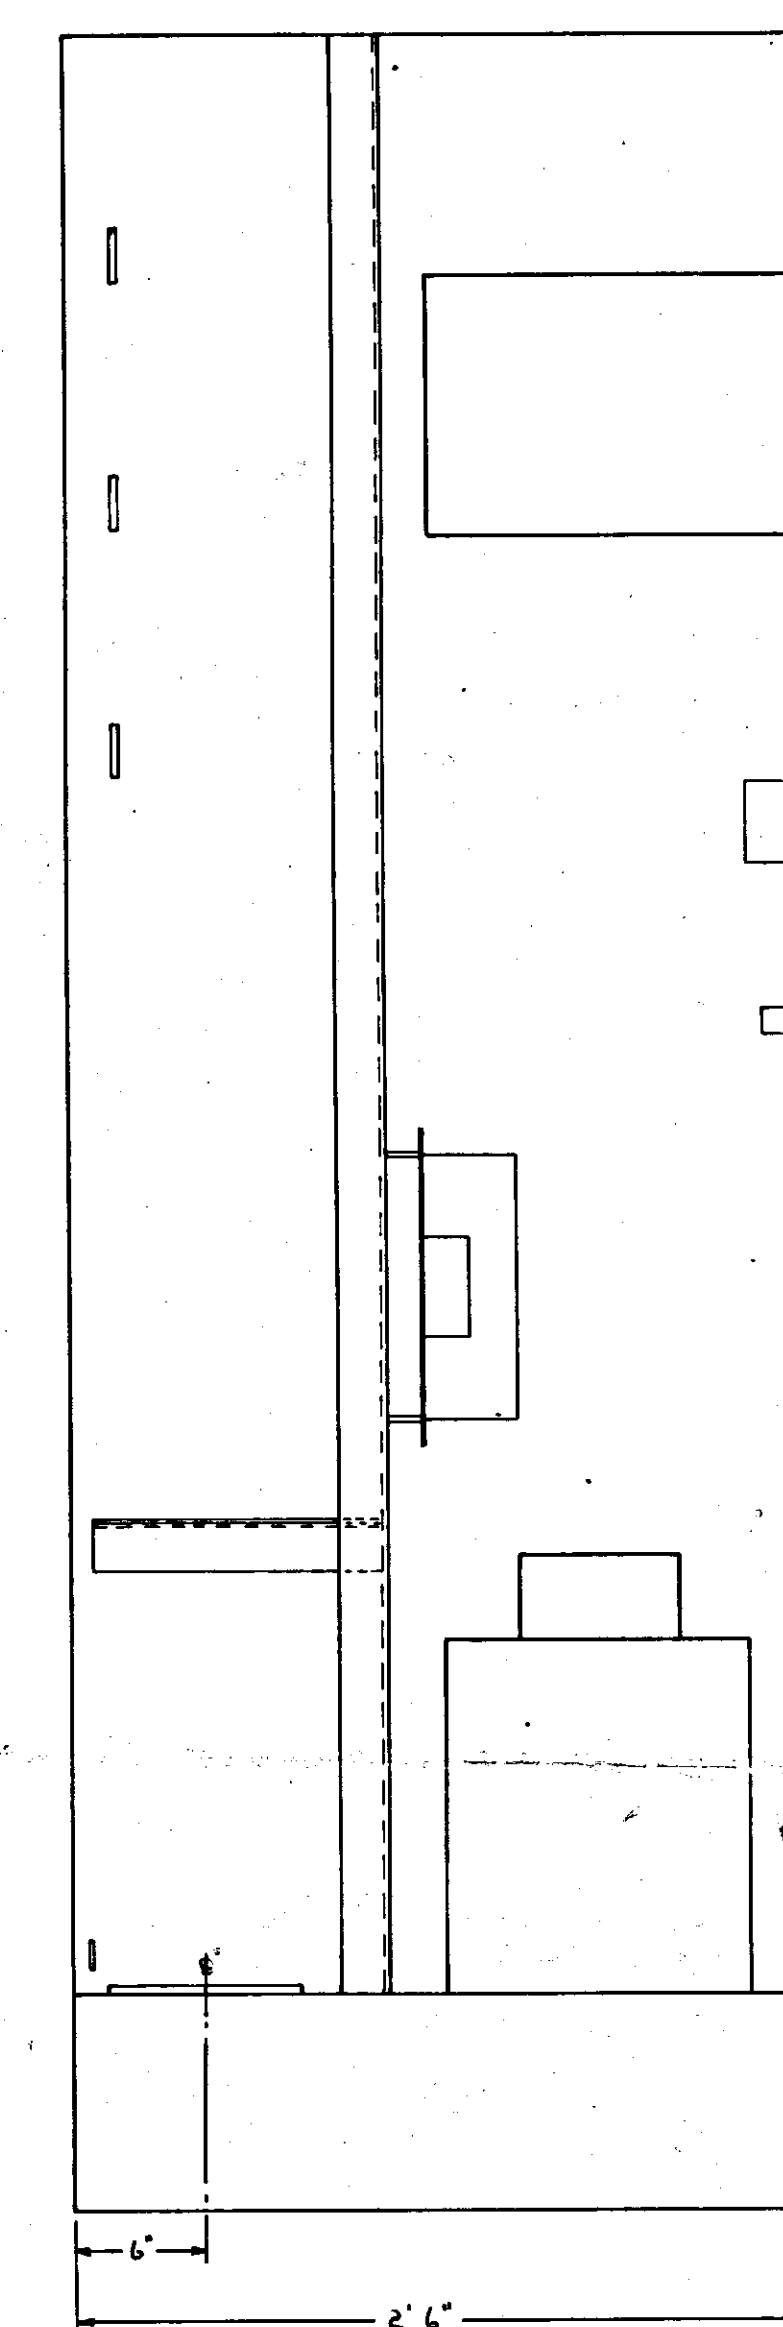


SECTION B-B

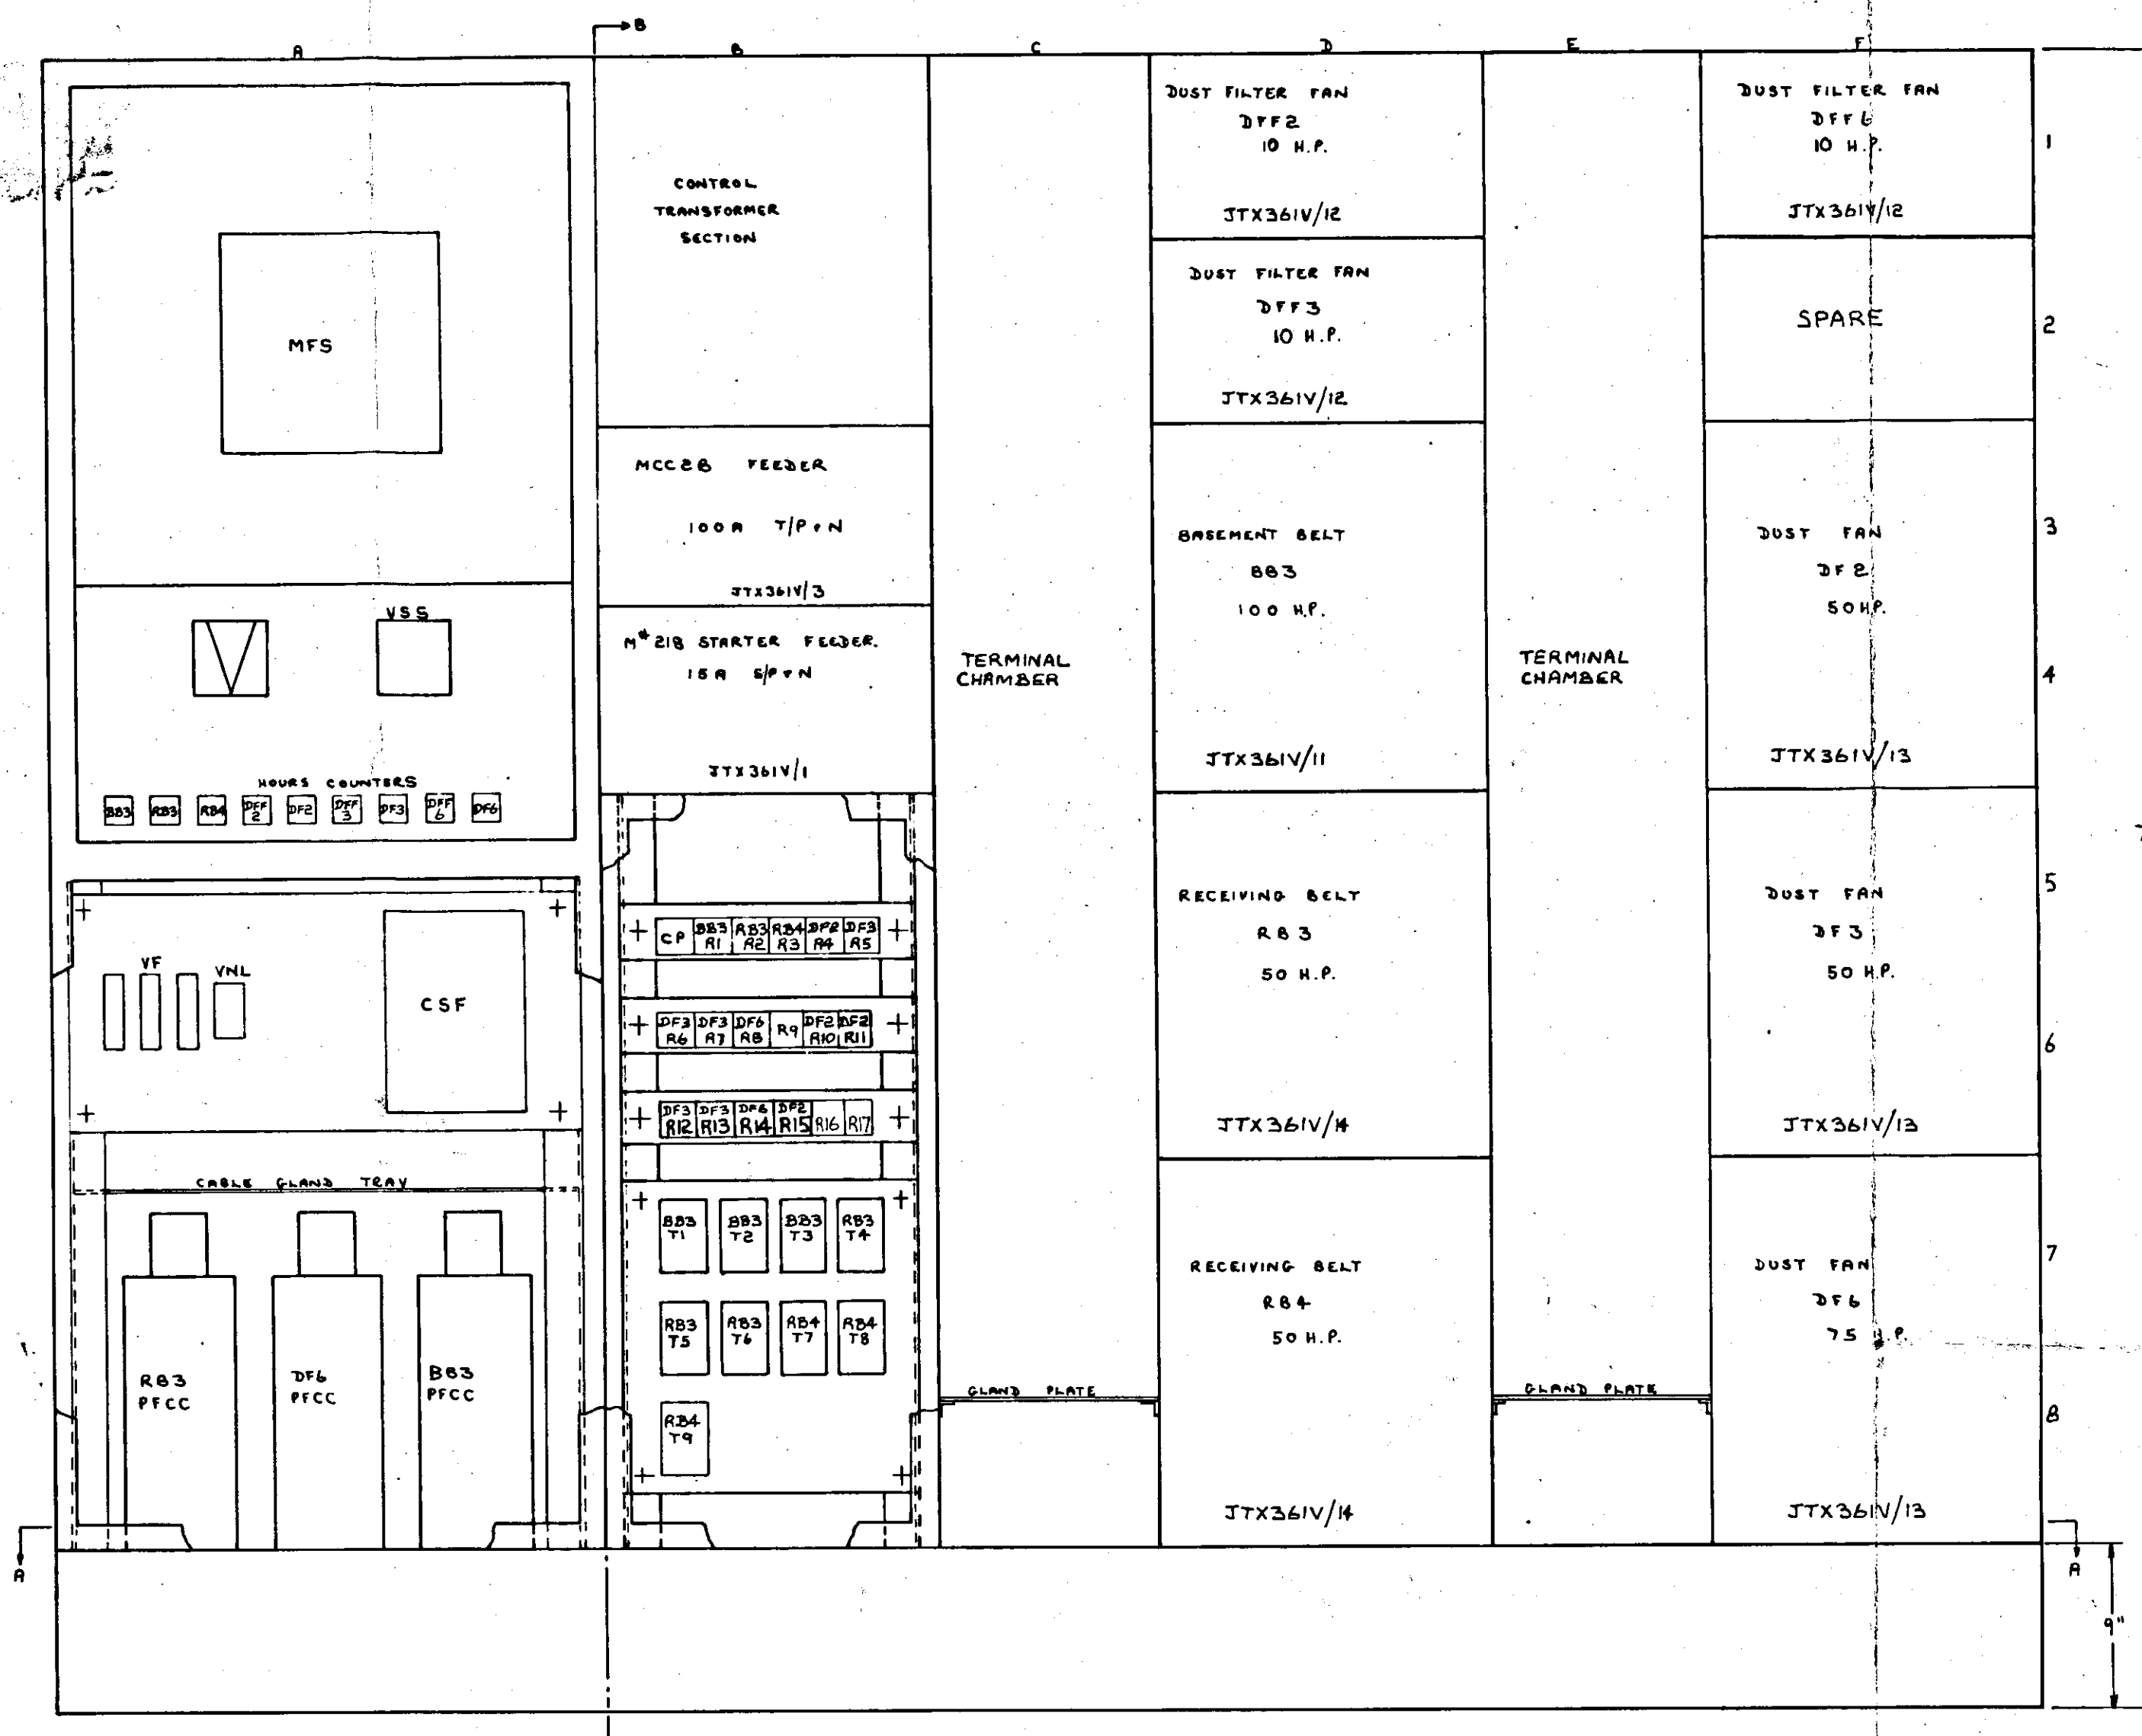

SECTION A-A

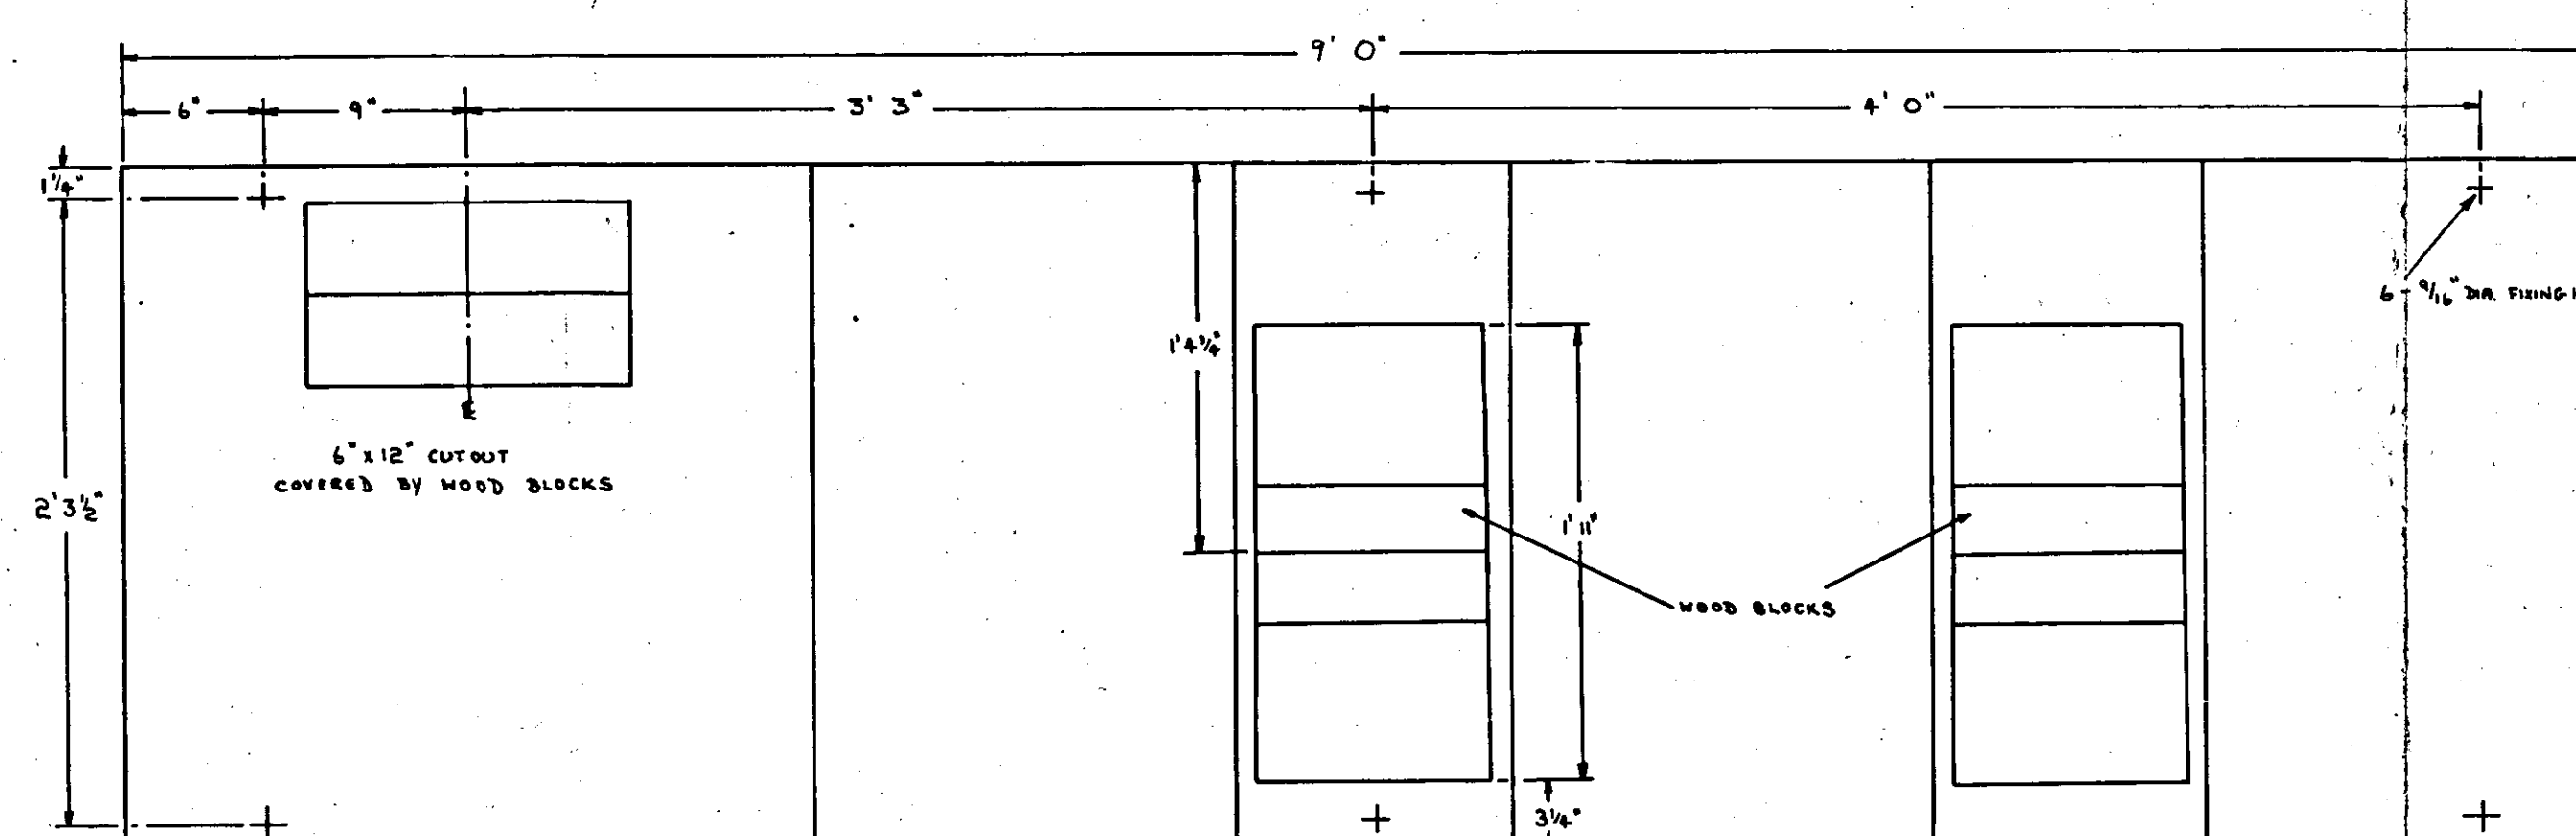

- NOTES
- ① PANEL TO BE DESPATCHED IN ONE SECTION
 - ② PANEL TO BE LIFTED FROM TOP

LAYOUT FOR MCC2C - SEAFORTH GRAIN TERMINAL

THE DESIGN AND MANUFACTURING INFORMATION CONTAINED IN THIS DRAWING IS THE EXCLUSIVE RIGHT OF DEWHURST & PARTNER LTD. AND MUST NOT BE COPIED OR USED FOR MANUFACTURING PURPOSES.	ISSUE	1	2	3	4	5	6	7	8
	HTX361Y								
	HTX361Y								

DEWHURST & PARTNER LTD.
MELBOURNE WORKS HOUNSLOW

TITLE:
LAYOUT FOR MCC2C - SEAFORTH GRAIN TERMINAL

REVISION: 7 REVISED BY: J.T.	REVISION: 6 REVISED BY: J.T.	REVISION: 5 REVISED BY: J.T.	REVISION: 4 REVISED BY: J.T.	REVISION: 3 REVISED BY: J.T.	REVISION: 2 REVISED BY: J.T.	REVISION: 1 REVISED BY: J.T.
ORIGIN: ELS P	ORIGIN: ELS P	ORIGIN: ELS P	ORIGIN: ELS P	ORIGIN: ELS P	ORIGIN: ELS P	ORIGIN: ELS P
DATE: 13/4/71	DATE: 13/4/71	DATE: 13/4/71	DATE: 13/4/71	DATE: 13/4/71	DATE: 13/4/71	DATE: 13/4/71

DRAWN BY: J.T.	CHECKED BY: J.T.	APPROVED BY: J.T.
DATE: 13/4/71	DATE: 13/4/71	DATE: 13/4/71

KEY DIAG. No.	EXT. DIAG. No.	REL. DIAG. No.	PANEL LAYOUT No.