

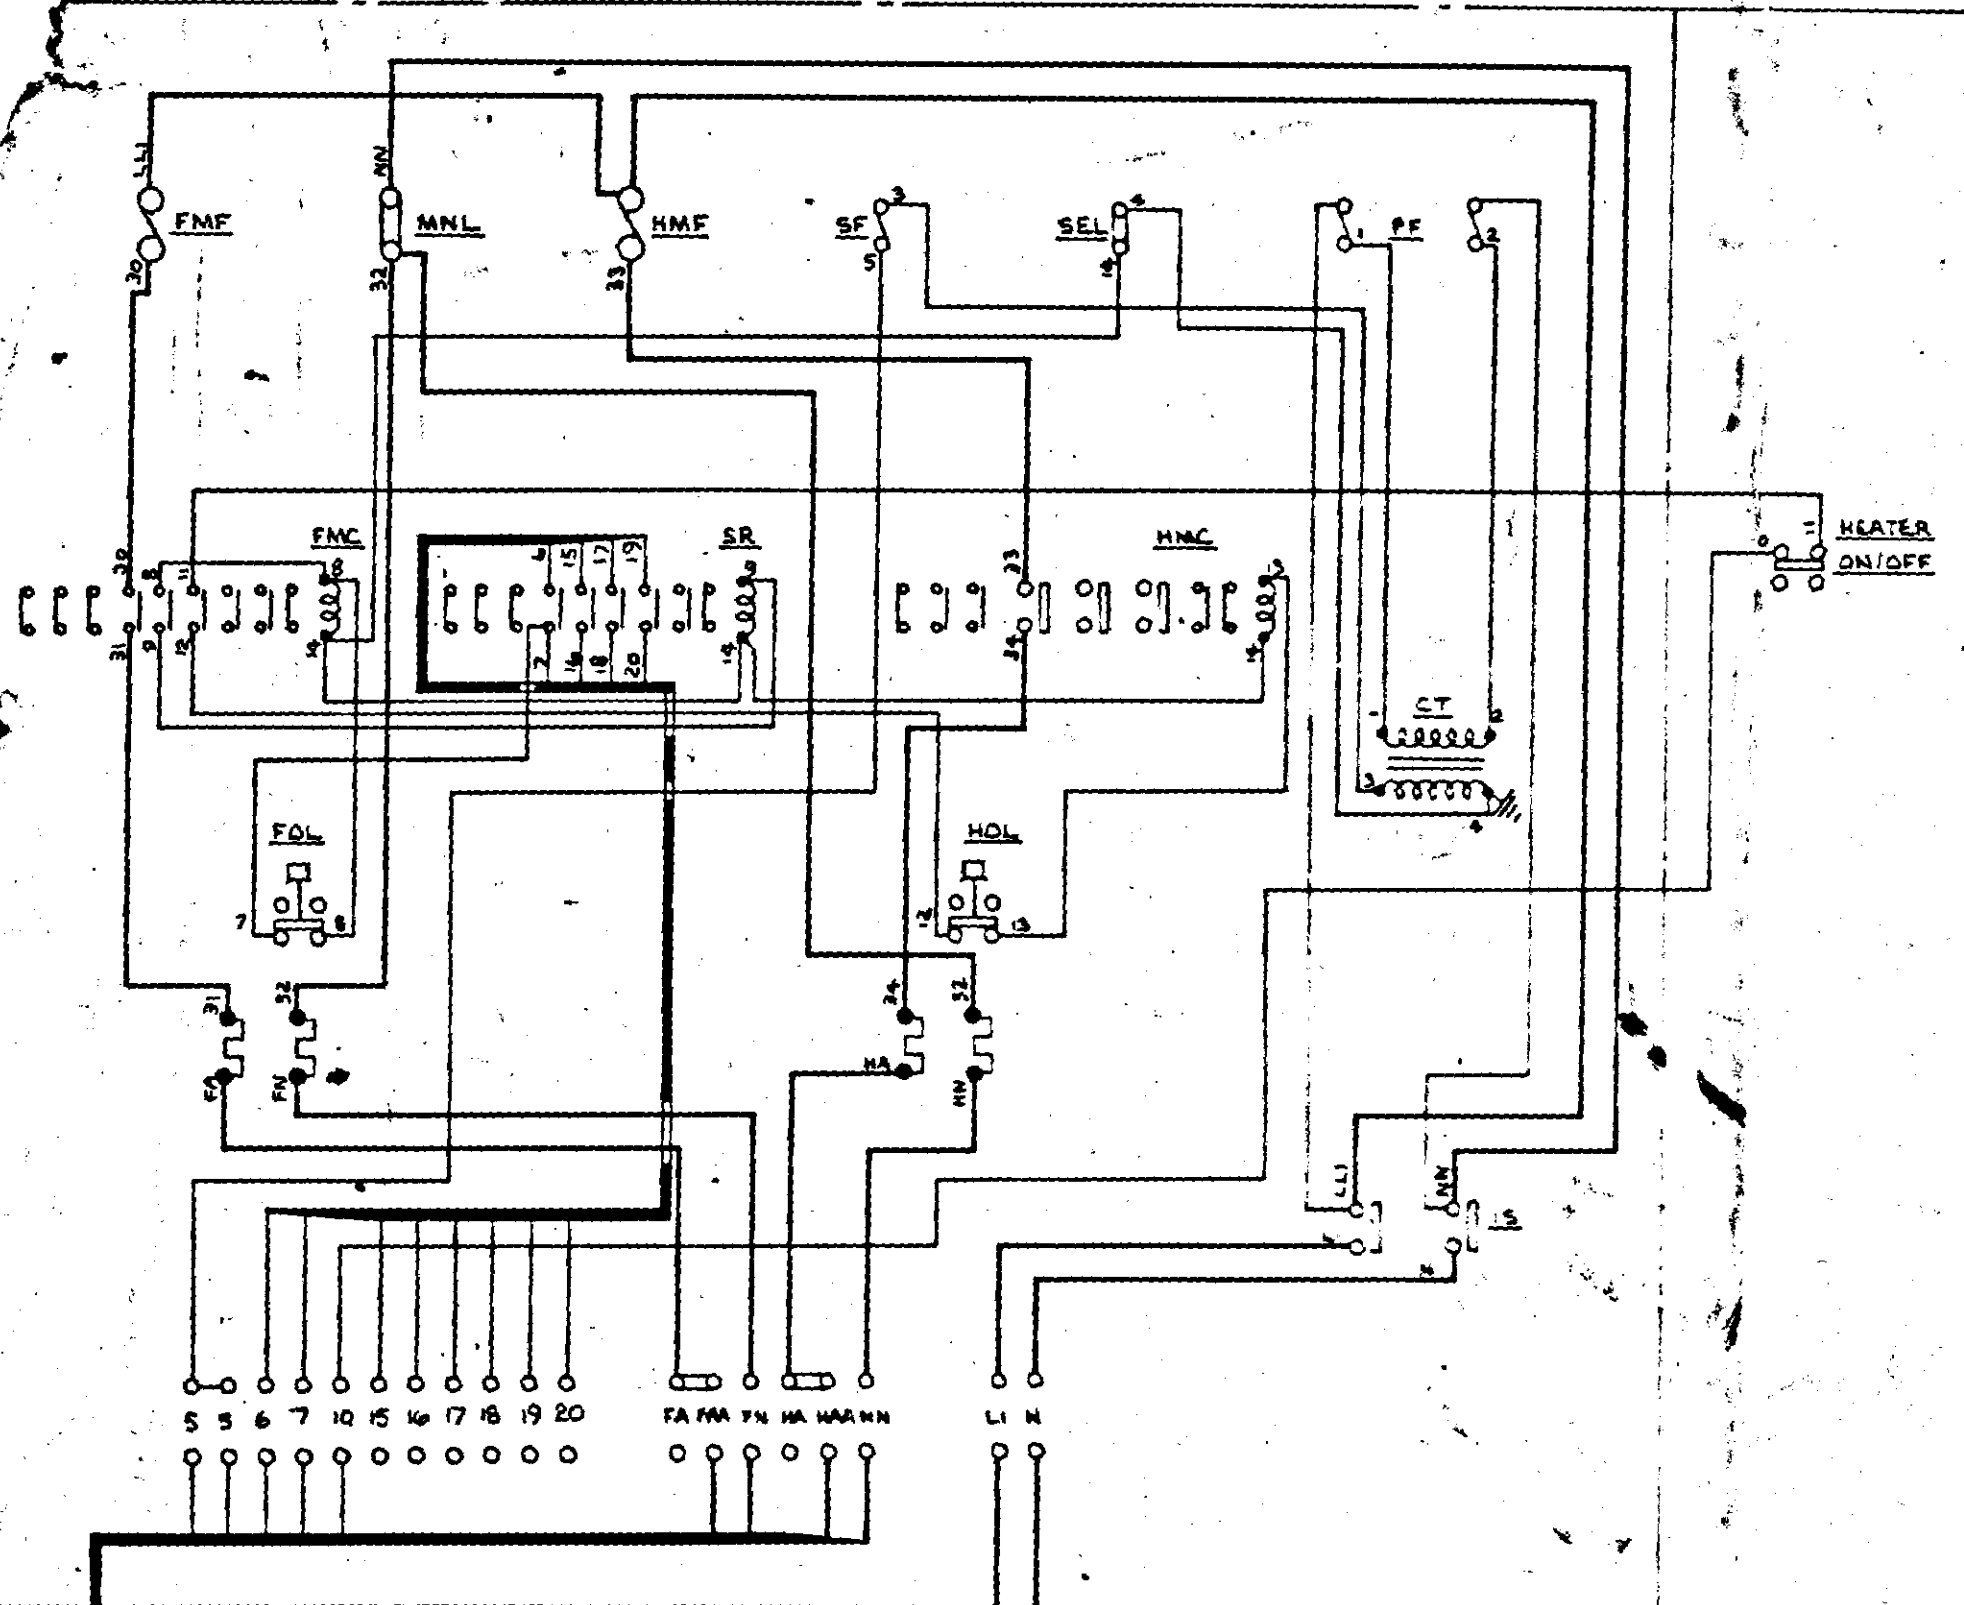


VIEW OF PANEL

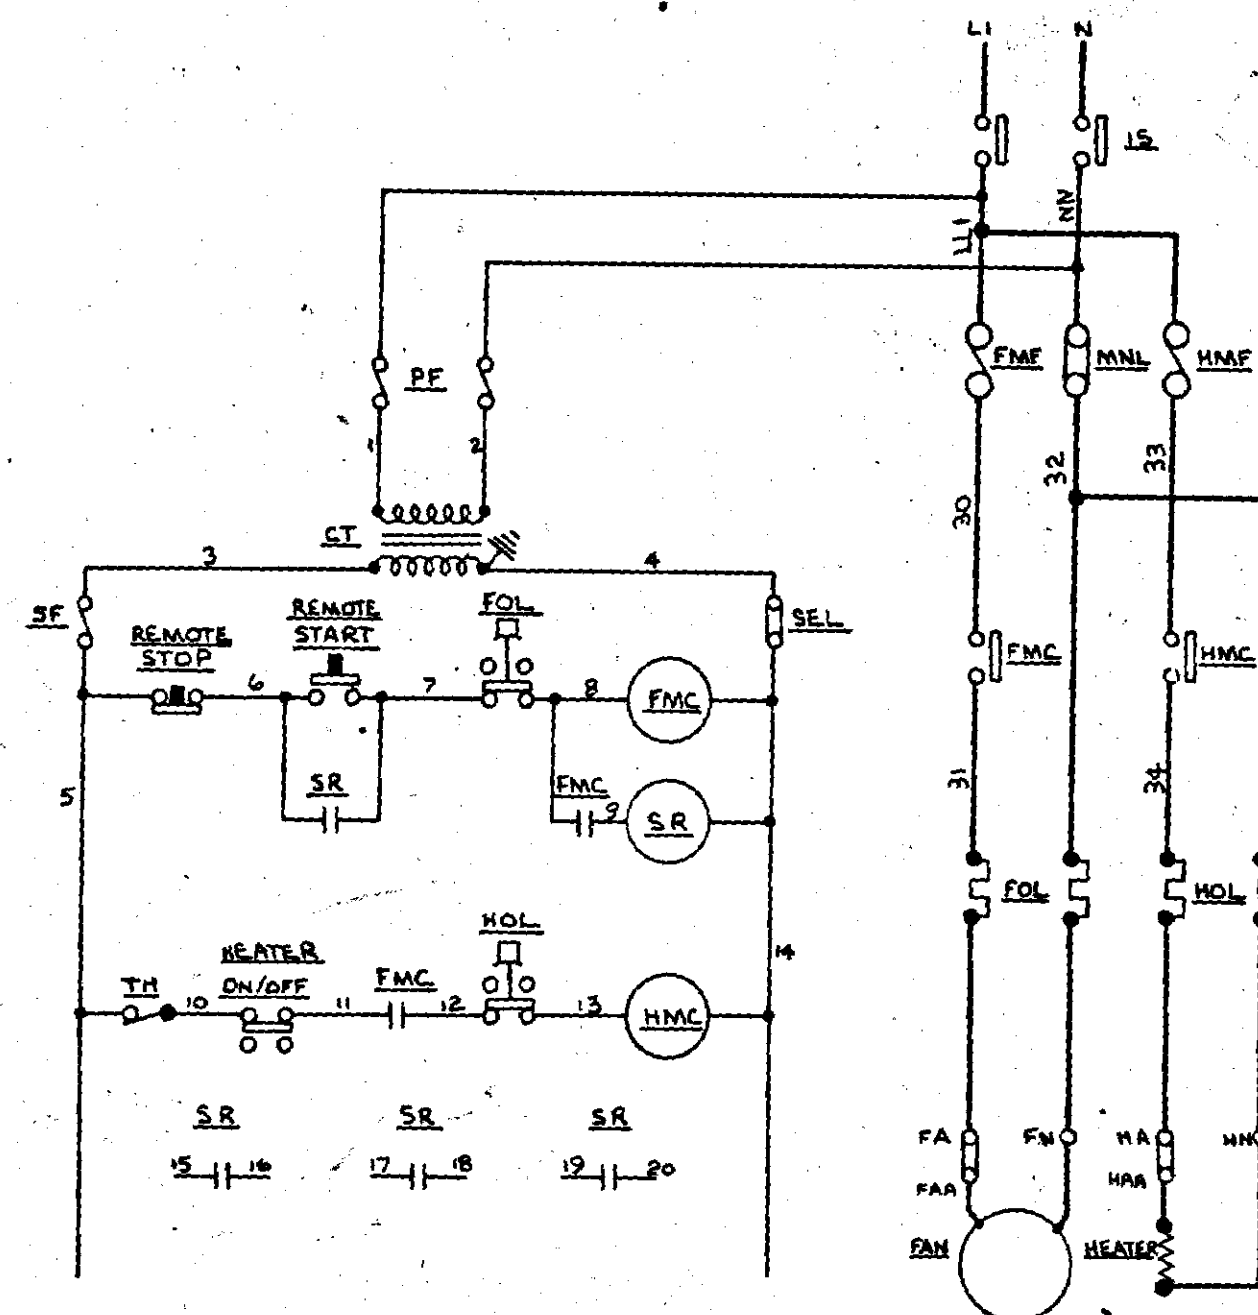

SUPPLY FROM DISTRIBUTION  
FUSE BOARD IN SCALE ROOMS

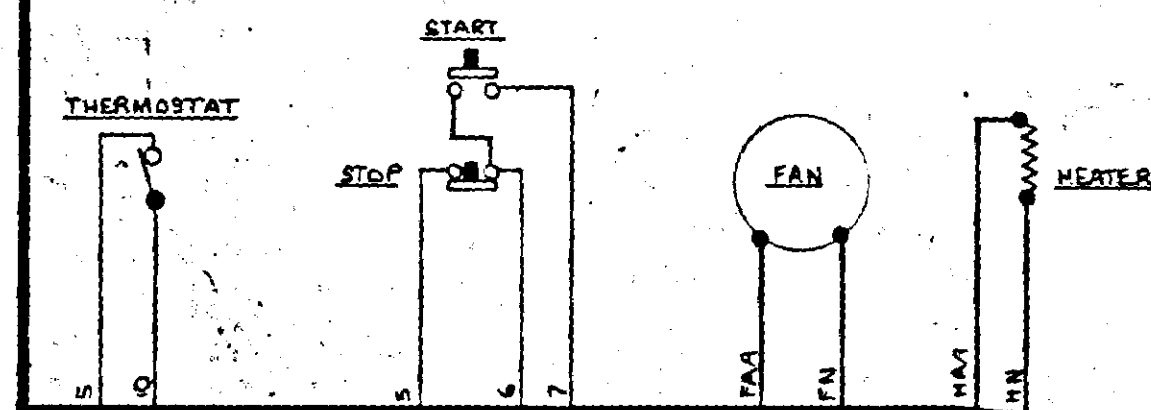

|     |                       |         |           |
|-----|-----------------------|---------|-----------|
| CT  | CONTROL TRANSFORMER   |         |           |
| FMC | FAN MAIN CONTACTOR    |         |           |
| FMF | FAN MAIN FUSES        |         |           |
| FOL | FAN OVERLOAD          |         |           |
| HMC | HEATER MAIN CONTACTOR |         |           |
| HMF | HEATER MAIN FUSES     |         |           |
| HOL | HEATER OVERLOAD       |         |           |
| IS  | ISOLATOR              |         |           |
| PF  | PRIMARY FUSES         |         |           |
| SEL | SECONDARY EARTH LINK  |         |           |
| SF  | SECONDARY FUSE        |         |           |
| SR  | SLAVE RELAY           | CONTROL | 32/0.2 mm |
| TH  | THERMOSTAT            |         |           |
| MNL | MAIN NEUTRAL LINK     | MAINS   | 1/1.58 mm |

# SCHEMATIC PANEL & EXTERNAL WIRING DIAGRAM ROOM PRESSURISATION FAN & HEATER PANEL

THE DESIGN AND MANUFACTURING  
INFORMATION CONTAINED IN  
THIS DRAWING IS THE EXCLUSIVE  
RIGHT OF DEWHURST & PARTNER  
LTD. AND MUST NOT BE COPIED  
OR USED FOR MANUFACTURING  
PURPOSES.

ISSUE 1

QPF111A

QPF111A

DEWHURST & PARTNER LTD.

MELBOURNE WORKS

HOUNSLOW

REVISION

ORIGIN  
SGO

REVISION

ORIGIN  
SGD

DRAWN BY A.M.

DATE 9.12.70

CHECKED BY

APPROVED BY

DATE

KEY DIAG. No.

EXT. DIAG. No.

REL. DIAG. No.

PANEL LAYOUT No. QPF111A