
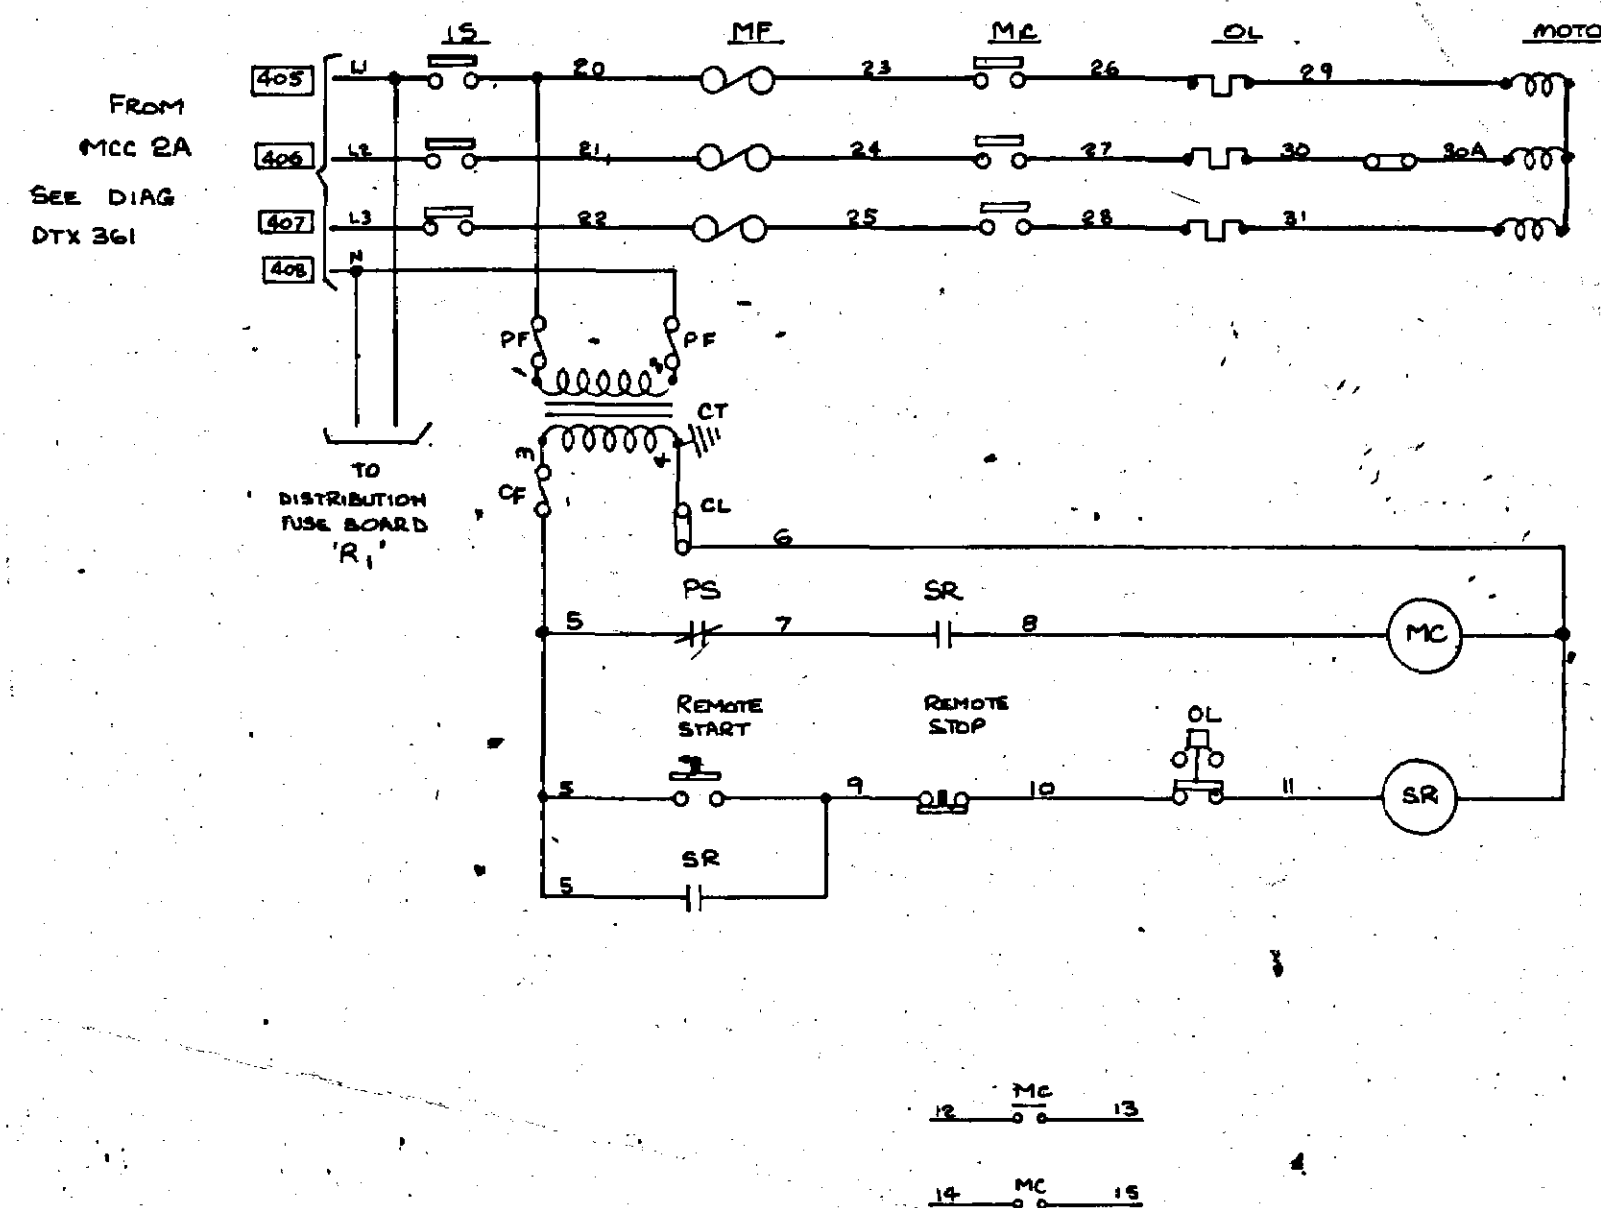


FRONT VIEW OF PANEL

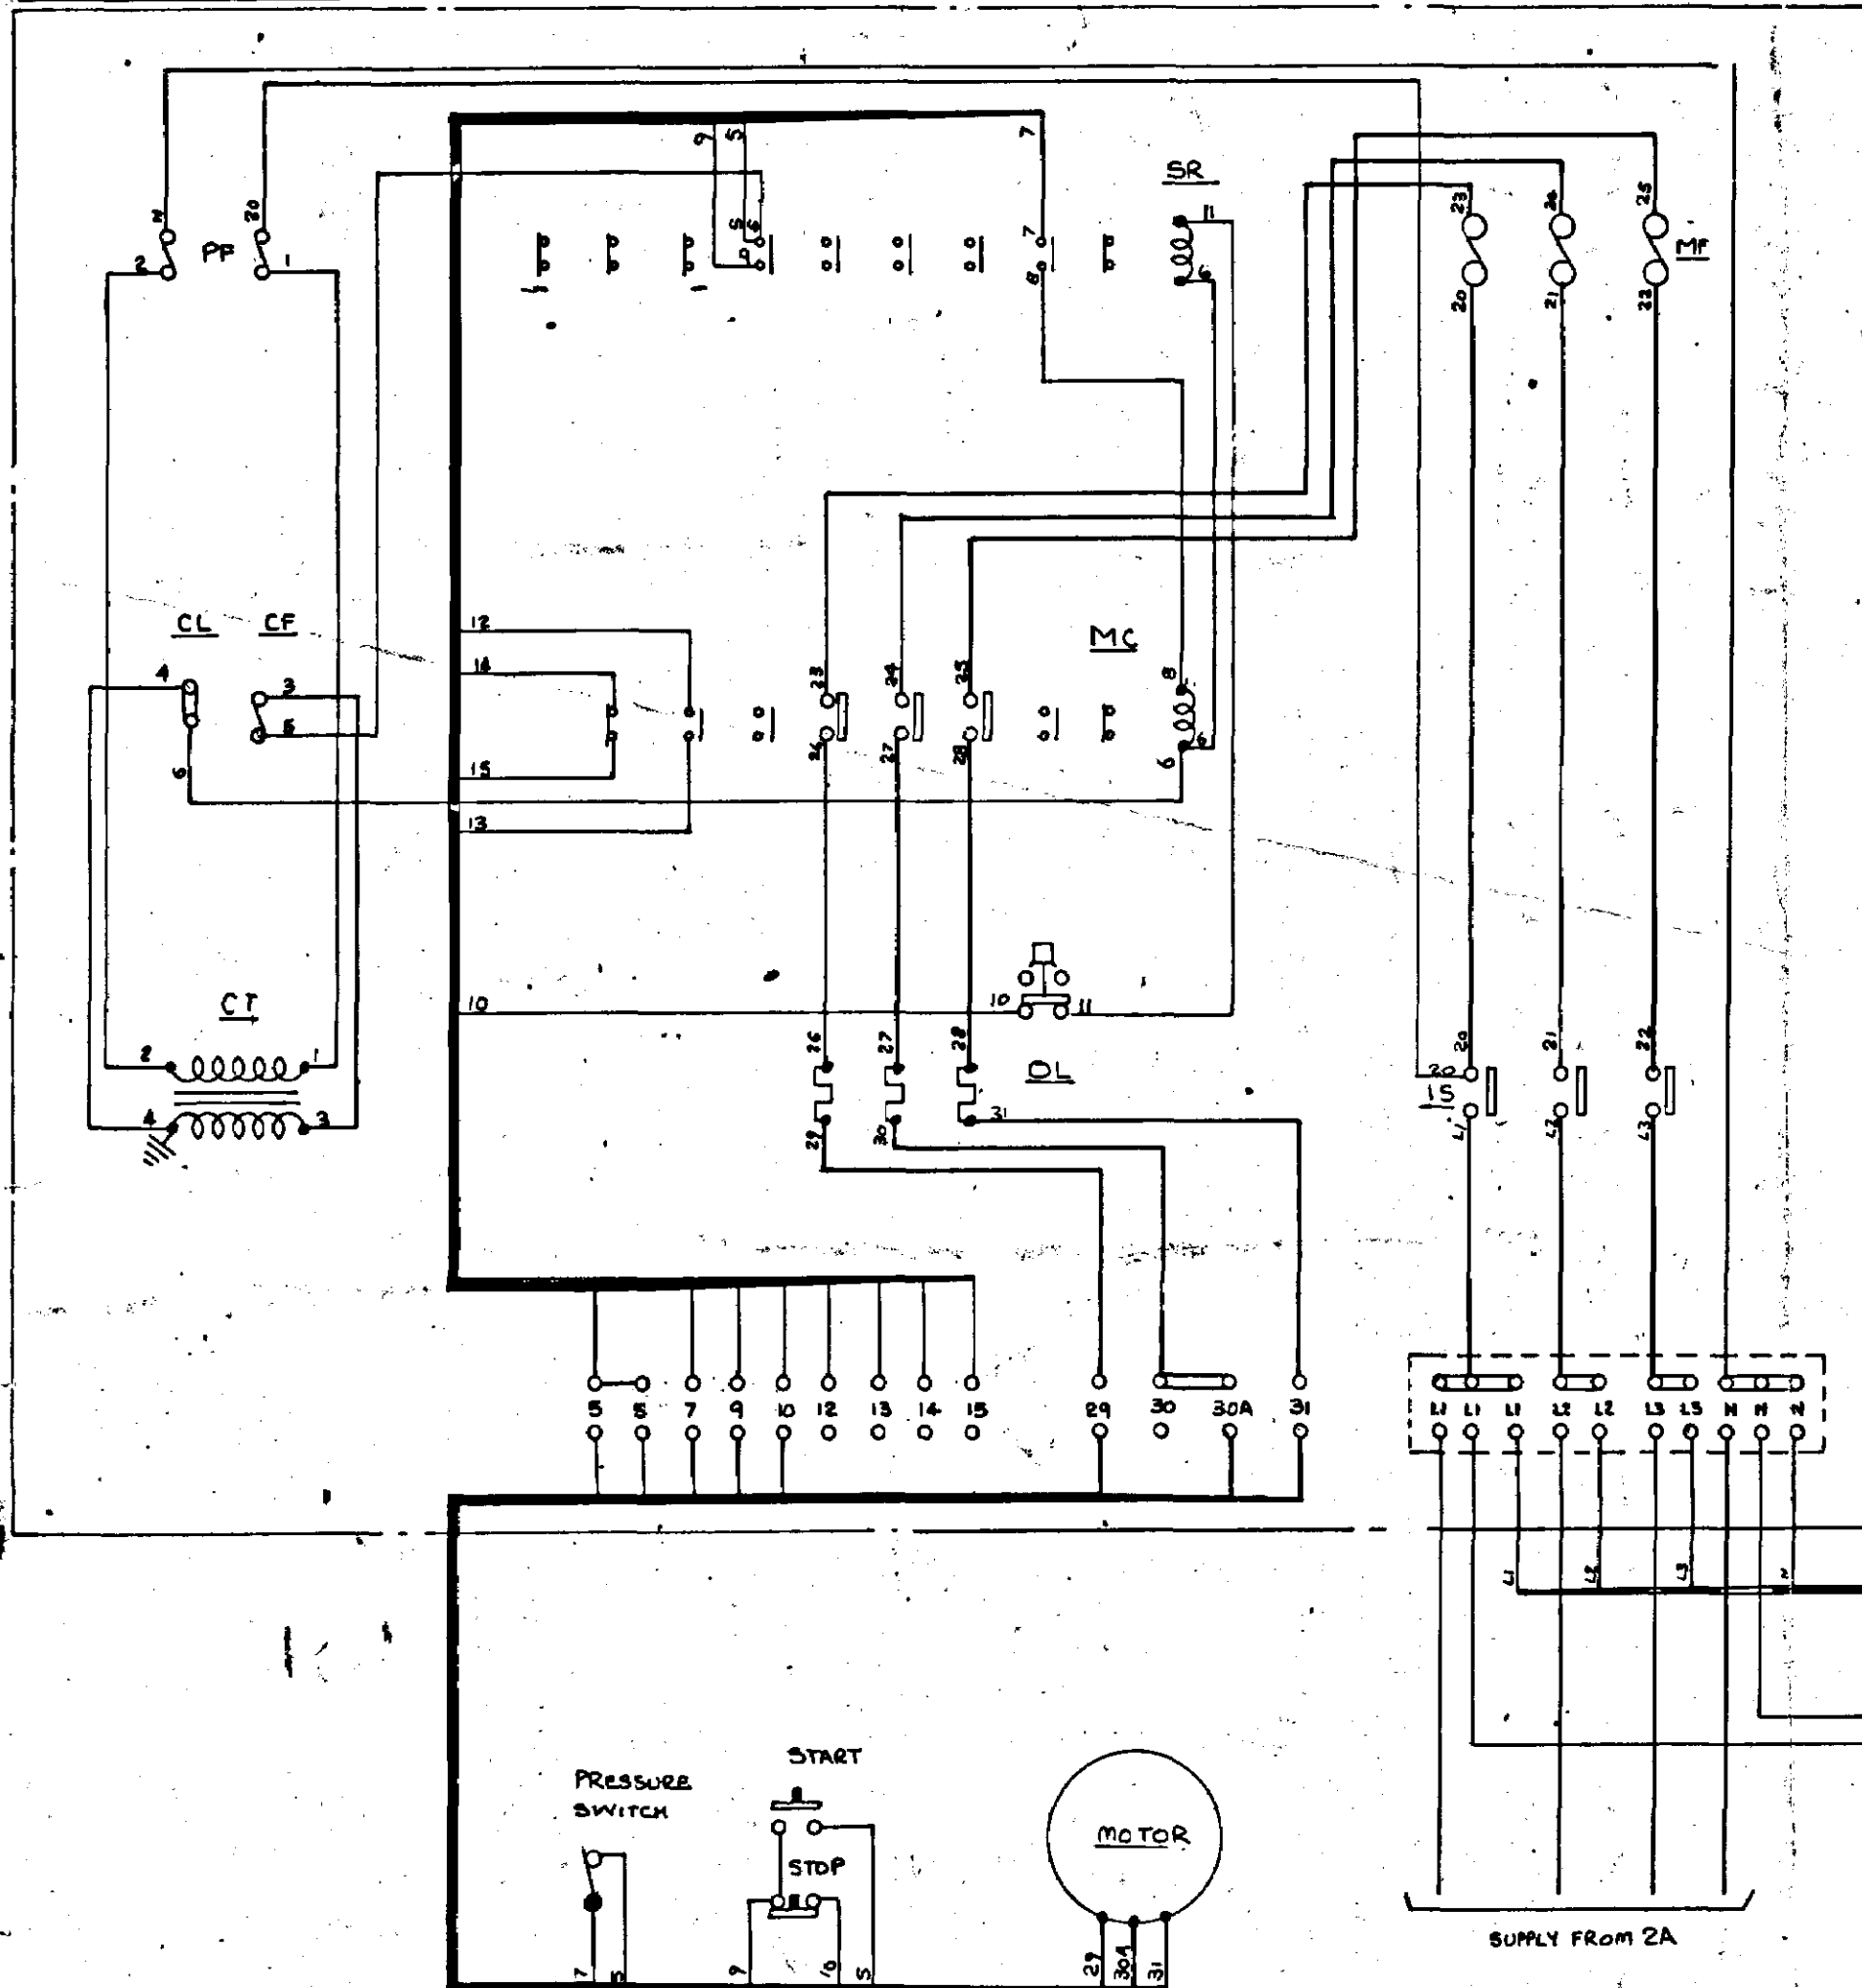

LORRY LOADING SCALE
COMPRESSOR No 2 AS No 1
EXCEPT INCOMING
TERMINALS

COMPRESSOR No 2

TO DISTRIBUTION
FUSE BOARD R.

SUPPLY FROM 2A

CF	CONTROL FUSE			
CL	CONTROL LINK			
CT	CONTROL TRANSFORMER			
IS	ISOLATOR			
MC	MAIN CONTACTOR			
MF	MAIN FUSES			
OL	OVERLOAD			
PF	PRIMARY FUSES			
PS	PRESSURE SWITCH			
SR	SUSTAINING RELAY			

	WIRING	STANDARD HELLERMAN COLOUR CODED WIRE MARKERS
	BLACK PVC	
CONTROL	32/0.2mm	1-15
MAINS	7/0.67mm	L1, L2, L3, N 20-31 30A

SCHEMATIC, PANEL & EXTERNAL WIRING DIAGRAM FOR LORRY LOADING SCALE COMPRESSOR

THE DESIGN AND MANUFACTURING
INFORMATION CONTAINED IN
THIS DRAWING IS THE EXCLUSIVE
RIGHT OF DEWHURST & PARTNER
LTD. AND MUST NOT BE COPIED
OR USED FOR MANUFACTURING
PURPOSES.

ISSUE 2

QTF 311 AD

QTF 311 AD

DEWHURST & PARTNER LTD.

MELBOURNE WORKS

HOUNSLOW

REVISION:

ORIGIN: / / SGD.

REVISION: 1

INCOMING TERMINALS
MODIFIED.

ORIGIN: ICD.
30/3/72 SGD. JS.

DRAWN BY: T. H. M. M.

DATE: 8/12/70

CHECKED BY:

APPROVED BY:

DATE:

KEY DIAG. No. -

EXT. DIAG. No. -

REL. DIAG. No. -

PANEL LAYOUT No. ETE 311AD