

10900

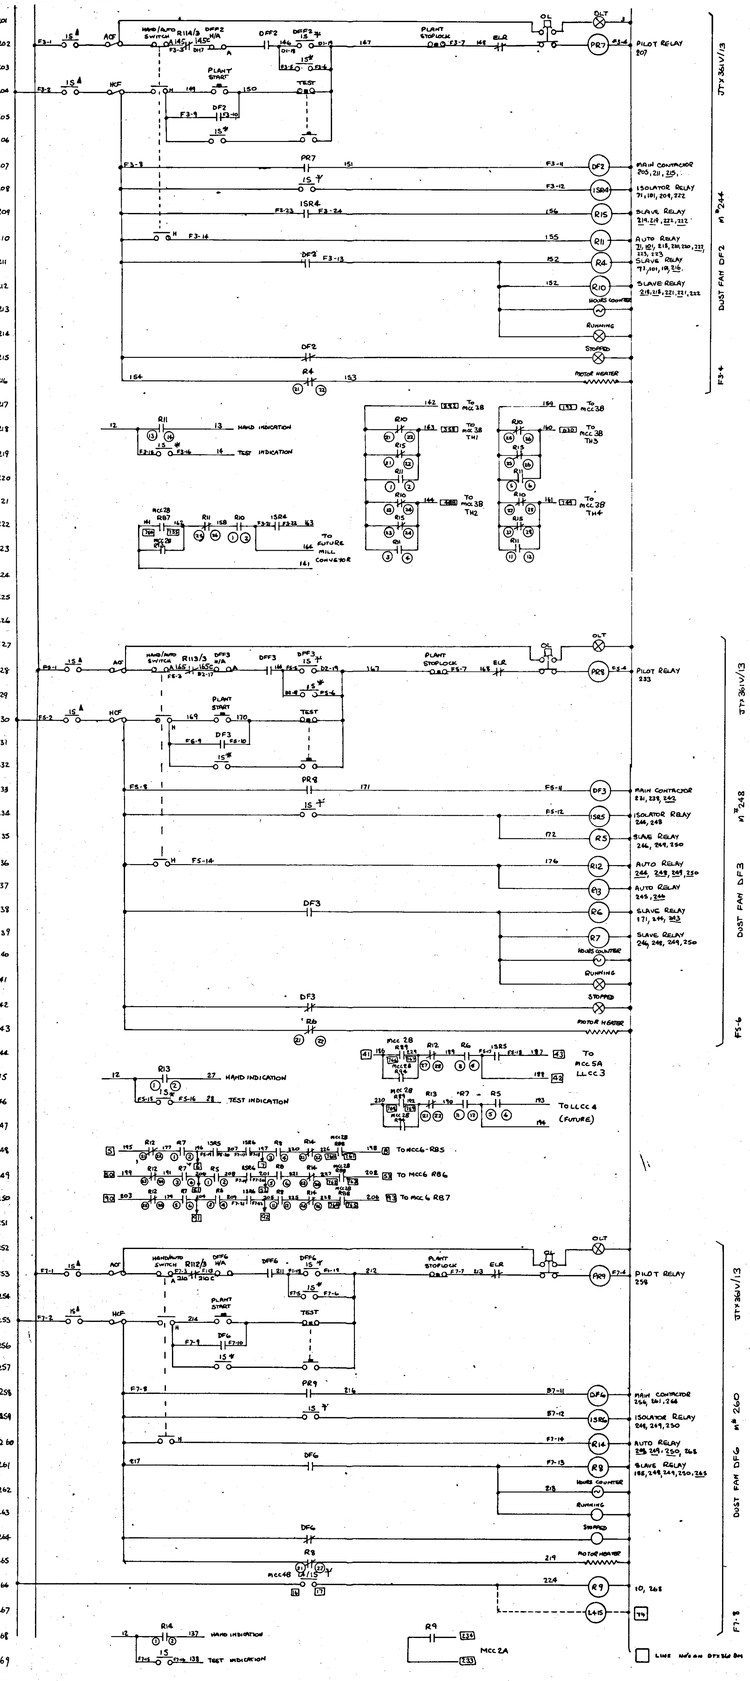

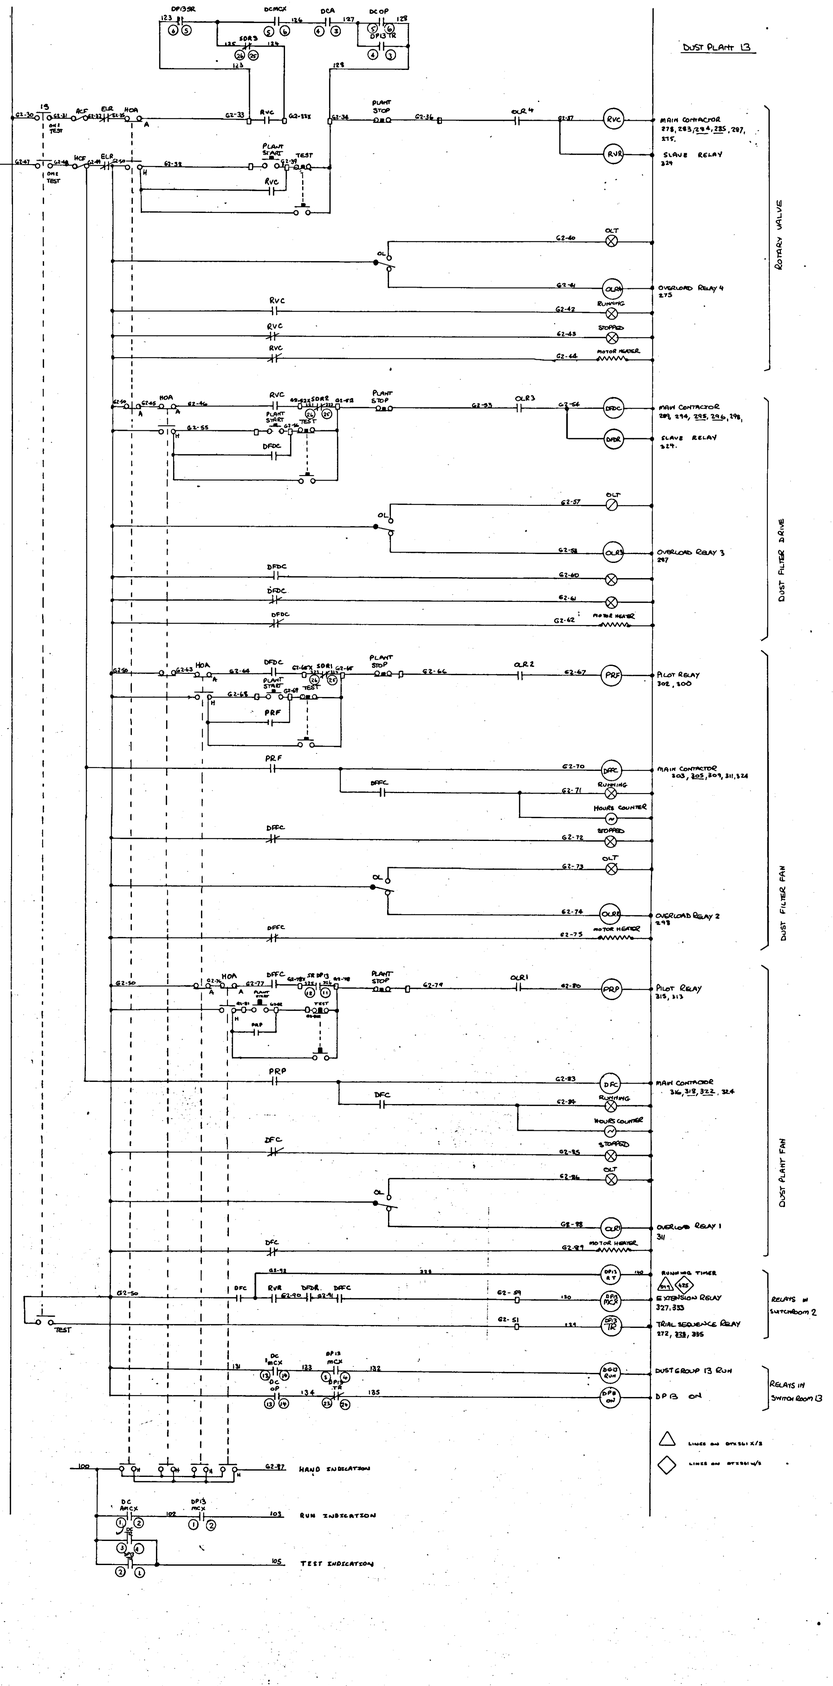

20A

10900

REVISION : 18	REVISION : 17	REVISION : 16	REVISION : 15	REVISION : 14	DRAWN BY A.M.	THE DESIGN AND MANUFACTURING INFORMATION CONTAINED IN THIS DRAWING IS THE EXCLUSIVE RIGHT OF DEWHURST & PARTNER LTD. AND MUST NOT BE COPIED OR USED FOR MANUFACTURING PURPOSES.	ISSUE 15 16 17 18 19 20 21		
ORIGIN : HD 15/1/76 SGD. A.J.T.B	ORIGIN : HD 14/1/77 SGD. A.J.T.B	ORIGIN : HD 13/1/77 SGD. A.J.T.B	ORIGIN : HD 17/1/77 SGD. A.J.T.B	ORIGIN : HD 21/1/77 SGD.	DATE 26/1/77		DTX 361Y/2		
					CHECKED BY	KEY DIAG. No.			
					APPROVED BY	EXT. DIAG. No. STA 361T			
					DATE	REL. DIAG. No.	DTX 361Y/2		
						PANEL LAYOUT No. HTX 361Y			

REVISION 20
Dust plant sequenced shut down—Mods on lines 202, 228, 253, 21-5-77

REVISION : 19
ALM & SGB Lamping wires for hand ind. hours counter and spigot used.
ORIGINATED 8/1/76 A.J.T.B

DEWHURST & PARTNER LTD.
MELBOURNE WORKS HOUNSLOW

TITLE: SCHEME FOR MCC 2C - SEAFORTH GRAIN TERMINAL

BAF 1266/74