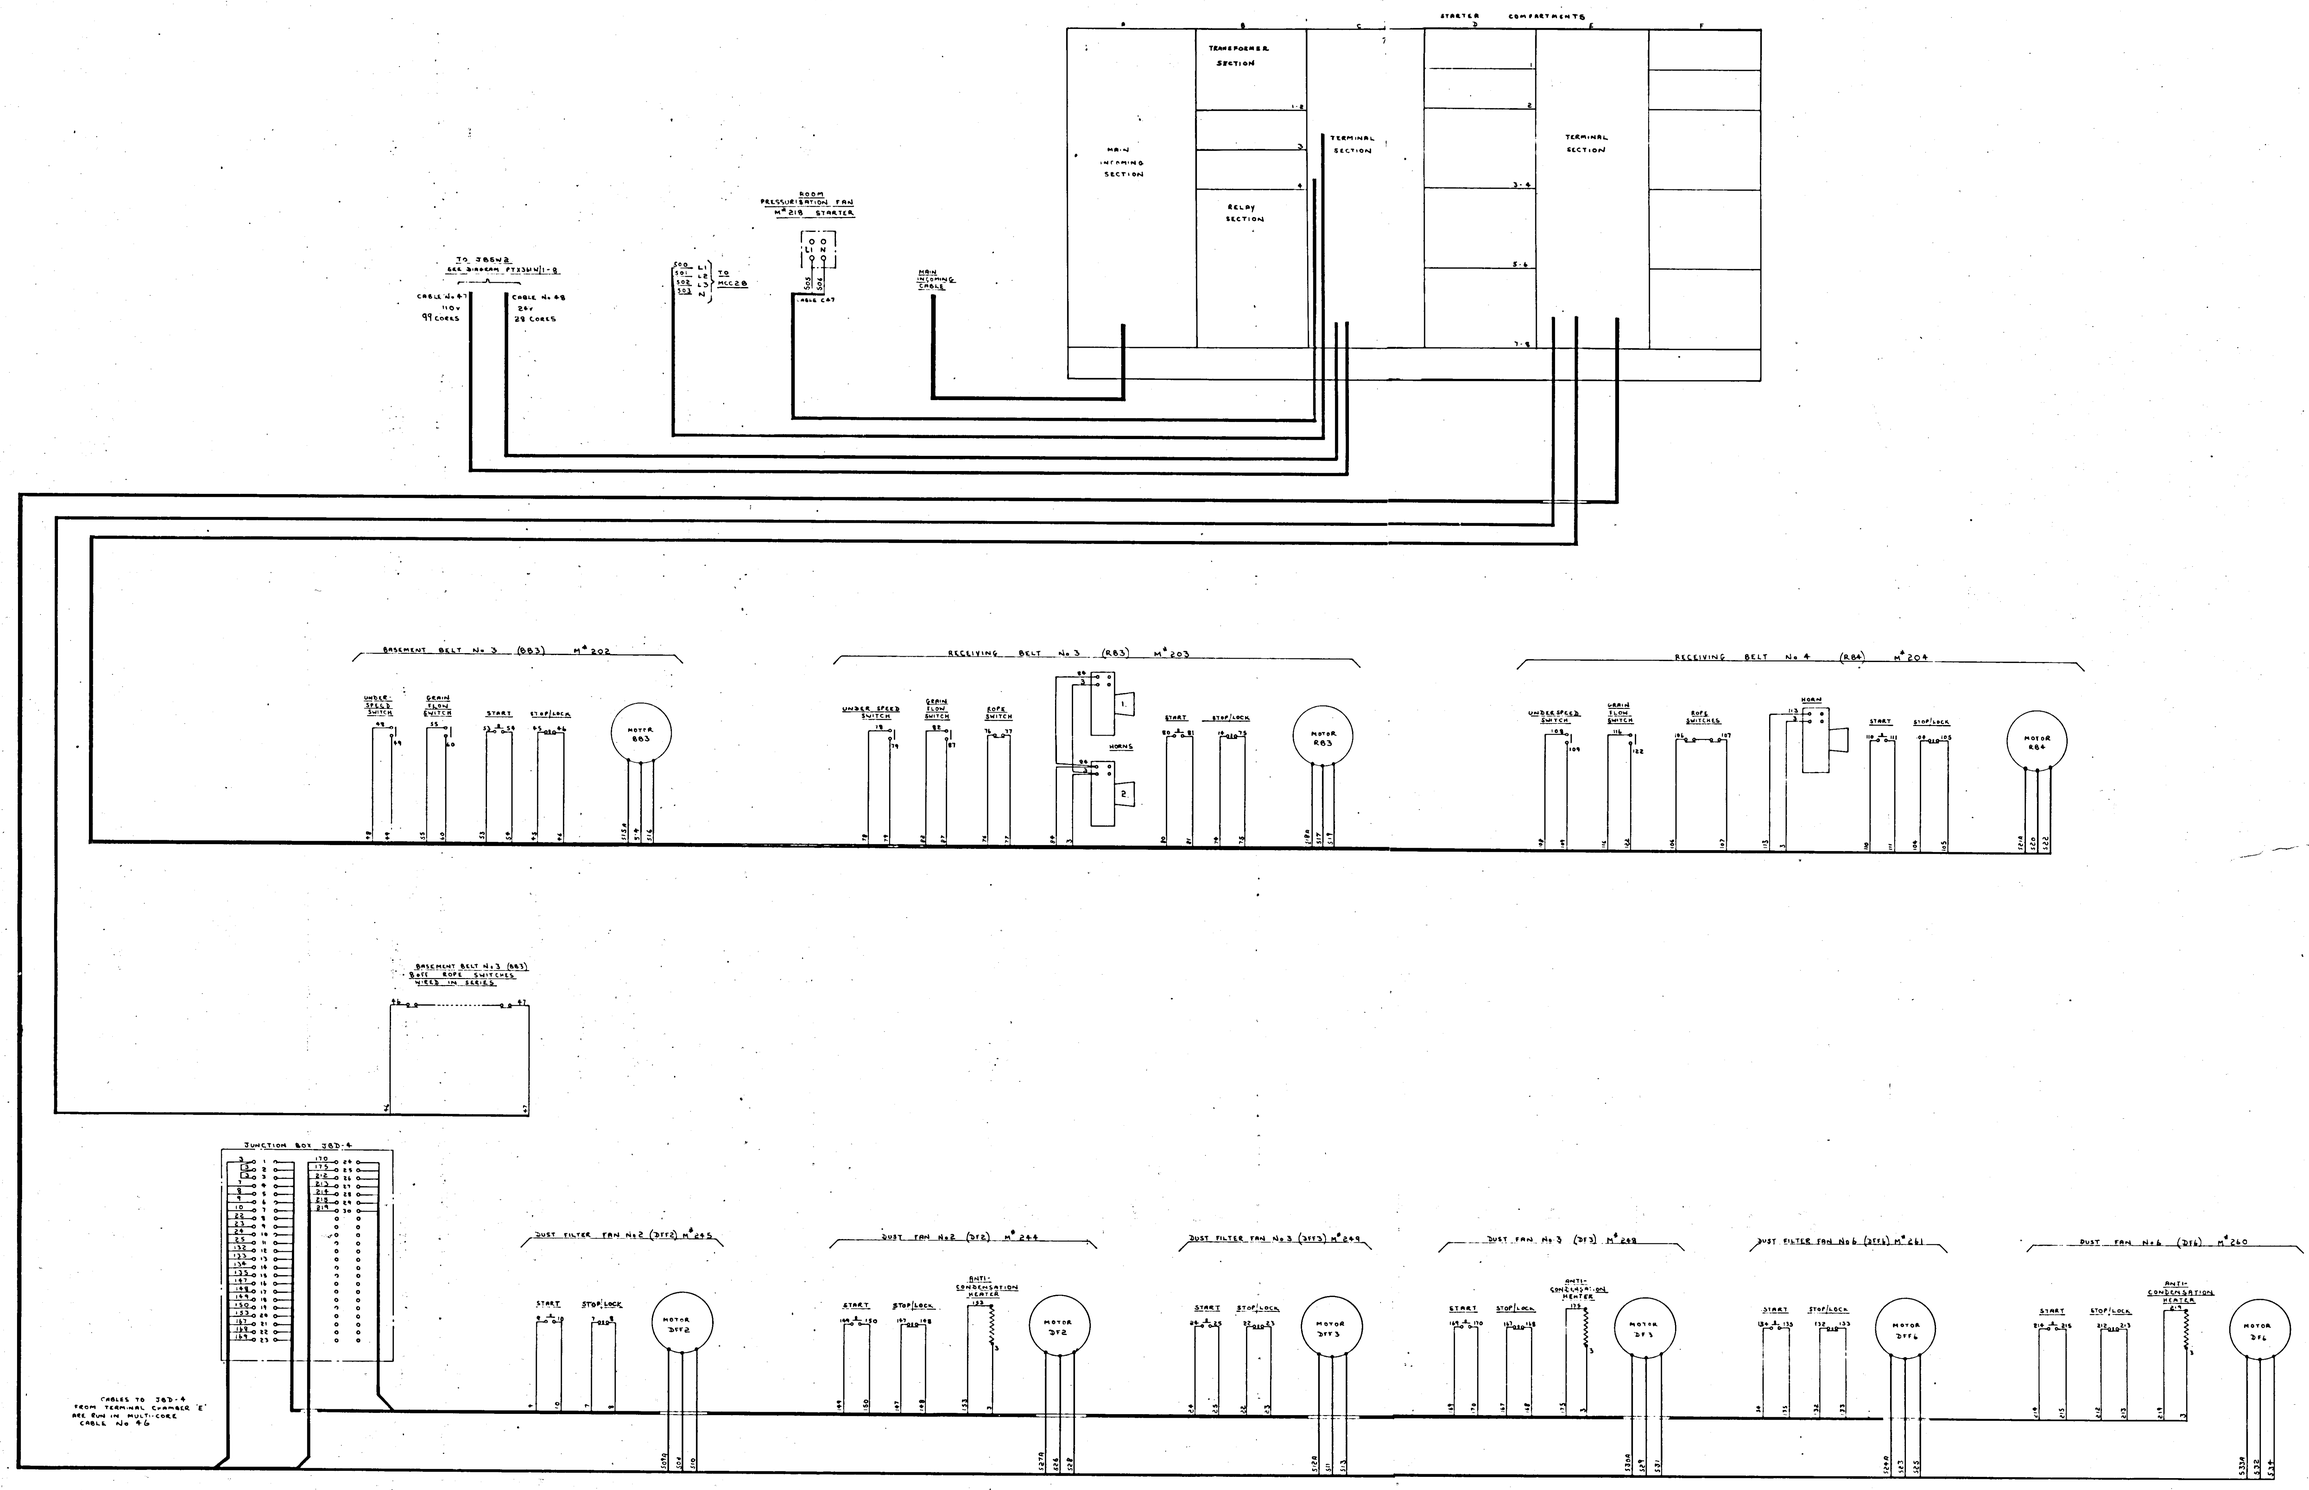


NUMBERS ADJACENT TO LOOMS INDICATE TERMINAL DESIGNATION ONLY – NOT WIRE NUMBERS

EXTERNAL WIRING DIAGRAM FOR MCC 2C - SEAFORTH GRAIN TERMINAL

THE DESIGN AND MANUFACTURING INFORMATION CONTAINED IN THIS DRAWING IS THE EXCLUSIVE RIGHT OF DEWHURST & PARTNER LTD. AND MUST NOT BE COPIED OR USED FOR MANUFACTURING PURPOSES

ISSUE 1 2 3 4 5

STX361Y

STX361Y

DEWHURST & PARTNER LTD.
MELBOURNE WORKS HOUNSLOW

TITLE: EXTERNAL WIRING DIAGRAM FOR MCC 2C — SEAFORTH GRAIN TERMINAL

REVISION:	REVISION: 4	REVISION: 3	REVISION: 2	REVISION: 1	
ORIGIN:	ORIGIN: HCD	ORIGIN: CUST	ORIGIN: CUST	ORIGIN: CUST	DRAWN BY
/ / SGD.	18/5/72 SGD. HJC	3/5/72 SGD. BJ	24/4/71 SGD. JT	9/2/71 SGD.	DATE 23-11-71
	CABLE No 47 TO 385W2 INCREASED FROM 87 TO 99 CORES.	CABLE No 47 TO 385W2 INCREASED FROM 71 TO 87 CORES	B83 WORKS REMOVED. R83, R84 & R85 WORKS ADDED. COMMON CORE WORKS ADDED.	24v CORES WERE 40 OFF	CHECKED BY
					APPROVED BY
					DATE

KEY DIAG. No	393361T/1-2
EXT. DIAG. No	—— ——
REL. DIAG. No.	
PANEL LAYOUT No.	HTX361Y

ADMEC 4917